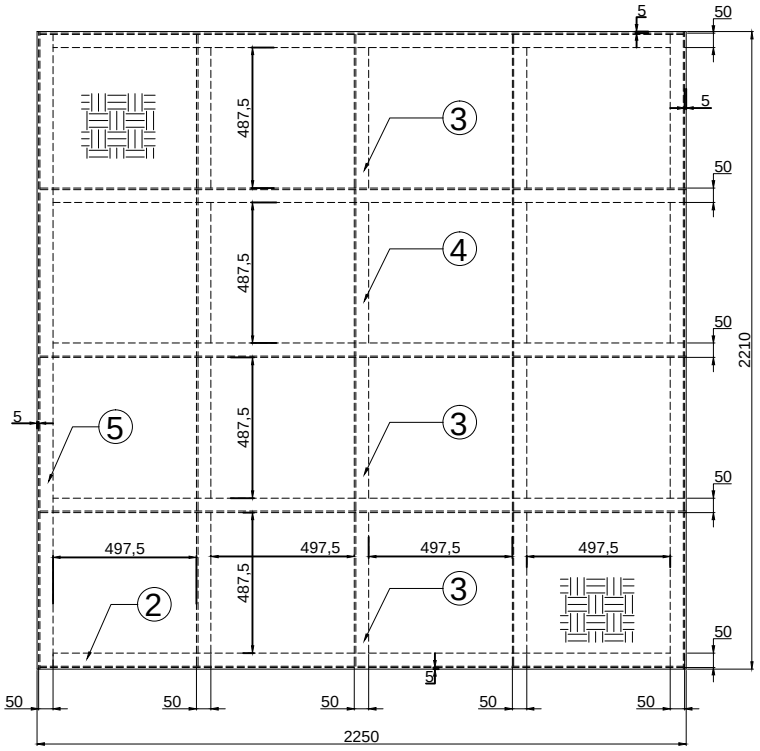

ELEVATION

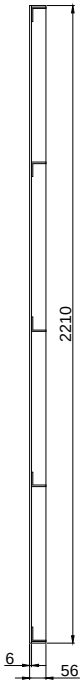

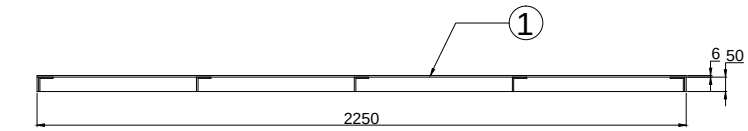

PLAN

SR NO	ITEM	SPECIFICATION	QTY	WEIGHT
1.	CHEQ. SHEET	2210 X 6 THK X 2250L	1 NO	235 KGS
2.	ISA	50 X 50 X 5 X 2230L(NOTCH)	5 NOS	42 KGS
3.	ISA	50 X 50 X 5 X 532L	9 NOS	18 NOS
4.	ISA	50 X 50 X 5 X 577L	3 NOS	7 NOS
5.	ISA	50 X 50 X 5 X 2200L	2 NOS	17 NOS

SIZE:

WIDTH	LENGTH	HEIGHT	QUANTITY
2210 mm	2250 mm	56 mm	07 NOS.

NIHVA TECHNOLOGIES PVT. LTD.

NIHVA TECHNOLOGY
PVT. LTD. PUNE
Email:- info@nihva.com
Website:- www.nihva.com

TITLE:

DOCK PIT ENCLOSER

CLIENT'S APPROVAL :

CLIENT -

PROJECT -

SITE LOCATION -

DWG. NO. : NIHVA/18-19/VDR/038

SCALE: NTS	WT: 317 kgs	SHEET:1 OF 1
DRAWN BY: PA		DATE: 14.06.2018
CHECK BY: SS		DATE: 14.06.2018

If any queries contact : design@nihva.com

NOTE: ALL DIMENSION ARE IN mm

THIS DRAWING & DESIGNING IS THE PROPERTY OF NIHVA TECHNOLOGIES. NOT BE SOLD OR COPY TO ANY OTHER CONCERN.