
REVISIONS				
ZONE	REV.	DESCRIPTION	DATE	APPROVED
	01	OUTFEED CONVEYOR LENGHT,HEIGHT & STRUCTURE MODIFIED.	16.08.2021	R.G

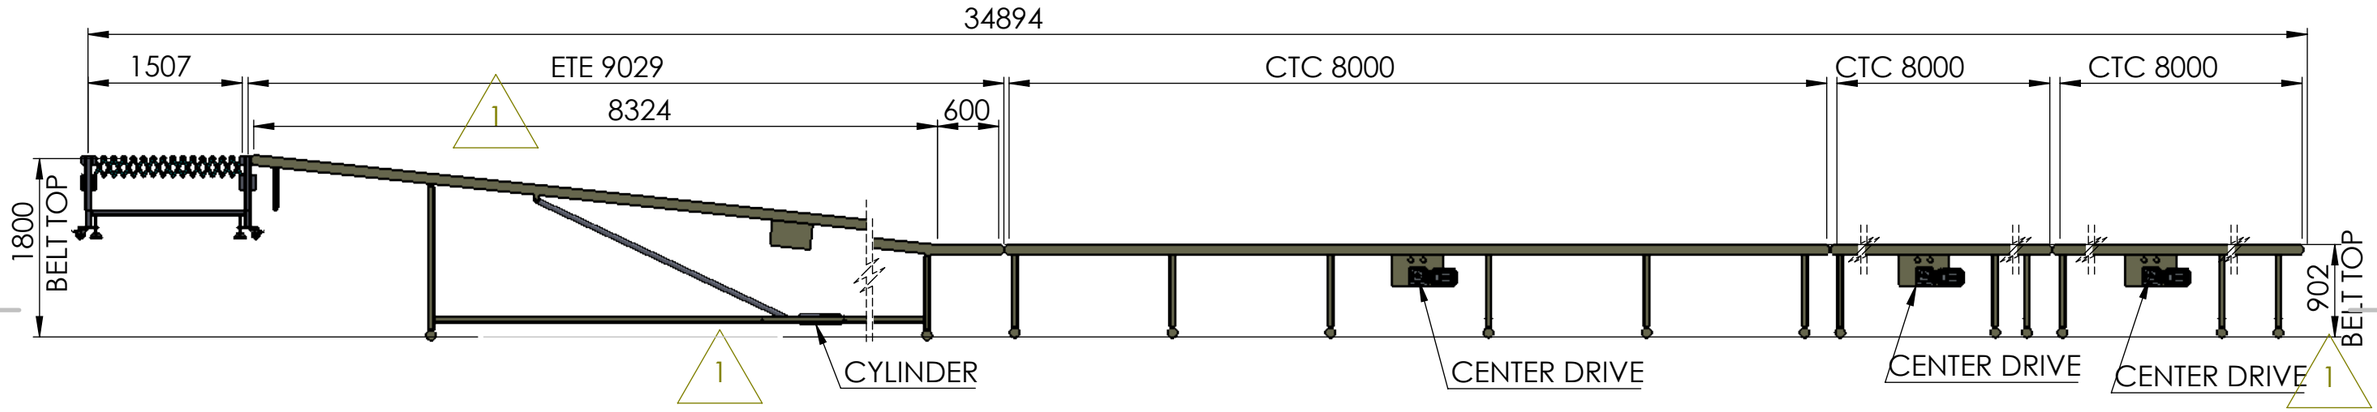

Use Tolerance as per ISO-2768 part 1&2:1989

UNLESS OTHERWISE SPECIFIED: DIMENSIONS ARE IN MILLIMETERS SURFACE FINISH: TOLERANCES: LINEAR: ANGULAR:	FINISH:				DEBURR AND BREAK SHARP EDGES	DO NOT SCALE DRAWING / REVISION
	NAME	SIGNATURE	DATE			NIHVA TECHNOLOGIES PVT LTD Email:-info@nihva.com Website:-www.nihva.com
DRAWN	ROHIT G		16-08-2021			TITLE:
CHK'D	ROHIT K		16-08-2021			
APPV'D	VT		16-08-2021			
MFG						
Q.A				MATERIAL:		DWG NO. LT1000067-KISLAY VEGI FARMS A3
				WEIGHT: GMS		SCALE:1:200 / SHEET 1 OF 2