


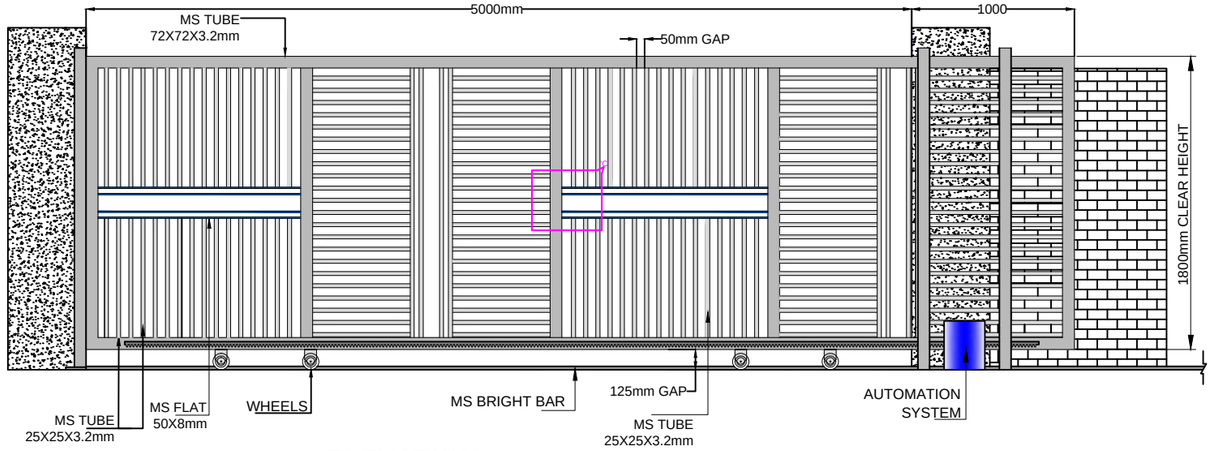


ELEVATION

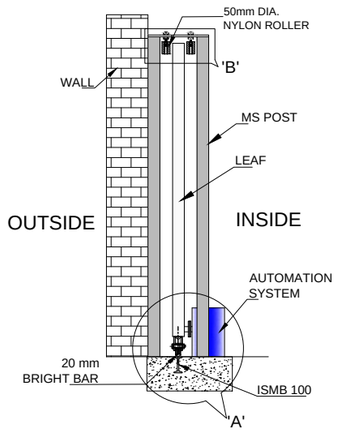


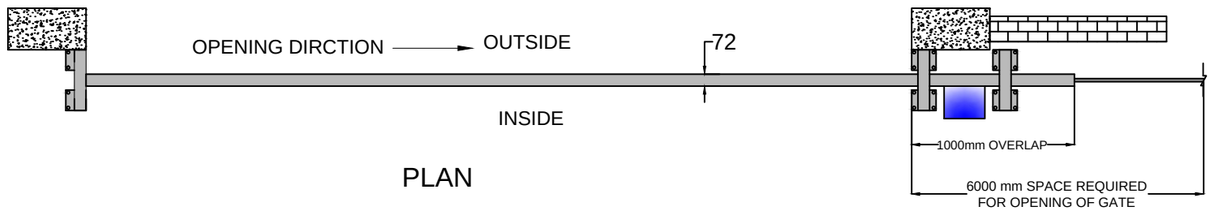


PLAN

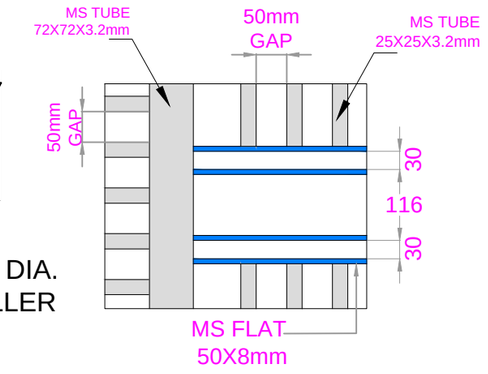

DETAIL VIEW OF 'C'.

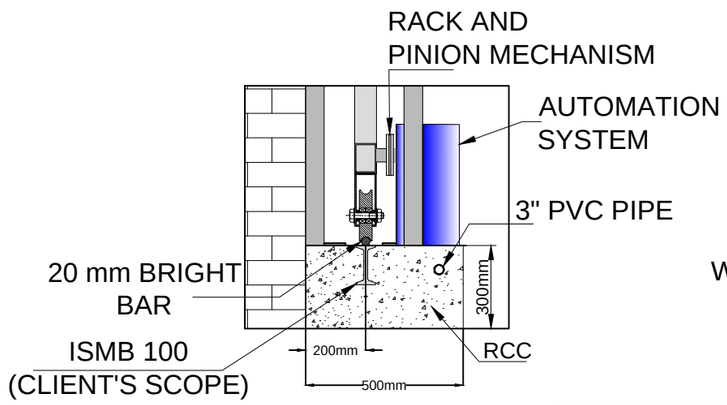

DETAIL VIEW OF 'A'.

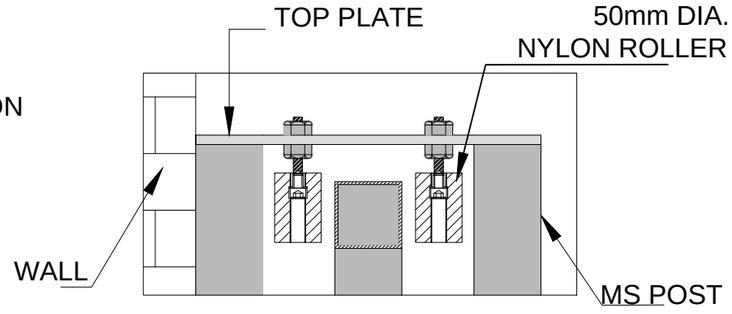

DETAIL VIEW OF 'B'.

TOLERANCE - ±10mm

NOTE-
1. ALL REQUIRED CIVIL WORK WILL BE IN CLIENTS SCOPE.
2. ONE COAT OF RED OXIDE & TWO COAT OF APPROVED RAL SHADE WILL BE GIVEN TO THE GATE.

SR NO	CLEAR WIDTH	CLEAR HEIGHT	QTY.
1	5000mm	1800mm	01NOS

This drawing & design is the property of NIHVA TECHNOLOGIES. Not to be sold or copied to any other concern.

TITLE
MOTORIZED SLIDING GATE

NIHVA
NIHVA TECHNOLOGIES PVT. LTD.

NIHVA TECHNOLOGIES
PVT. LTD. PUNE
Tel : 020 66304033
Email:- info@nihva.com
Website:- www.nihva.com

	NAME	SIGN	DATE
DRAWN	SURAJ		28-03-2018
CHECK	OMKAR		28-03-2018
APPRD.	SHEKHAR		28-03-2018

CLIENT - SCON PROJECT
PROJECT - ARI ARMATUREN STEAMLINE LLP
SITE LOCATION -PUNE
If any queries contact : design@nihva.com
DWG. NO. : NIHVA/17-18/0408
REV- 0
ALL DIMENSION ARE IN mm
SCALE: NTS
WT:
SHEET: 01 OF 01

29-03-2018 10:03:42