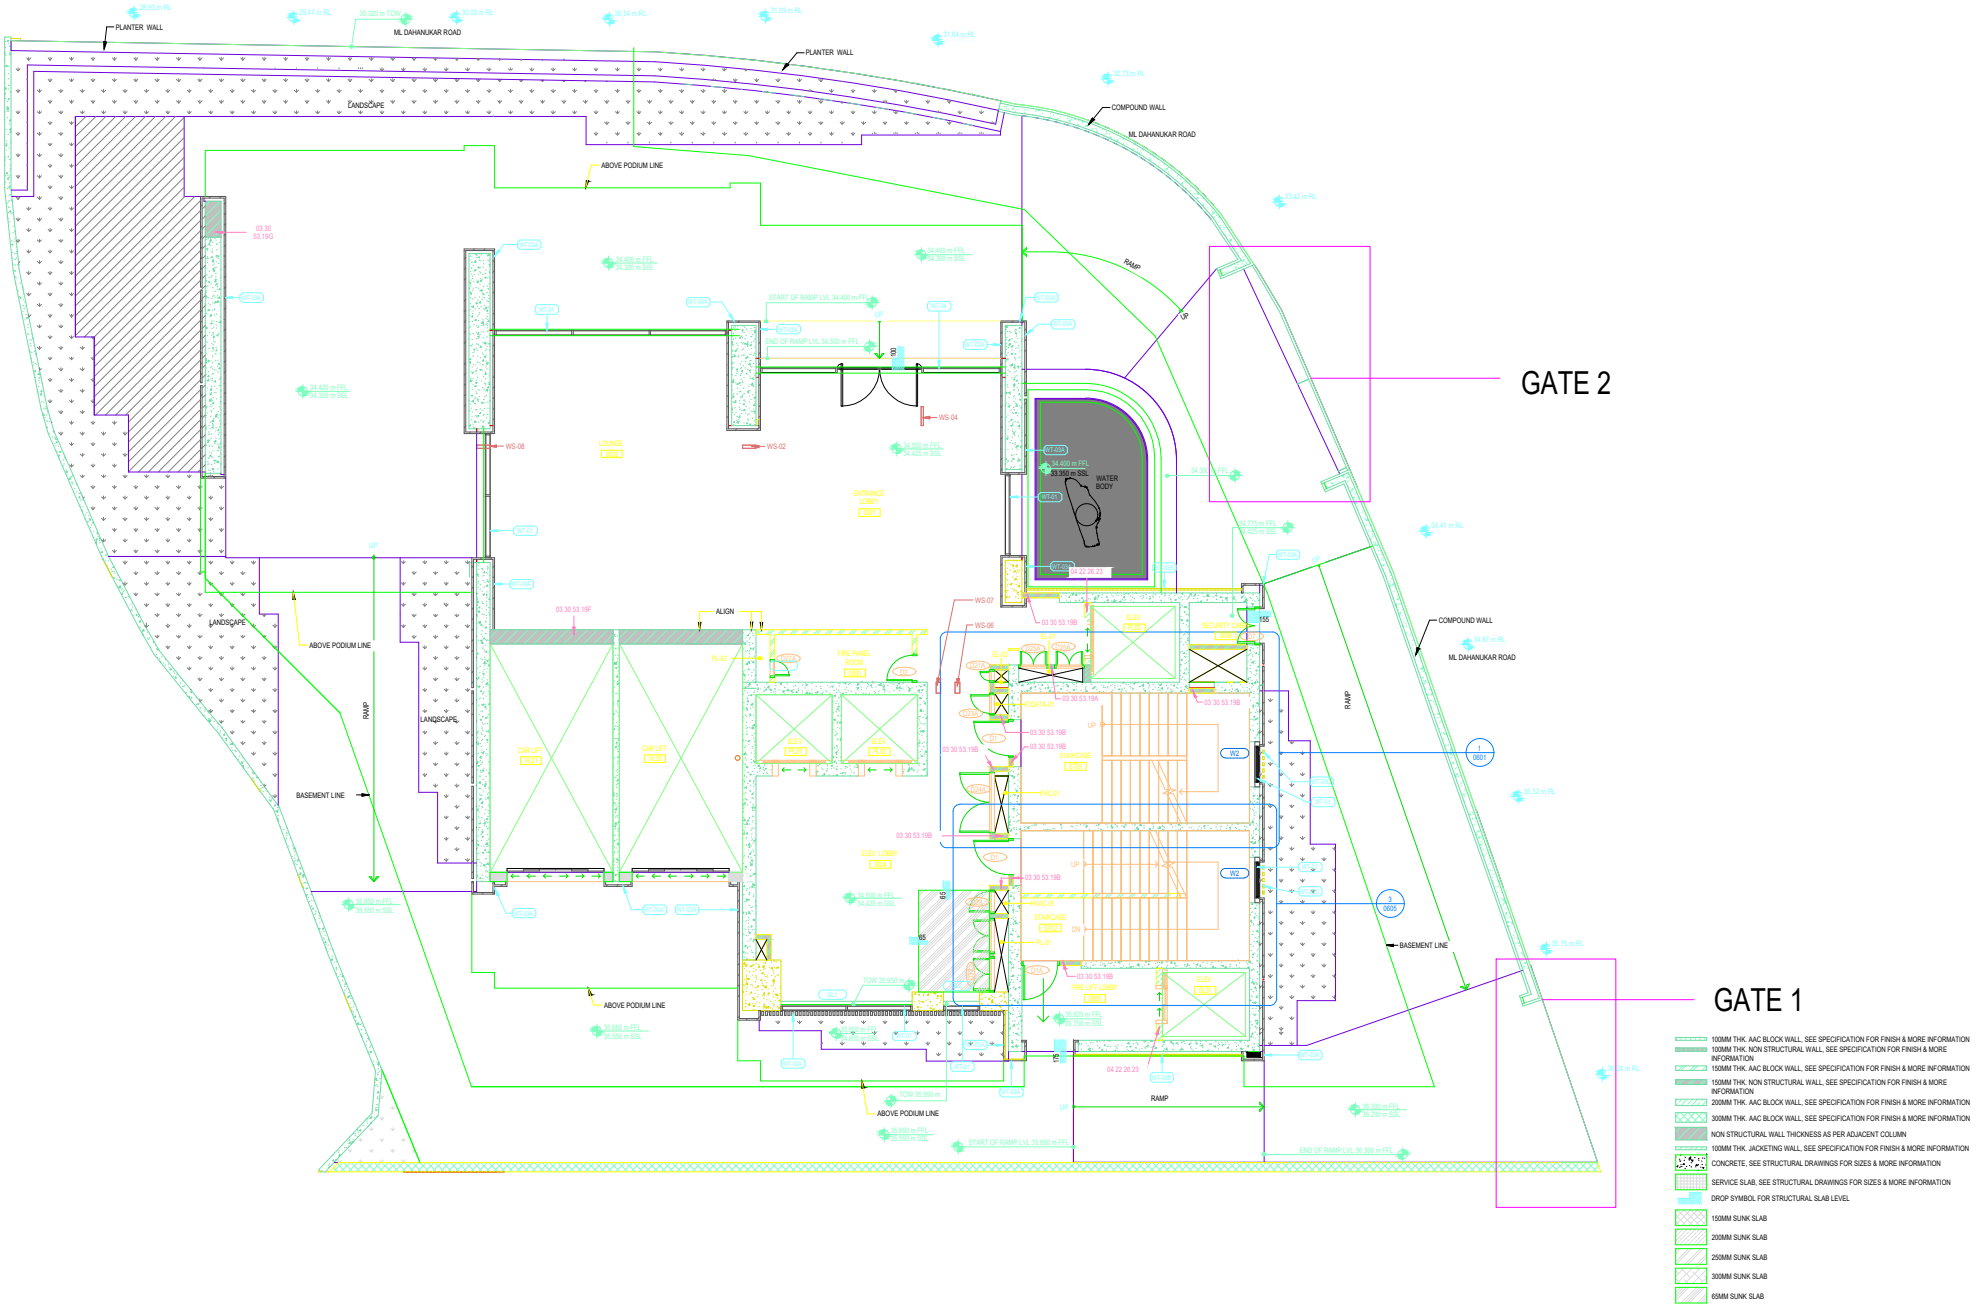

GATE 2
GATE 1
PLANTER WALL
ML DAHANUKAR ROAD
LANDSCAPE
COMPOUND WALL
ABOVE PODIUM LINE
RAMP
WATER BODY
LOUNGE
ENTRANCE LOBBY
FIRE PANEL ROOM
ELEV. LOBBY
STAIRCASE
FIRE LIFT LOBBY
CAR LIFT
BASEMENT LINE
ALIGN
100MM THK. AAC BLOCK WALL, SEE SPECIFICATION FOR FINISH & MORE INFORMATION
100MM THK. NON STRUCTURAL WALL, SEE SPECIFICATION FOR FINISH & MORE INFORMATION
150MM THK. AAC BLOCK WALL, SEE SPECIFICATION FOR FINISH & MORE INFORMATION
150MM THK. NON STRUCTURAL WALL, SEE SPECIFICATION FOR FINISH & MORE INFORMATION
200MM THK. AAC BLOCK WALL, SEE SPECIFICATION FOR FINISH & MORE INFORMATION
300MM THK. AAC BLOCK WALL, SEE SPECIFICATION FOR FINISH & MORE INFORMATION
NON STRUCTURAL WALL THICKNESS AS PER ADJACENT COLUMN
100MM THK. JACKETING WALL, SEE SPECIFICATION FOR FINISH & MORE INFORMATION
CONCRETE, SEE STRUCTURAL DRAWINGS FOR SIZES & MORE INFORMATION
SERVICE SLAB, SEE STRUCTURAL DRAWINGS FOR SIZES & MORE INFORMATION
DROP SYMBOL FOR STRUCTURAL SLAB LEVEL
150MM SUNK SLAB
200MM SUNK SLAB
250MM SUNK SLAB
300MM SUNK SLAB
65MM SUNK SLAB