
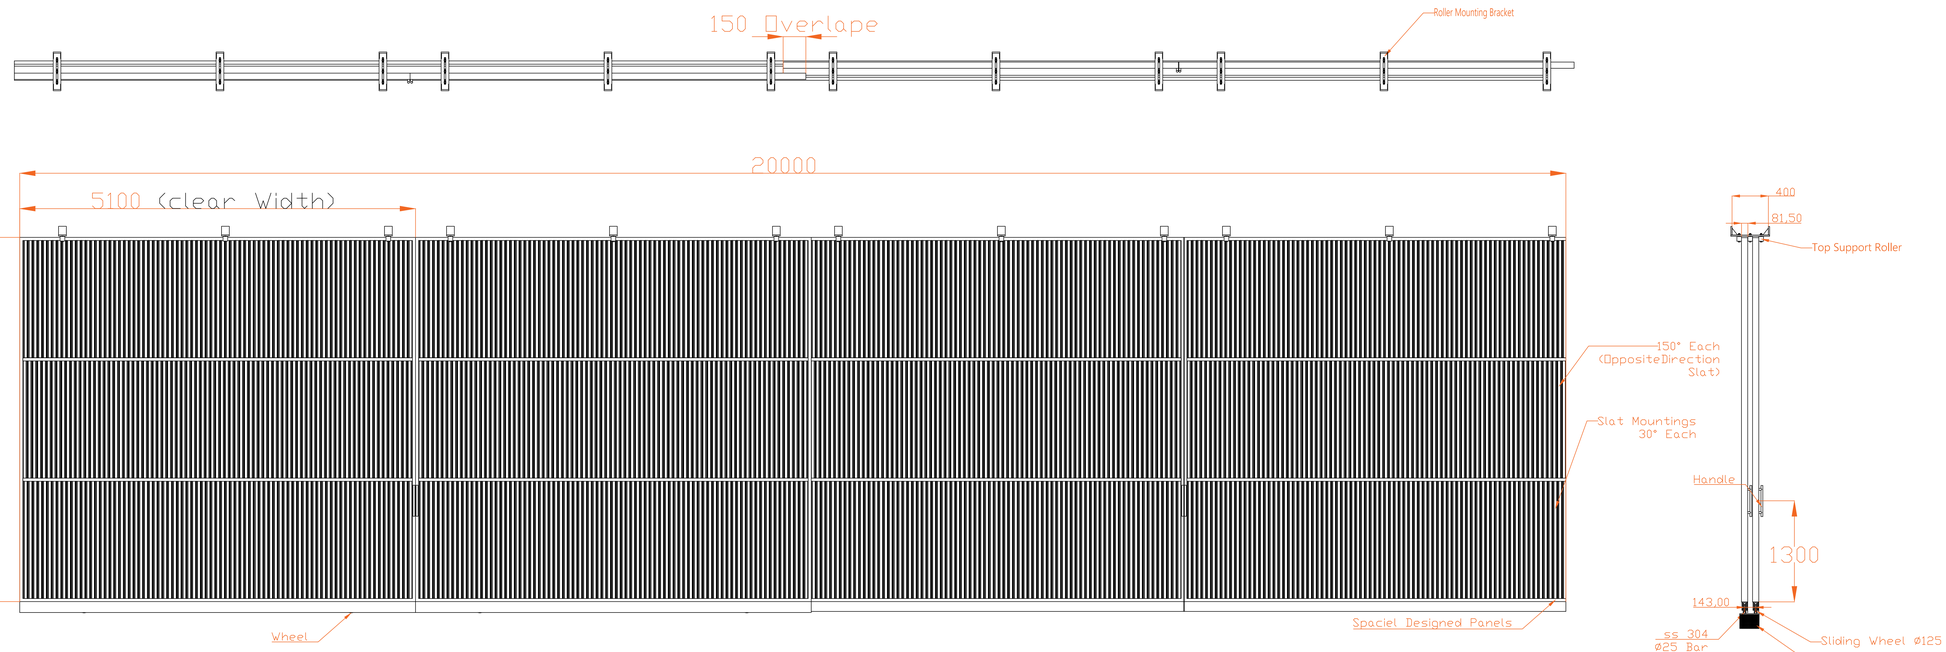


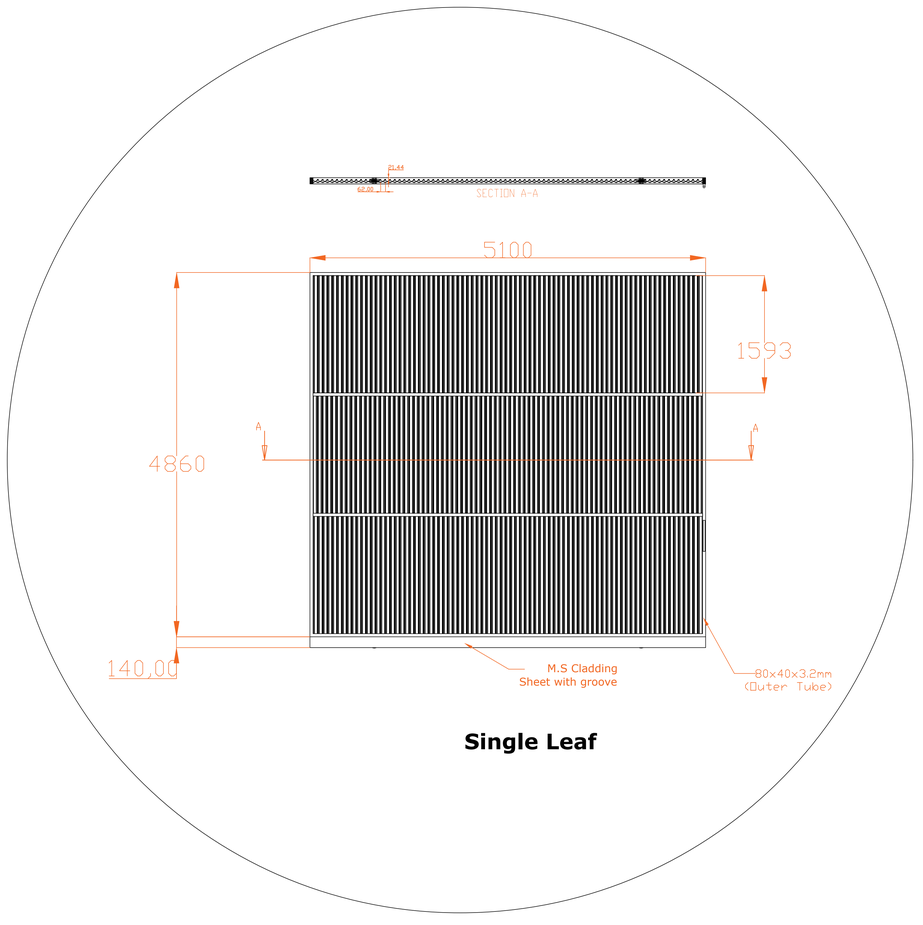

Single Leaf

Shown GA IS ONLY FOR 2 LEAFS

TECHNICAL SPECIFICATION:-

SR.	SPECIFICATION	DETAILS
1.	Slat	Straight 80 mm GI Sheet - 1.0 mm Thk.
2.	Leaf Size	5100 mm x 4860mm= 14 qty
3.	Overlap	Overlap considered 100 mm between 2 gates

This drawing & designing is the property of NIHVA TECHNOLOGIES. Not to be sold or copied to any other concern.

TITLE :- Manual Sliding Gate

NIHVA TECHNOLOGIES PVT. LTD.
NIHVA TECHNOLOGIES PVT. LTD. PUNE
Tel : 020 66304033
Email:- info@nihva.com
Website:- www.nihva.com

	NAME	DATE	
DRAWN	S.J	13/04/2024	CLIENT - Panchashil
CHECK	A.K.	13/04/2024	PROJECT - Manual Sliding Gate
APPROVAL	V.T.	13/04/2024	FORMAT NO - NIHVA-DD-F-03
			DWG. NO. : NIHVA/23-24/XX — REV-00
			SCALE: NTS — WT: — SHEET: 01 OF 01
ALL DIMENSION ARE IN mm			If any queries contact : design@nihva.com