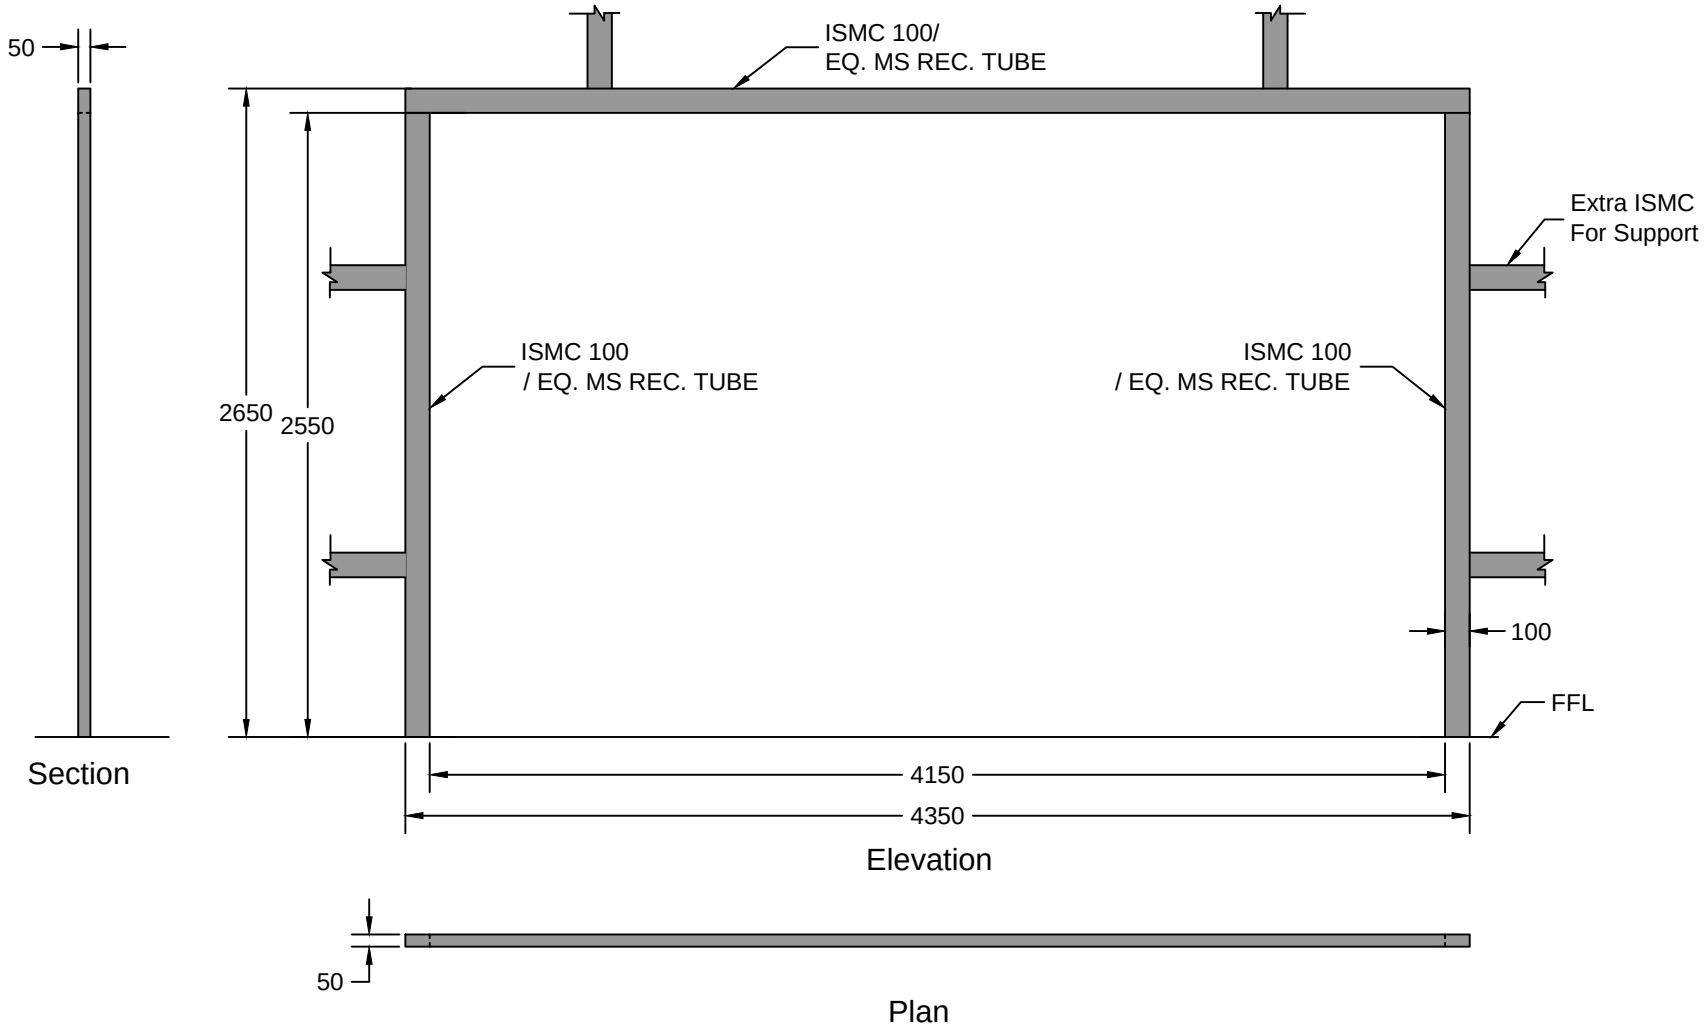


This drawing & design is the property of NIHVA TECHNOLOGIES. Not to be sold or copied to any other concern.

| | | |
|---|---|---|
| TITLE: Steel Structure for Automatic sliding door | NIHVA TECHNOLOGIES PVT. LTD. | NIHVA TECHNOLOGIES PVT. LTD. PUNE<br>Tel : 020 66304033<br>Email:- info@nihva.com<br>Website:- www.nihva.com |
| | SIGN | DATE |
| DRAWN | Omkar | 18/12/17 |
| CHECK | Shekhar | 18/12/17 |
| REV. | | |
| APPROVAL | Shekhar | 18/12/17 |
| If any queries contact : design@nihva.com | CLIENT - Cochin International Airport Ltd. | |
| ALL DIMENSION ARE IN mm | PROJECT - | |
| | SITE - Cochin | |
| | DWG. NO. : NIHVA/17-18/0313 | Rev- 0 |
| | SCALE: NTS / WT: | SHEET: 04 OF 04 |