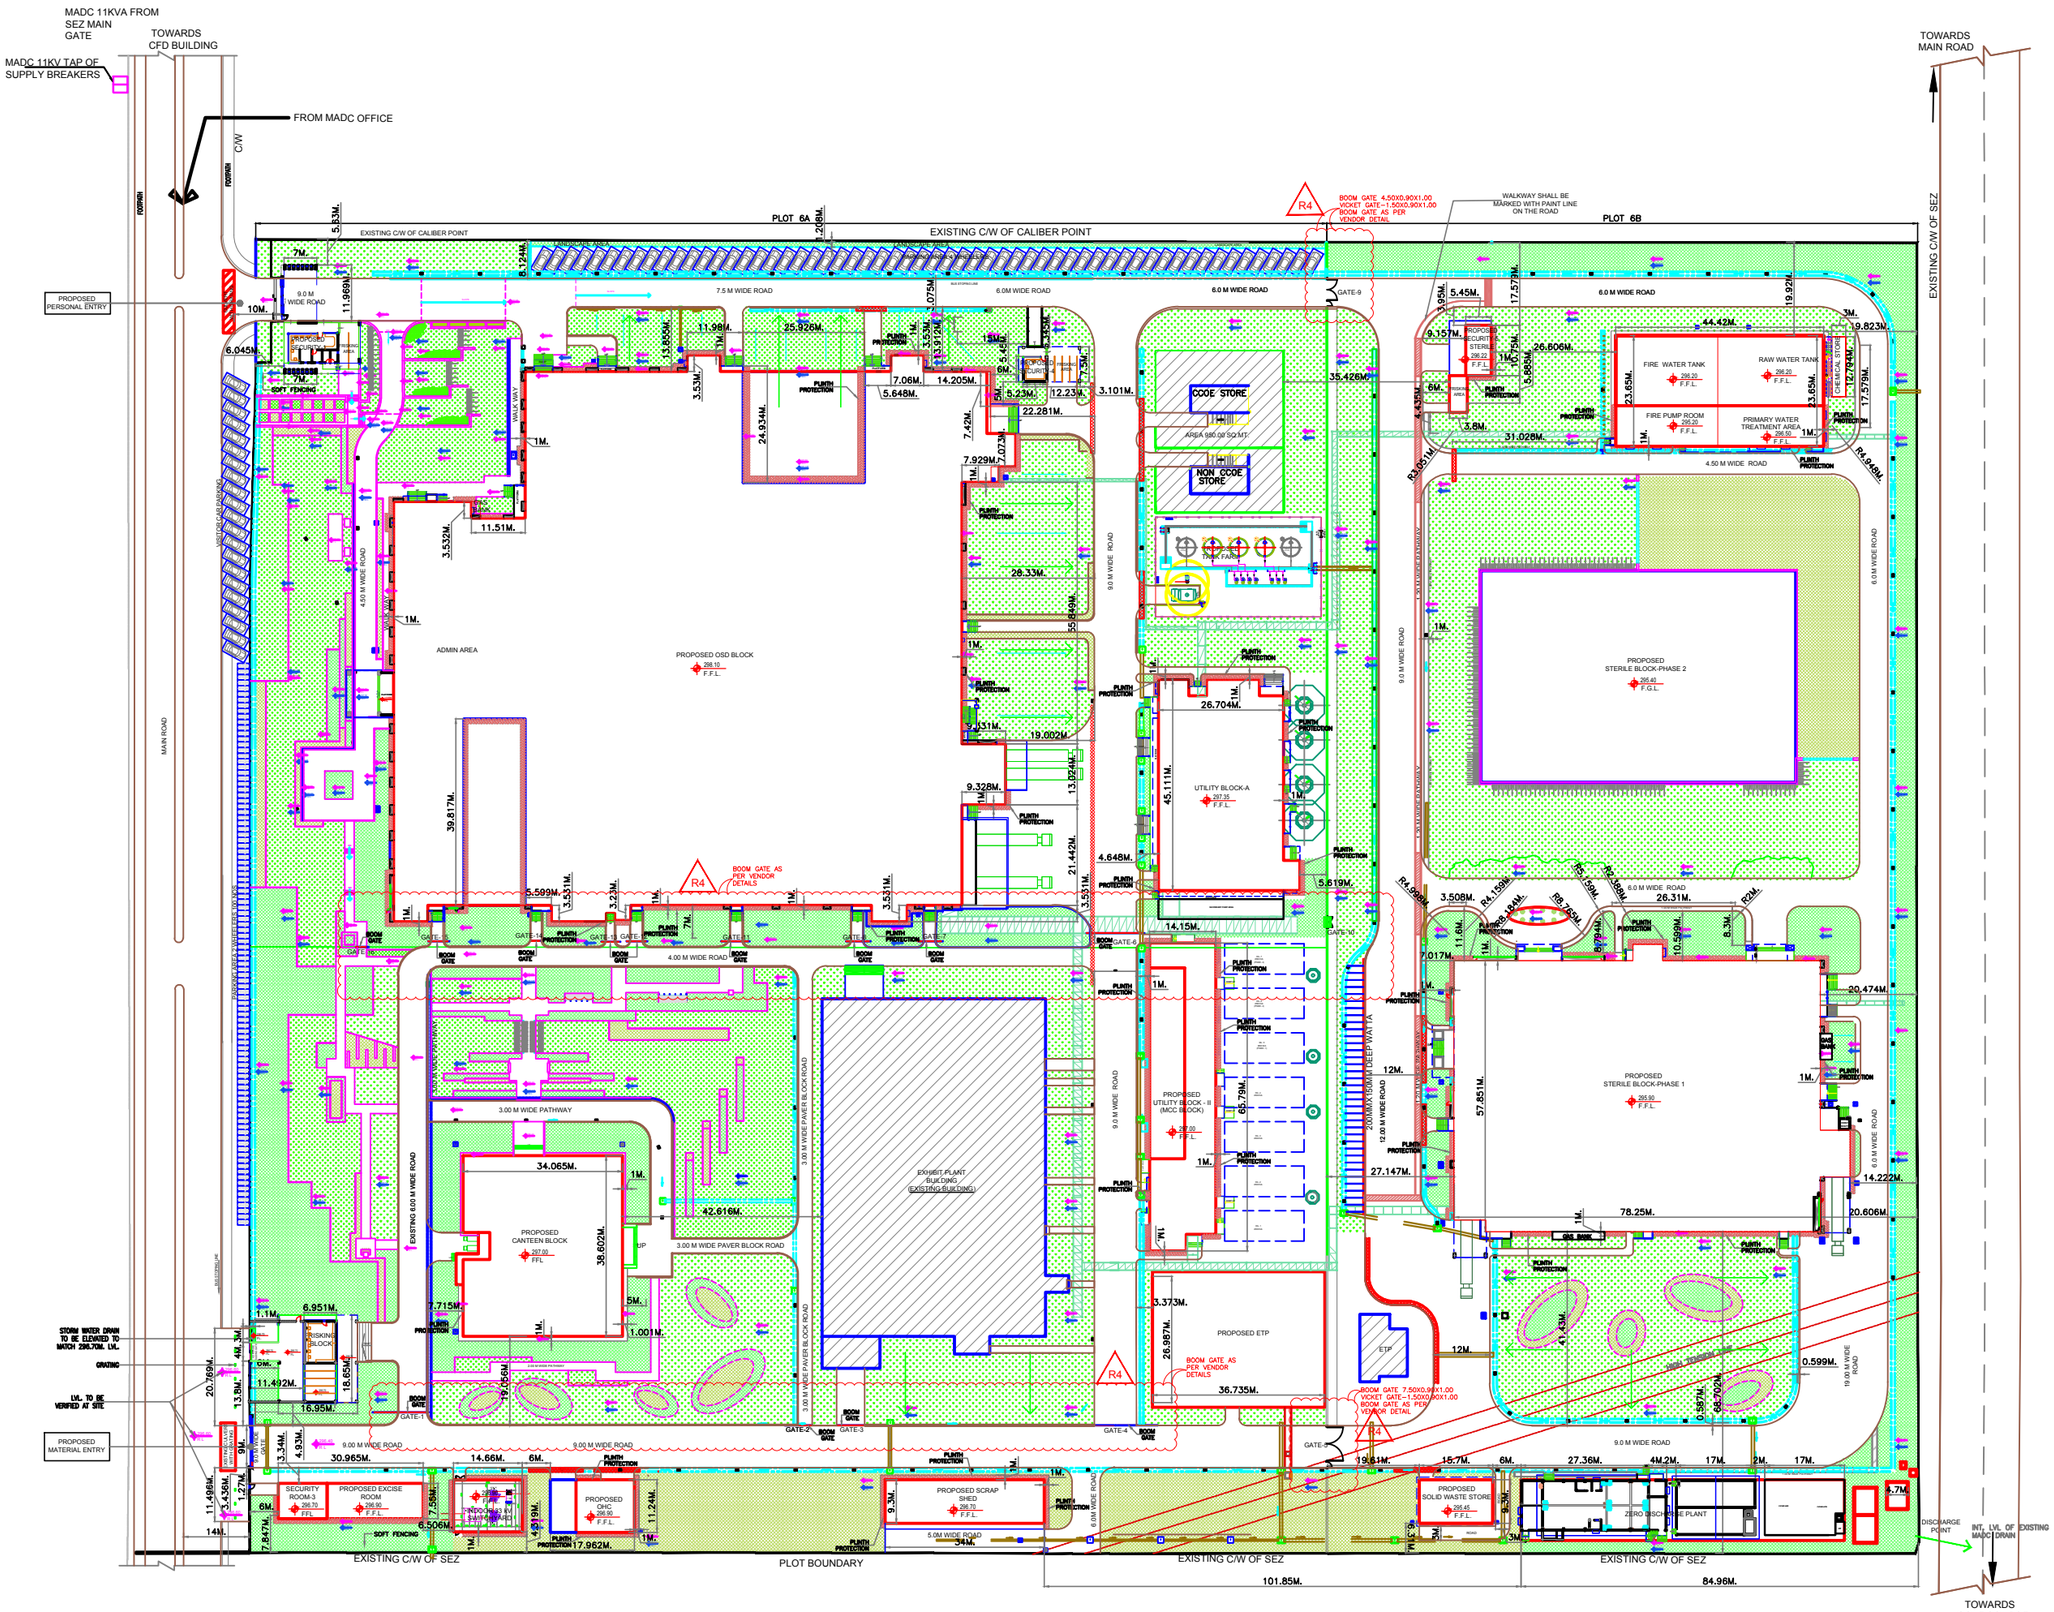


MASTER SITE PLAN WITH PHASE - I

ips INTERNATIONAL

Integrated Project Services
Engineering
Design
Site Supervision
Consulting

C-1,C-Block, Community Centre, Naraina Vihar
New Delhi - 110 028
+91-11-25777806 phone
+91-11-25779089 phone
+91-11-25779152 phone
www.ipsintl.net

REVISION	DATE	DESCRIPTION	BY
01	09FEB17	NEW DRAWING	PK
02	07SEP17	REVISED PER LANDSCAPE DWG.	SJ
03	25OCT17	REVISED AS PER SITE	PK
04	30OCT17	REVISED BOOM GATE AS PER CLINT	SJ

NOTES:

ALL DIMENSIONS ARE IN METERS UNLESS OTHERWISE SPECIFIED.

REFER SURVEY DRAWING NO 1415-01-APA-01-RC2a (SHARED BY LUPIN) IN ADDITION TO THIS LAYOUT PLAN

ALL COORDINATED MENTIONED FOR BUILDINGS ARE THE CENTERLINE OF THE COLUMNS.

OSD PLANT & STERILE BLOCK FFL TO BE CONSIDERED +/- 0.00M CORRESPONDS TO RL AS MENTIONED IN THE DRAWING.

COMMENT AND APPROVAL

BOOM GATE SCHEDULE

SIR.NO	GATE SIZE
1) GATE-1	6.00X0.90X1.00
2) GATE-2	3.00X0.90X1.00
3) GATE-3	6.00X0.90X1.00
4) GATE-4	9.00X0.90X1.00
5) GATE-5	7.50X0.90X1.00 1.50X0.90X1.00
6) GATE-6	9.00X0.90X1.00
7) GATE-7	2.50X0.90X1.00
8) GATE-8	2.50X0.90X1.00
9) GATE-9	4.50X0.90X1.00 1.50X0.90X1.00
10) GATE-10	2.50X0.90X1.00
11) GATE-11	2.50X0.90X1.00
12) GATE-12	2.50X0.90X1.00
13) GATE-13	1.80X0.90X1.00
14) GATE-14	2.50X0.90X1.00
15) GATE-15	2.50X0.90X1.00
16) GATE-16	2.00X0.90X1.00

PARKING AREA -
1) 4 WHEELERS CAR = 60 NOS
2) 2 WHEELERS = 100 NOS
3) CYCLE PARKING = 60 NOS.

KEY PLAN

CONFIDENTIAL
THE INFORMATION CONTAINED HEREIN MAY NOT BE USED OR REPRODUCED IN ANY MANNER WITHOUT WRITTEN PERMISSION OF INTEGRATED PROJECT SERVICES.

CLIENT
LUPIN LIMITED
MIHAN NAGPUR
Lupin Ltd.

DRAWING TITLE
MASTER LAYOUT PLAN

ENGINEER	ARCHITECT	DESIGNER
	SK	
DRAWN BY	REVIEWED BY	SCALE
SJ/PK		1:500

IPS # 14-1095/96
XREF FILE(S)
DRAWING NUMBER IPS-14-1095/96-AR- A4
CADD FILE #
PAPER SIZE A1 R3