

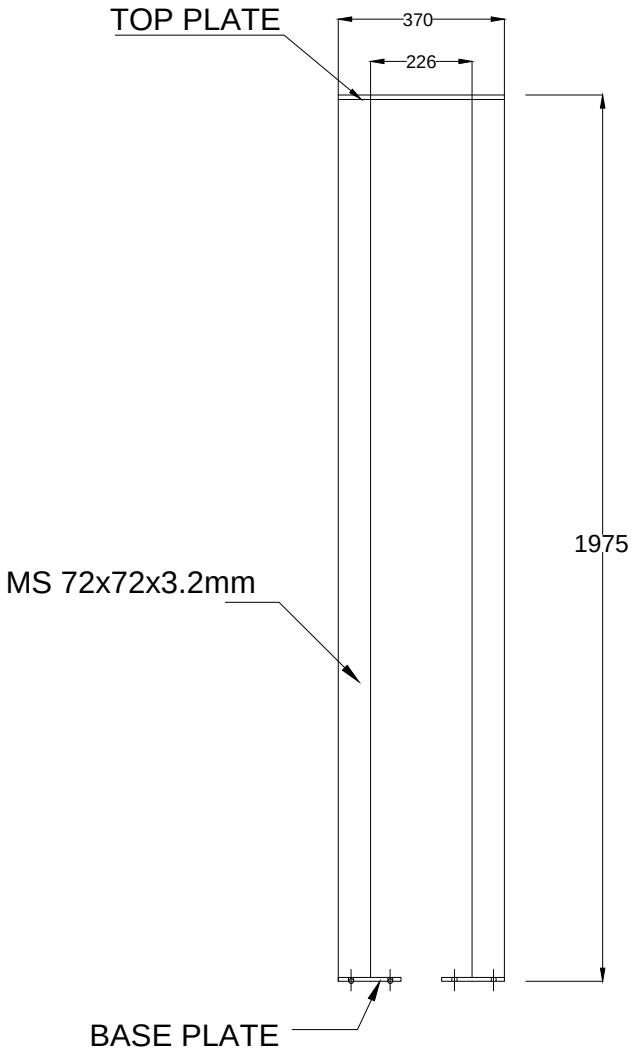


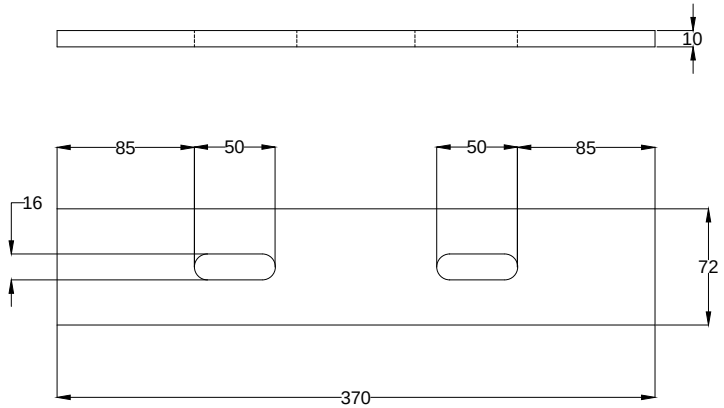


TOP PLATE

MATERIAL:-MS
THICKNESS:-10mm
QTY:- 09NOS

MATERIAL:-MS
QTY:- 09NOS

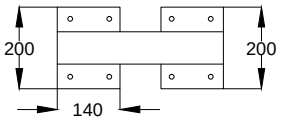

POST

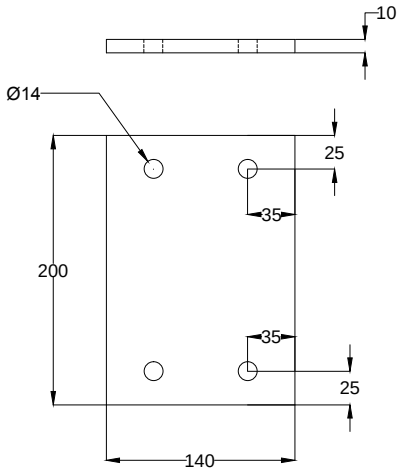

BASE PLATE

MATERIAL:-MS
THICKNESS:-10mm
QTY:- 18 NOS

NOTE:-ALL PLATE SHOULD BE LASER CUTTING

SR NO	TUBE SPECIFICATION		MATERIAL	SIZE
1	72X72X3.2mm MS TUBE	POST	MILD STEEL	1.955MTR- 18NOS
2	370X72X10mm MS PLATE	TOP PLATE	MILD STEEL	370X72X10mm- 09NOS
3	200X140X10mm MS PLATE	BOTTOM PLATE	MILD STEEL	140X200X10mm- 18NOS

This drawing & designing is the property of NIHVA TECHNOLOGIES. Not to be sold or copied to any other concern.

TITLE				
SLIDING GATE POST DRAWING				NIHVA TECHNOLOGIES PVT. LTD.
	Name	SIGN	DATE	Website:- www.nihva.com
DRAWN	SURAJ		23/11/18	CLIENT -
CHECK	PRADEEP		23/11/18	PROJECT -
APPROVAL	R.D		23/11/18	SITE LOCATION -CHAKAN
If any queries contact : design@nihva.com				DWG. NO. : NIHVA/18-19/VDR/235 REV.:- 0
ALL DIMENSION ARE IN mm				SCALE: NTS WT: SHEET: 01 OF 01

NIHVA TECHNOLOGIES PVT. LTD. PUNE
Tel : 020 66304033
Email:- info@nihva.com