
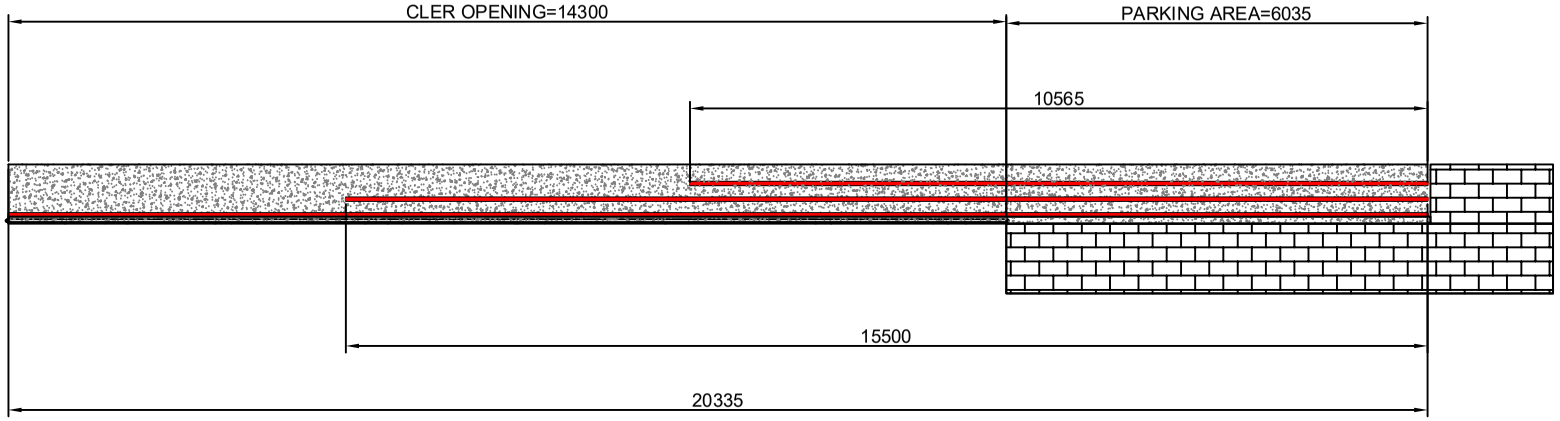


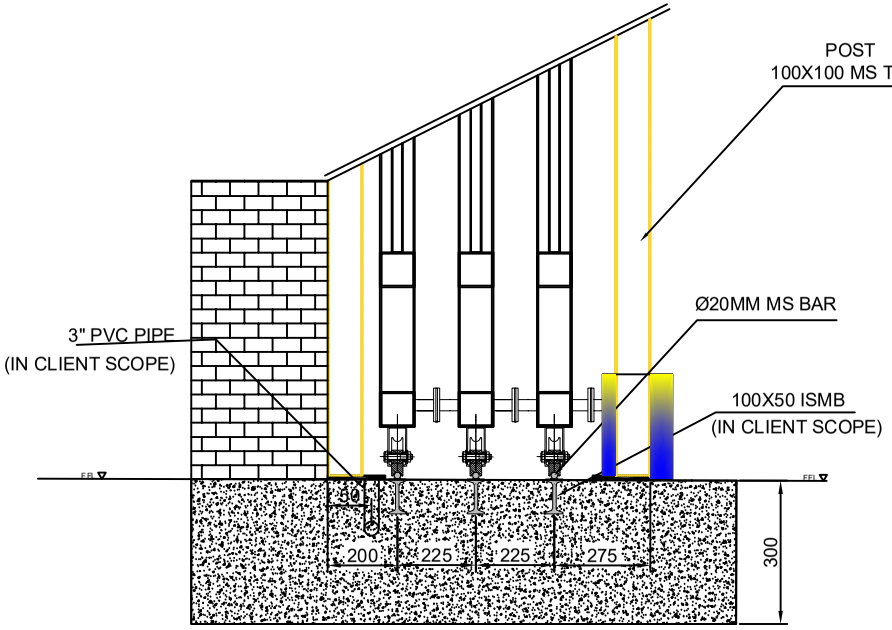

Note:-

1.All dimension are in mm.

2.All civil work is in client scope.

This drawing & design is the property of NIHVA TECHNOLOGIES. Not to be sold or copied to any other concern.

TITLE:- TEL.SLINDING GATE FOUNDATION DRAWING

NIHVA TECHNOLOGIES PVT. LTD.
NIHVA TECHNOLOGIES PVT. LTD. PUNE
Tel : 020 66304033
Email:- info@nihva.com
Website:- www.nihva.com

	NAME	DATE	SIGN
DRAWN	SUJATA.B	31/01/2022	
CHECK	G.PATIL	31/01/2022	
APPRD.	A.K	31/01/2022	

CLIENT - Fanidhar Mega Food Park Private Limited

LOCATION - GUJARAT

PRODUCT - TEL.SLIDING GATE

If any queries contact : design@nihva.com

DWG NO:-NIHVA/21-22/CLT/0307 REV- 1

ALL DIMENSION ARE IN mm

SCALE: NTS SCALE:-- 1:1 SHEET: 01 OF 01

Rev No.	Revision	Date	Revised By