

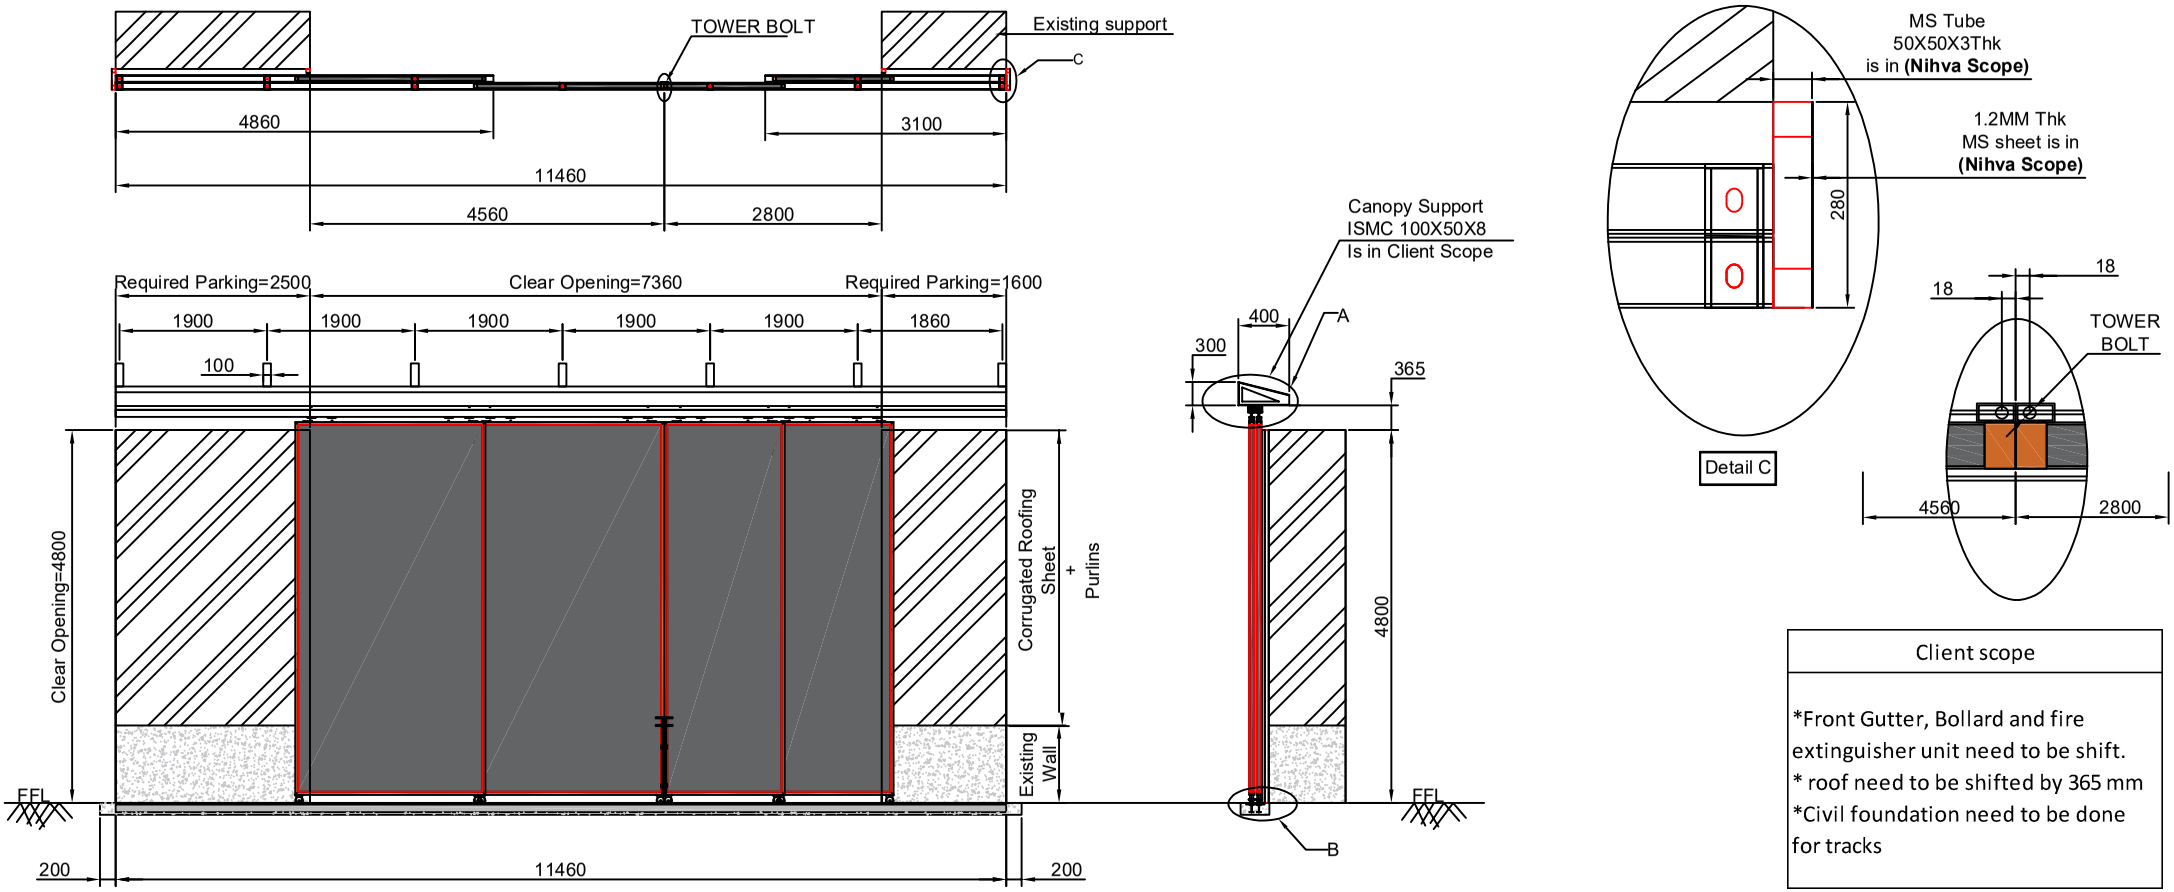


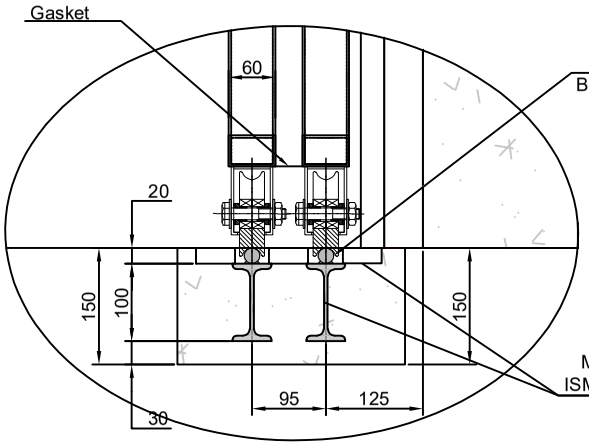

Detail A

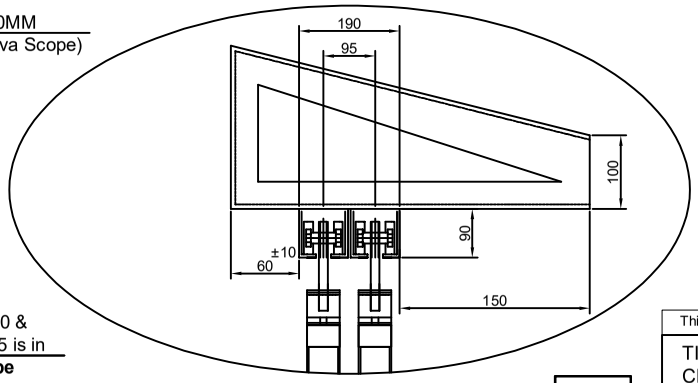

Detail B

Client scope
*Front Gutter, Bollard and fire extinguisher unit need to be shift. * roof need to be shifted by 365 mm *Civil foundation need to be done for tracks

Color code	Color
5018	Turquoise blue

Note:--

1. All dimension are in MM
2. All Civil work will be in client scope
3. Manufacturing,civil and installation tolerance will be ±10mm
4. Top and Bottom track should be in parallal within ±3mm
5. Nihva Supervisor on site for Monitoring/Checking of civil work

This drawing & design is the property of NIHVA TECHNOLOGIES. Not to be sold or copied to any other concern.

TITLE:-4LEAF-BOTH SIDE CRM DOOR-13

NIHVA TECHNOLOGIES PVT. LTD.
NIHVA TECHNOLOGIES PVT. PUNE
Tel : 020 66304033
Email:- info@nihva.com
Website:- www.nihva.com

	NAME	DATE	SIGN
DRAWN	SUJATA	13/05/2022	
CHECK	M.SUTAR	13/05/2022	
APPRD.	V.TARAK	13/05/2022	

CLIENT - LESTECH
LOCATION - POSCO MANGAON
PRODUCT - SLIDING DOOR
If any queries contact : design@nihva.com
DWG NO:-NIHVA/22-23/CLT/0037
REV- 0
ALL DIMENSION ARE IN mm
SCALE: NTS
SCALE:-- 1:1
SHEET: 01 OF 01

Rev No.	Revision	Date	Revised By