


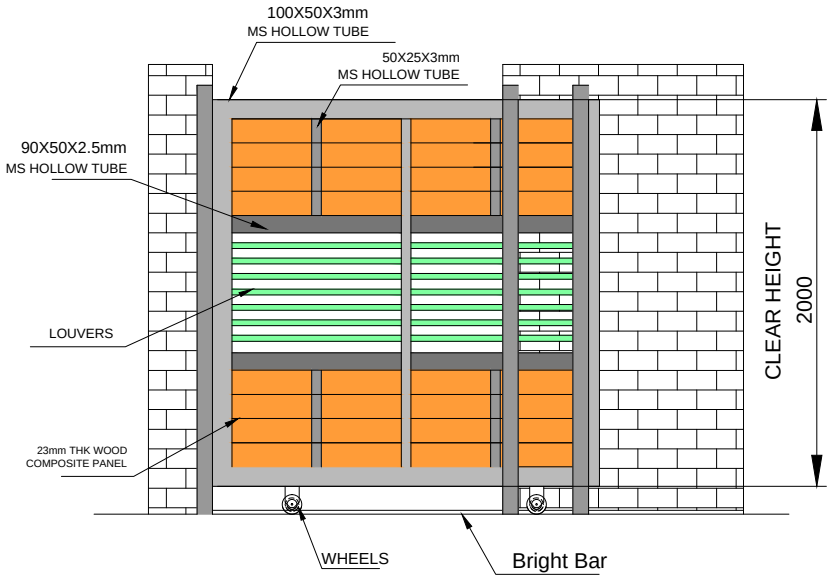


INSIDE ELEVATION

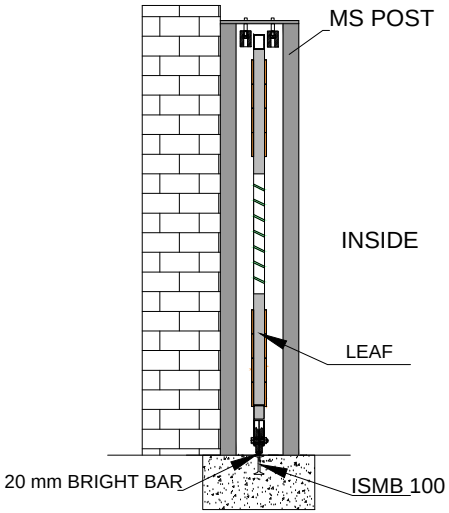


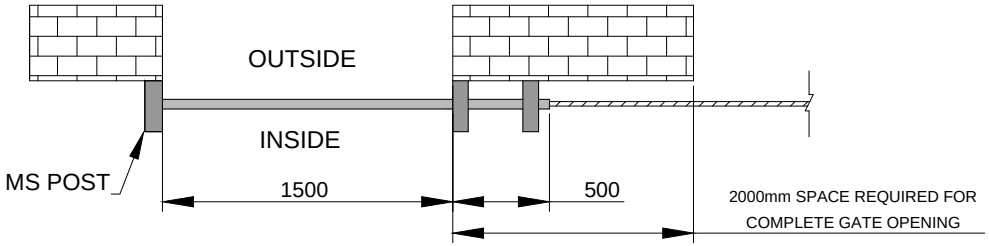

PLAN

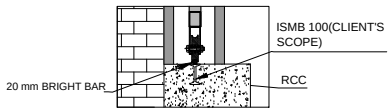

DETAIL VIEW OF A

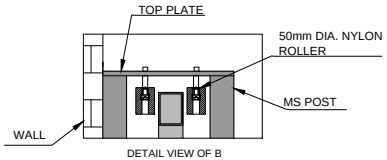

DETAIL VIEW OF B

TOLERANCE- ±10mm

SR NO	TUBE SPECIFICATION	
1	100X50X3mm	OUTER FRAME
2	50X25X2.5mm	INNER PATTERN
3	90X50X3mm	INNER PATTERN
4	100X50X3mm	INNER PATTERN
5	50X50X2mm	INNER PATTERN
6	100X50X3mm	FOR MS POST

CLEAR WIDTH	CLEAR HEIGHT	QUANTITY
1500mm	2000mm	1 NOS

DIMENSION :

CLEAR WIDTH	CLEAR HEIGHT	QUANTITY
1500mm	2000mm	1 NOS

MATERIAL:

THICKNESS :

NOTE-
1. ALL REQUIRED CIVIL WORK WILL BE IN CLIENTS SCOPE.
2. ONE COAT OF RED OXIDE SHADE WILL BE GIVEN TO THE GATE.

NIHVA TECHNOLOGIES PVT. LTD.
NIHVA TECHNOLOGIES PVT. LTD. PUNE
Email:- info@nihva.com
Website:- www.nihva.com

TITLE:

WICKET GATE

CLIENT'S APPROVAL :

CLIENT - INDO COOL COMPOSITES PVT. LTD

PROJECT - LANDTECH ENGINEERS PVT. LTD

SITE LOCATION -CHENNAI

DWG. NO. : NIHVA/17-18/0151

SCALE: NTS	WT:	SHEET:1 OF 1

DRAWN BY: SURAJ	DATE: 11-08-2017
CHECK BY : SAGAR P	DATE: 11-08-2017
APPROVED BY : S.S	DATE: 11-08-2017

If any queries contact : projects@nihva.com

NOTE: ALL DIMENSIONS ARE IN mm

THIS DRAWING & DESIGN IS THE PROPERTY OF NIHVA TECHNOLOGIES. NOT TO BE SOLD OR COPIED TO ANY OTHER CONCERN.