




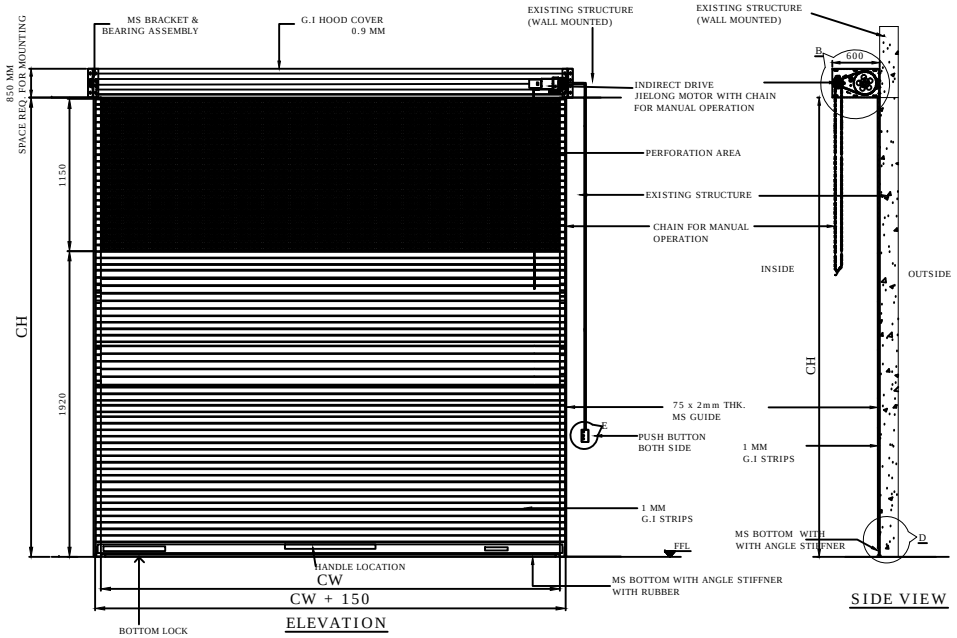


STRUCTURE

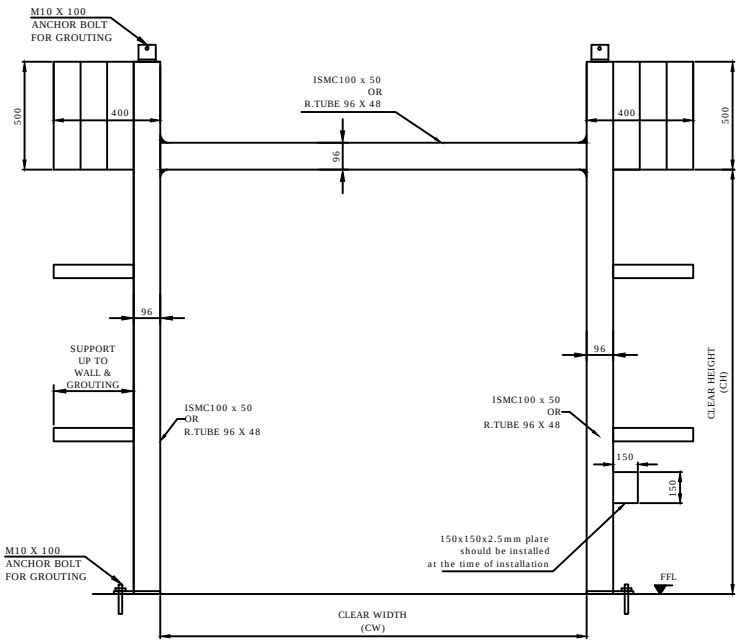


PLAN

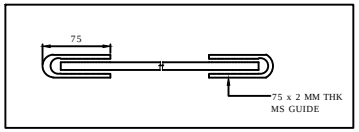


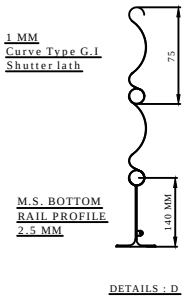

DETAILS : D

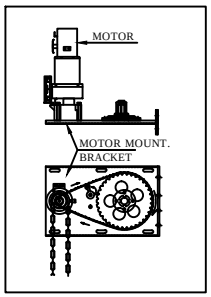

DETAILS : A & B

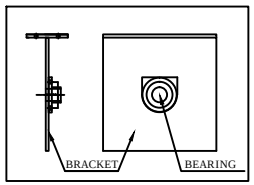

DETAILS : C

2280	3070	1	RAL -
CLEAR WIDTH (CW)	CLEAR HEIGHT (CH)	QUANTITY	RAL COLOR

(NOTE: REQUIRED TECHNICAL M.S STRUCTURE FOR SHUTTER SHOULD BE IN CLIENT SCOPE)

REV NO	DATE	DRAWN	REMARK
R02	01.09.20	P.A	1.CLEAR HEIGHT CHANGE
R01	08.08.20	P.A	2.STRUCTURE ADDED 1.CLEAR WIDTH CHANGE

This drawing & design is the property of NIHVA TECHNOLOGIES. Not to be sold or copied to any other concern.

TITLE: MOTORIZED ROLLING SHUTTER

NIHVA TECHNOLOGIES PVT. LTD.

NIHVA TECHNOLOGIES PVT. LTD. PUNE
Tel : 020 66304033
Email:- info@nihva.com
Website:- www.nihva.com

	NAME	SIGN	DATE
DRAWN	P.A		31.07.2020
CHECK	G.J		31.07.2020
APPRD.			

CLIENT - TECHEXPERT ENGINEERING PVT LTD.

PROJECT -

SITE LOCATION - PUNE

If any queries contact : design@nihva.com

DWG. NO. : NIHVA/20-21/0038/R02 REV- R02

ALL DIMENSION ARE IN mm

SCALE: NTS WT: SHEET: