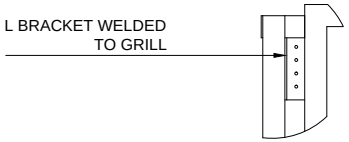

DETAIL A
SCALE 1 : 25

DETAIL B
SCALE 1 : 25

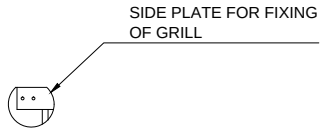

DETAIL D
SCALE 1 : 25

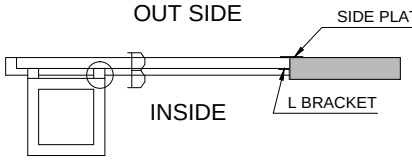

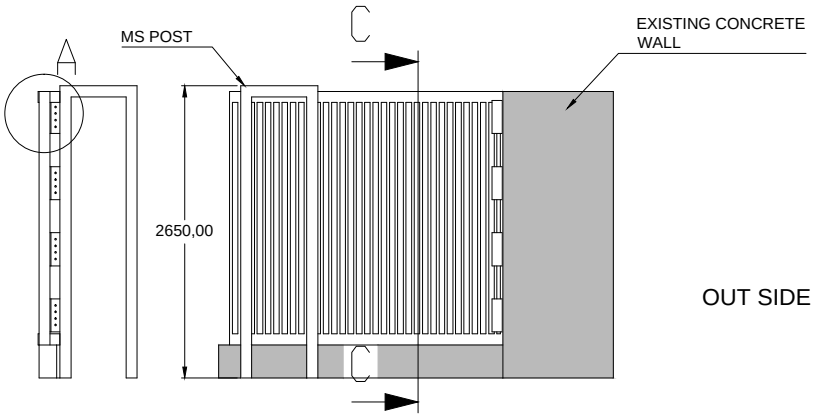

INSIDE VIEW

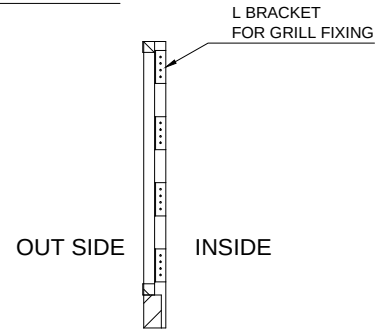

SECTION c-c

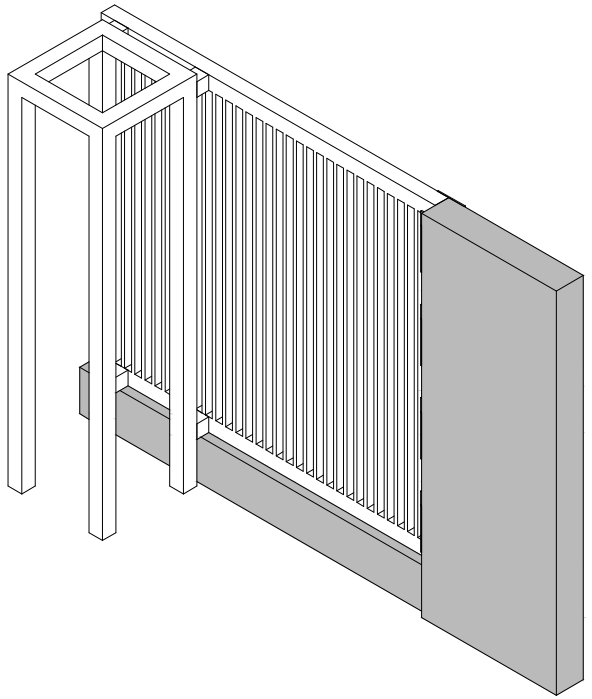

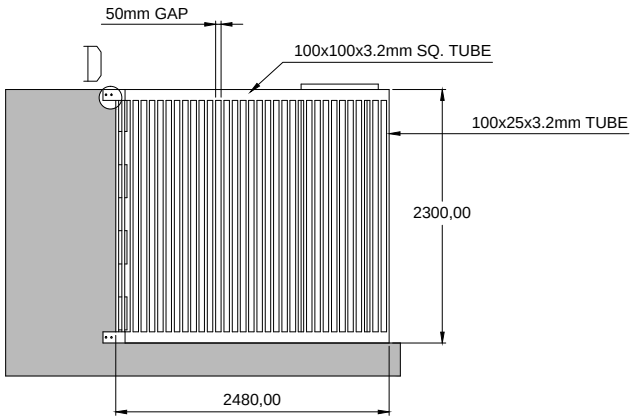

OUTSIDE VIEW

GRILL SIZE- 2480x2300 mm

This drawing & designing is the property of NIHVA TECHNOLOGIES. Not be sold or copy to any other concern.

TITLE: MS GRILL			NIHVA TECHNOLOGY PVT. LTD. PUNE Tel : 020 66304033 Email:- info@nihva.com Website:- www.nihva.com
	SIGN	DATE	
DRAWN	OMKAR	23/08/16	CLIENT - LUPIN LIMITED
CHECK	ANIL	23/08/16	PROJECT - LUPIN LIMITED
REV.	01		SITE - SUS ROAD
APPROVAL			DWG. NO. : NIHVA/16-17/0058
If any queries contact : projects@nihva.com			SCALE: 01 / WT: / SHEET: 01 OF 01
ALL DIMENSION ARE IN mm			