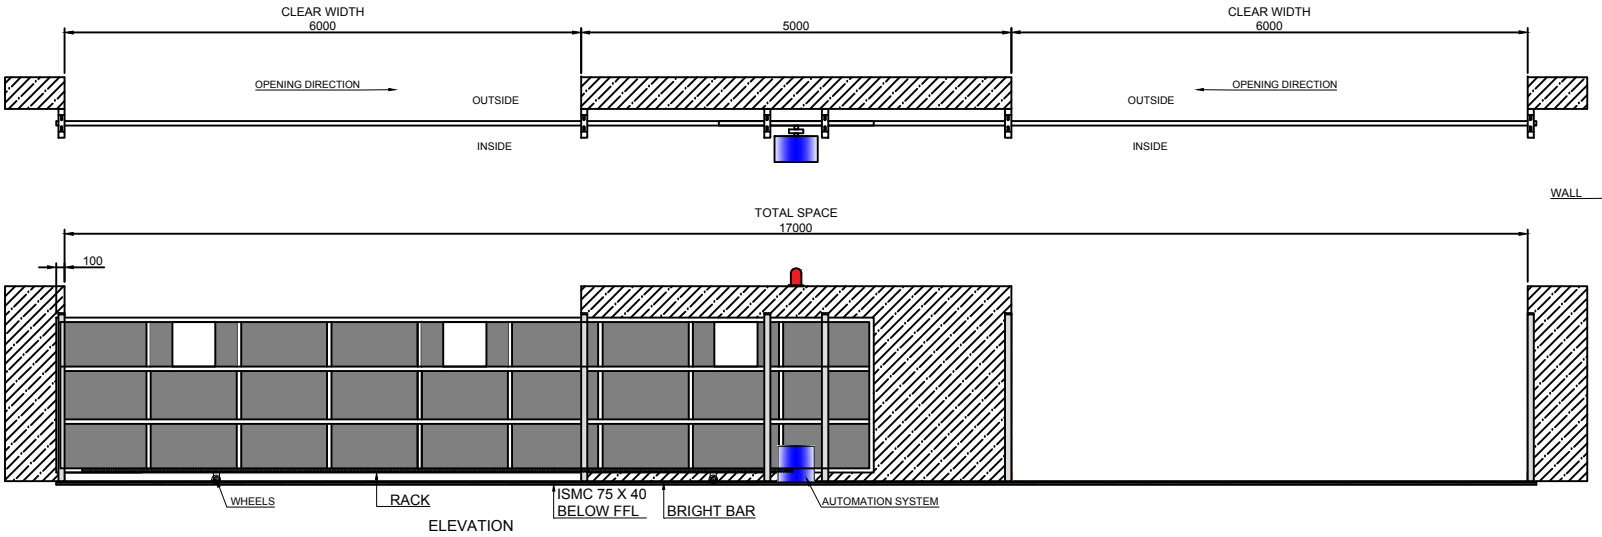
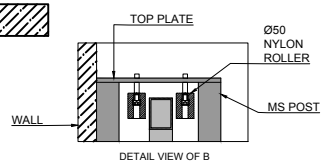
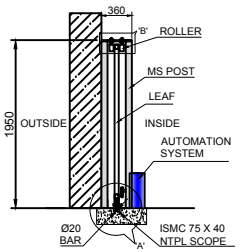
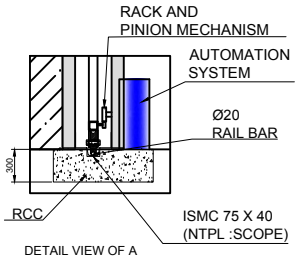



NOTE-
1. ALL REQUIRED CIVIL WORK WILL BE IN CLIENTS SCOPE.
2. TWO COATS OF PRIMER AND TWO COATS OF SYNTHETIC ENAMEL PAINT OF APPROVE SHADE.
3. SAFETY ACCESSORIES : FLASHING LIGHT, SAFETY PHOTOCELL, BUZZER, E.OFF PUSH BUTTON.
4. GATE LEAF WILL BE IN TWO PARTS FOR TRANSPORTATION & WILL BE WELD TOGETHER ON SITE.

TOLERANCE- ±10mm

This drawing & design is the property of NIHVA TECHNOLOGIES. Not to be sold or copied to any other concern.

| | | | |
|---|---|---|---|
| TITLE: AUTOMATIC SLIDING GATE | NIHVA TECHNOLOGIES PVT. LTD. | | |
| | NAME | SIGN | DATE |
| DRAWN | P.A | | 06.04.2020 |
| CHECK | G.J | | 06.04.2020 |
| APPRD. | | | |
| CLIENT - CLOOS INDIA WELDING TECHNOLOGY PVT LTD | | | |
| PROJECT - | | | |
| SITE LOCATION - BHOSARI, PUNE | | | |
| If any queries contact : design@nihva.com | DWG. NO. : NIHVA/20-21/0001 | | REV- R00 |
| ALL DIMENSION ARE IN mm | SCALE: NTS | WT: | SHEET: |

NIHVA TECHNOLOGIES PVT. LTD. PUNE
Tel : 020 66304033
Email:- info@nihva.com
Website:- www.nihva.com