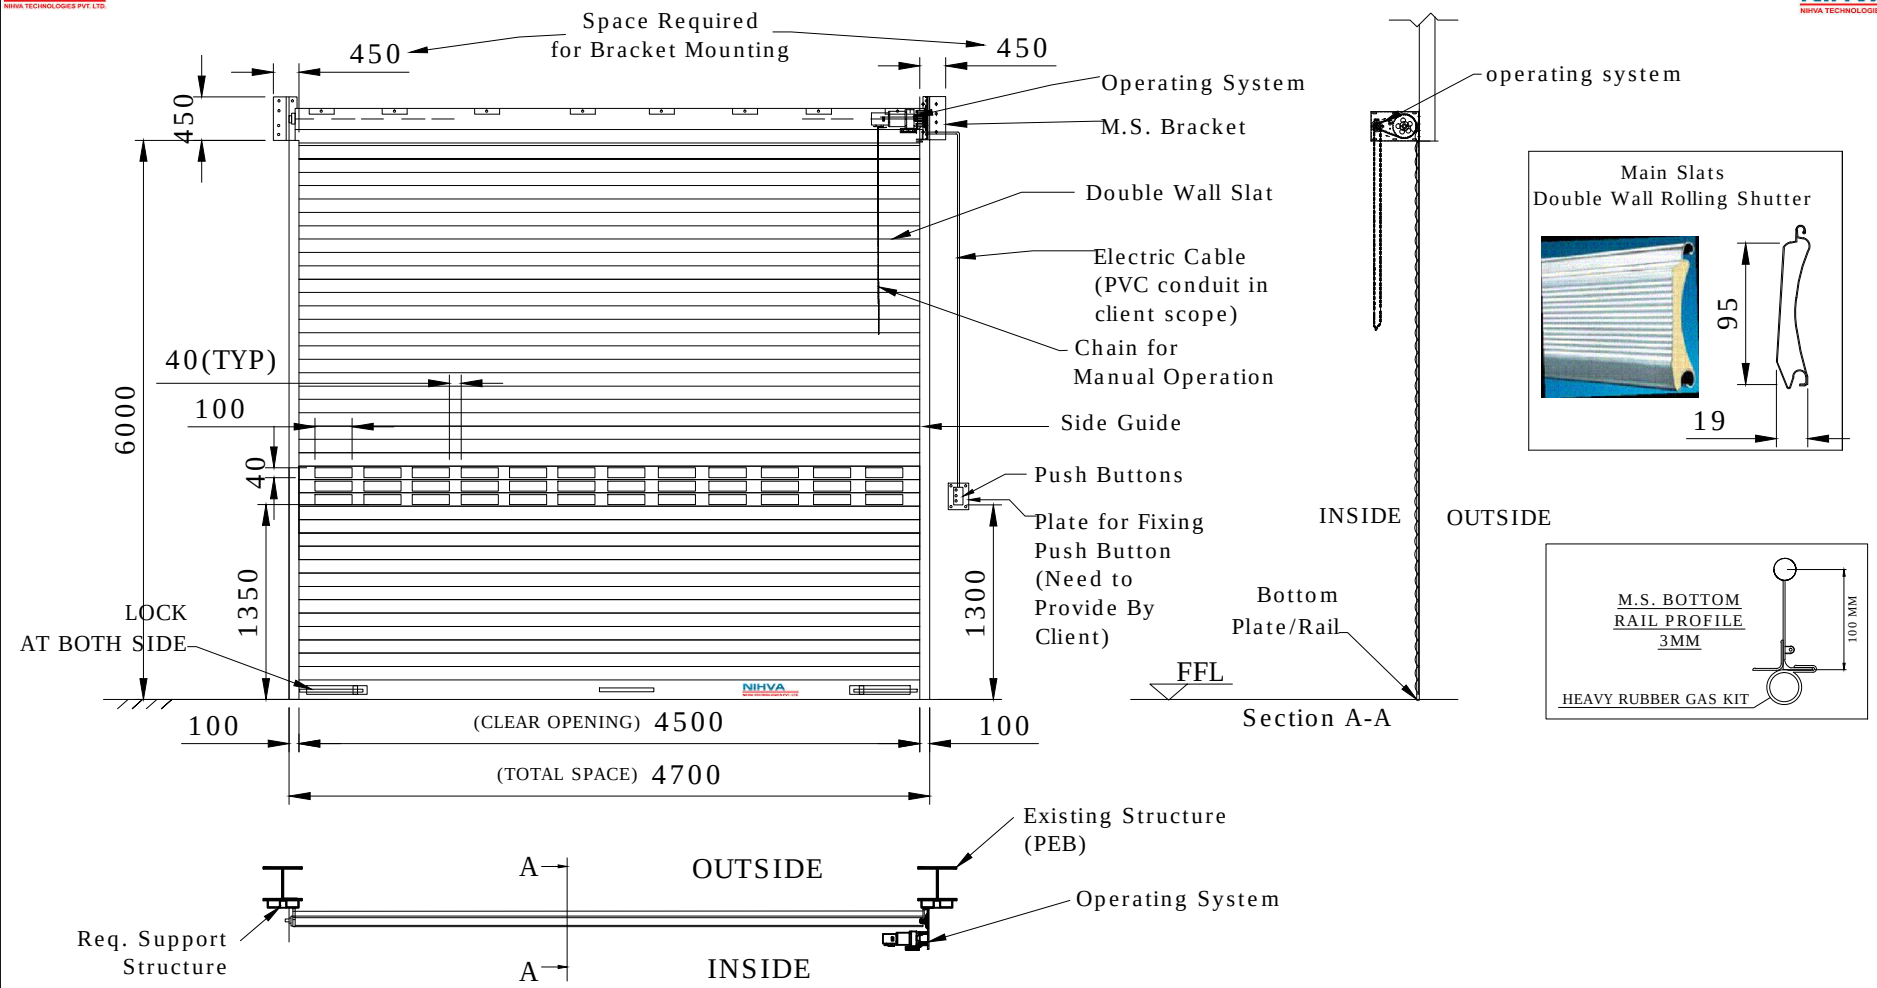


NOTE: push button fixing will be decided as per site ready condition.

QTY.:- 1 NOS.

Sr. No.	Details	Specification
1)	Slats Profile	95mm x 19mm with PU filled inside
2)	Guide Channel	100mm x 40mm
3)	Shaft	125mm OD with heavy duty flanges and hardware
4)	Bottom Rail	125mm x3mm thick with extra angle support. Locking arrangement provides
5)	Brackets	450mmx450mmx3mm thickness

as per standard:
EN12424 -wind resistant-100km/hr
EN13241-Thermal Insulation U=3.9w/m2k
EN717-1- Acoustic Insulation=R=19dB

CLEAR OPENING SIZE :- 4500mm x 6000mm	COLOUR: Off White