

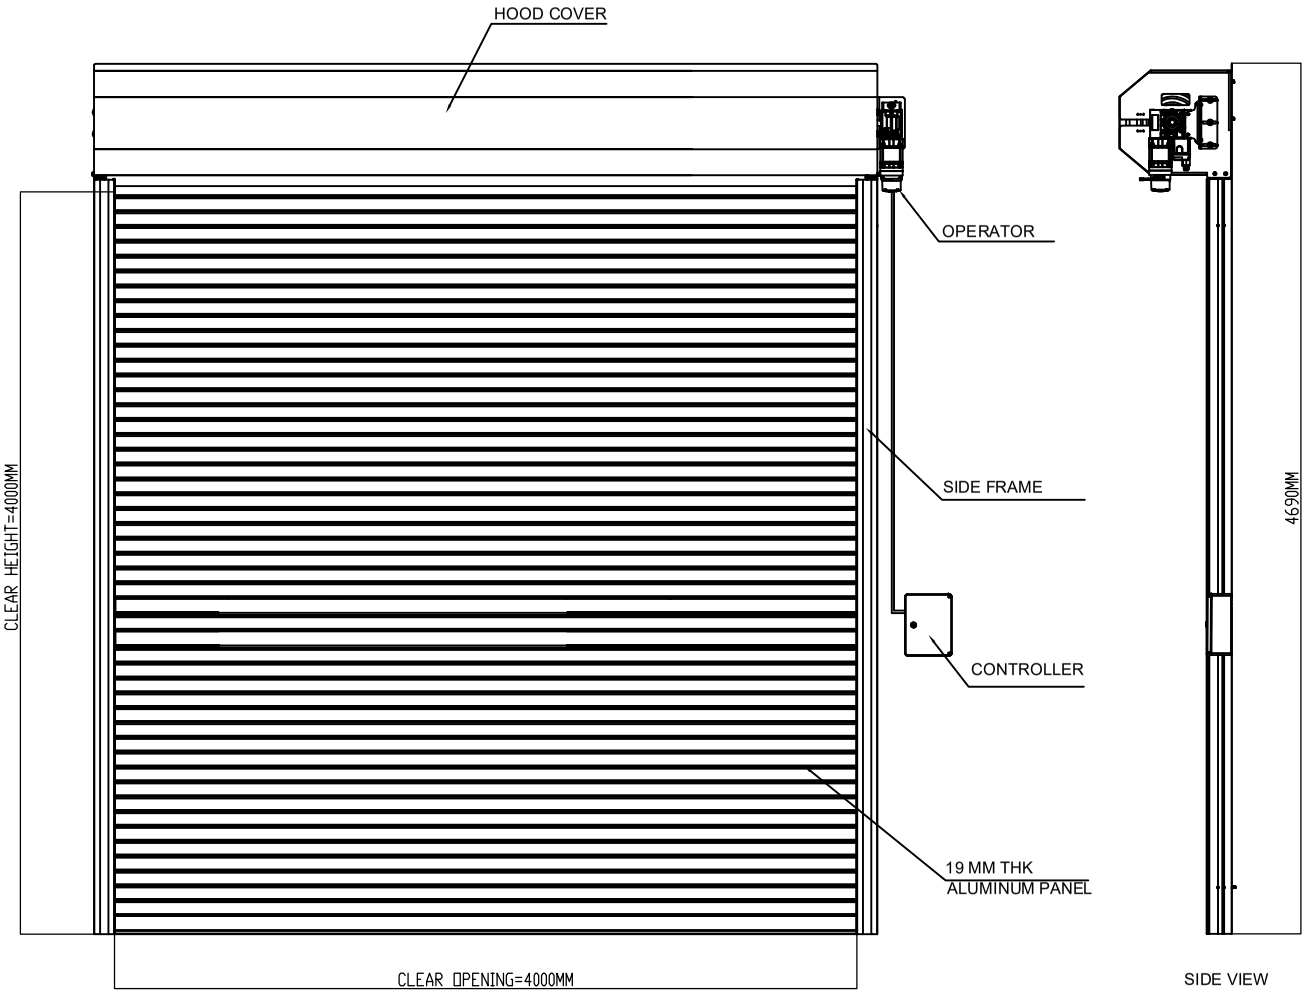


ELEVATION

SIDE VIEW

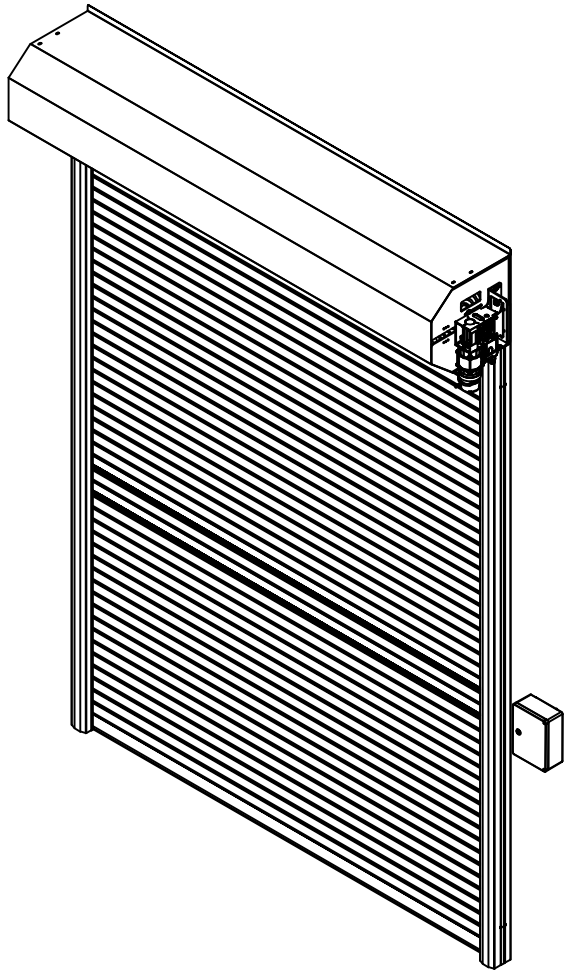

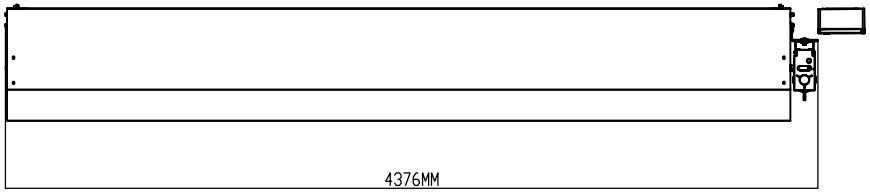

TOP VIEW

NOTES:
1. COLOR : RAL 9006 aluminium lamella
2. SAFETY DEVICE : PHOTOCELL
3. EMERGENCY OPENING : CRANK HANDLE
4. PLEASE CONFIRM THE MOUNTING OF DOOR WILL BE ON WALL OR STRUCTURE.

DOOR QTY : 1 NO

This drawing & design is the property of NIHVA TECHNOLOGIES. Not to be sold or copied to any other concern.

TITLE:-
DOUBLE WALL ALUMINUM HIGH SPEED DOOR

NIHVA TECHNOLOGIES PVT. LTD.
NIHVA TECHNOLOGIES PVT. LTD. PUNE
Tel : 020 66304033
Email:- info@nihva.com
Website:- www.nihva.com

	NAME	SIGN	DATE
DRAWN	S.B		03/12/2021
CHECK	G.P.		03/12/2021
APPRD.	A.K.		03/12/2021

CLIENT -MA ENGINEERING
PROJECT - JOHN DEERE
SITE LOCATION - PUNE

If any queries contact : design@nihva.com | DWG. NO. : NIHVA/21-22/CLT/0272 | REV- 0

ALL DIMENSION ARE IN mm | SCALE: NTS | WT: | SHEET: 01 OF 01