



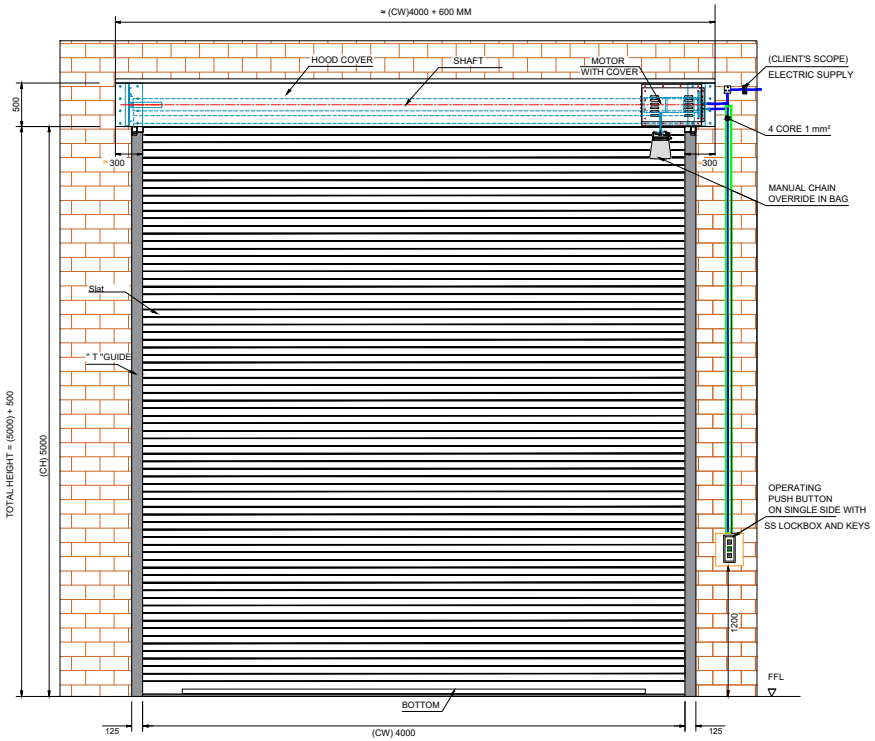

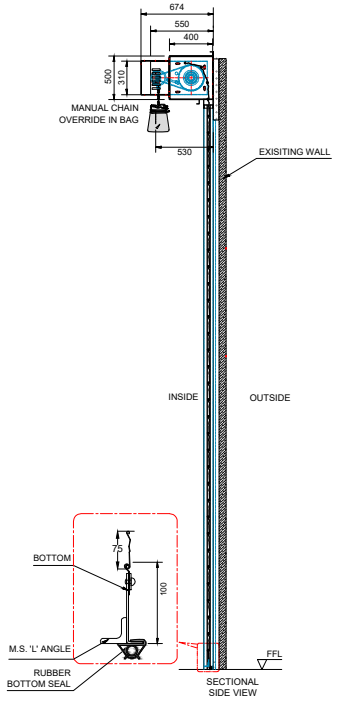

TECHNICAL SPECIFICATION:-

SR.	SPECIFICATION	DETAILS
1.	Description & Drive	Motorised Rolling Shutter (Indirect Drive)sprocket Chain arrangement.
2.	Location Area	Inside/Out side
3.	Mounting Surface	Side Brackets: Optional+On concrete/Steel&Side
4.	Slat	Curved 75 mm GI Sheet - 1.2 mm Thk
5.	Bottom Profile	MS Plate 100 x 2.5 mm thick with Angle Stiffener
6.	Guide Profile	M.S." T " Shape profile 65 mm -150 x 3.0 mm Thick.
7.	Hood Cover & Motor Cover	Made of GI Sheet Thickness 0.9 mm
8.	Colour	Synthetic Enamel Paint
9.	Push Botton	3 Way Push Baton on Single Side

SHUTTER SIZES :-

SR.	CLEAR WIDTH	CLEAR HEIGHT	QTY.
01	4000 mm	5000 mm	01

Note :-

1. All Dimension are in mm

This drawing & designing is the property of NIHVA TECHNOLOGIES. Not to be sold or copied to any other concern.

TITLE :- MOTORISED ROLLING SHUTTER			NIHVA TECHNOLOGIES PVT. LTD. PUNE Tel : 020 66304033 Email:- info@nihva.com Website:- www.nihva.com
	NAME	DATE	CLIENT - GS PEB & CIVIL WORK PVT. LTD.
DRAWN	B.S.	16/07/2025	PROJECT - MOTORISED ROLLING SHUTTER
CHECK & APPROVAL	V.T.	16/07/2025	FORMAT NO - NIHVA-DD-F-03
			DWG. NO. : NIHVA/24-25/GB/2411001 REV-00
			SCALE: NTS WT: SHEET: 01 OF 01
ALL DIMENSION ARE IN mm			If any queries contact : design@nihva.com