



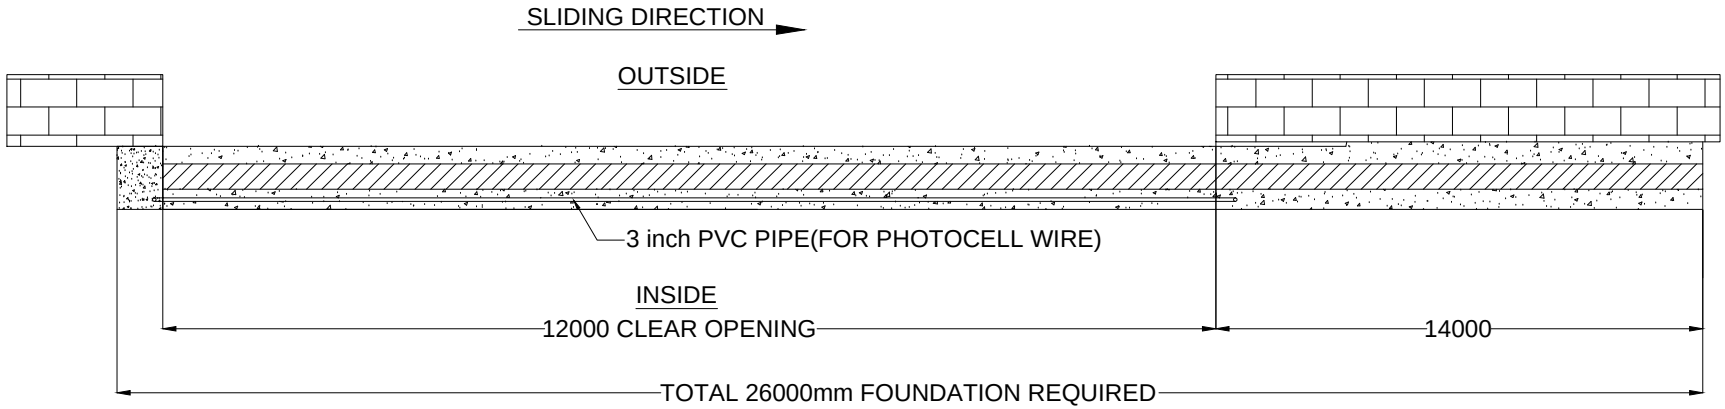

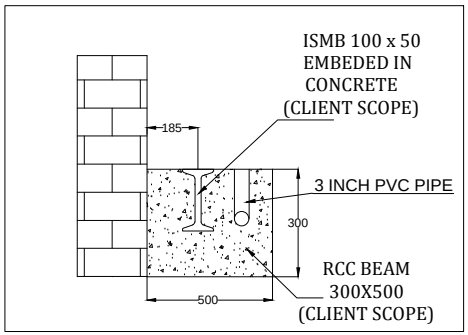

This drawing & designing is the property of NIHVA TECHNOLOGIES. Not to be sold or copied to any other concern.

TITLE: SLIDING GATE FOUNDATION DRAWING			NIHVA TECHNOLOGIES PVT. LTD. PUNE Tel : 020 66304033 Email:- info@nihva.com Website:- www.nihva.com
	Name	SIGN	DATE
DRAWN	SURAJ		10/10/18
CHECK	PRADEEP		10/10/18
APPROVAL	R.D		10/10/18
If any queries contact : design@nihva.com			DWG. NO. : NIHVA/18-19/0143 REV.:- 0
ALL DIMENSION ARE IN mm			SCALE: NTS WT: SHEET: 01 OF 01
			CLIENT - INOX
			PROJECT -
			SITE LOCATION -CHENNAI