



SR.NO	DESCRIPTION	QTY
1	ERW PIPE OD33 X 3490L	2 NOS
2	ERW PIPE OD33 X 3430L	2 NOS
3	ERW PIPE OD33 X 900L	4 NOS
4	ERW PIPE OD33 X 420L	8 NOS
5	ELBOW BEND OD33 X 150L	4 NOS
6	FLAT 50 X 16 X 100L	4 NOS
7	FLAT 50 X 10 X 100L	4 NOS
8	FLAT 50 X 16 X 75L	4 NOS
9	FLAT 50 X 10 X 75L	4 NOS
10	M10 X 25L WITH SPRING WASHER	12 NOS

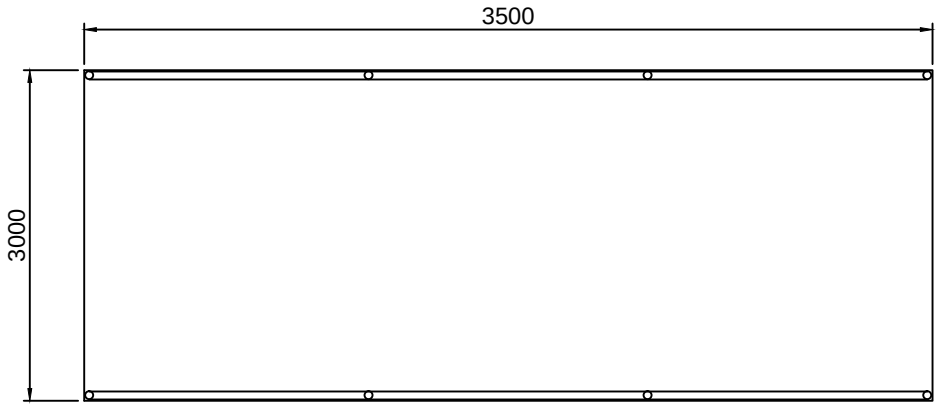

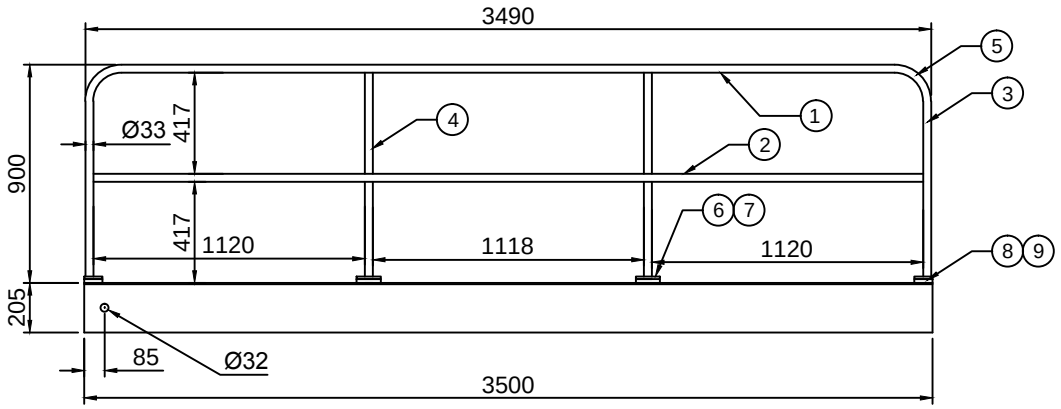

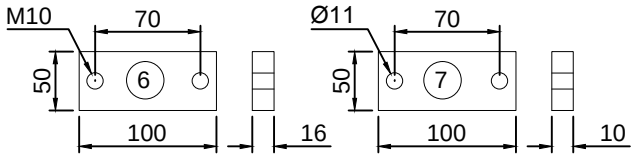

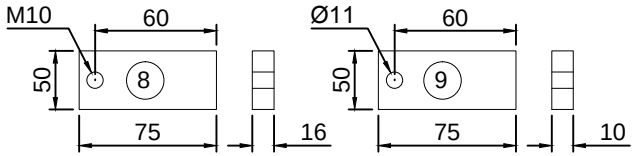

This drawing & design is the property of NIHVA TECHNOLOGIES. Not to be sold or copied to any other concern.

TITLE : -

SAFETY RAILING

NIHVA TECHNOLOGIES PVT. LTD.

NIHVA TECHNOLOGIES PVT. LTD. PUNE
Tel : 020 66304033
Email:- info@nihva.com
Website:- www.nihva.com

	SIGN	DATE
DRAWN	P.A	03.05.2019
CHECK		
REV.		
APPROVAL		

CLIENT -

PROJECT -

SITE -

DWG. NO. : NIHVA/19-20/VDR/012

If any queries contact : projects@nihva.com

SCALE: NTS | WT: | SHEET: 01 OF 01

ALL DIMENSION ARE IN mm