



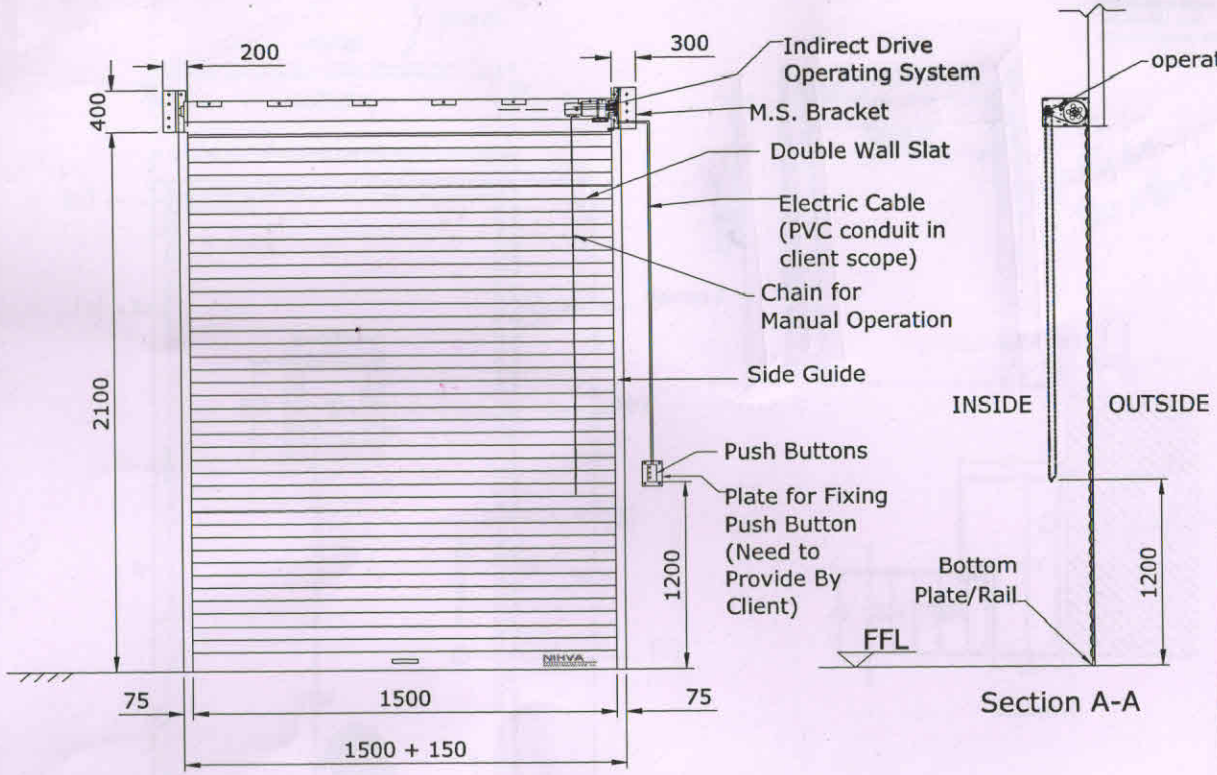


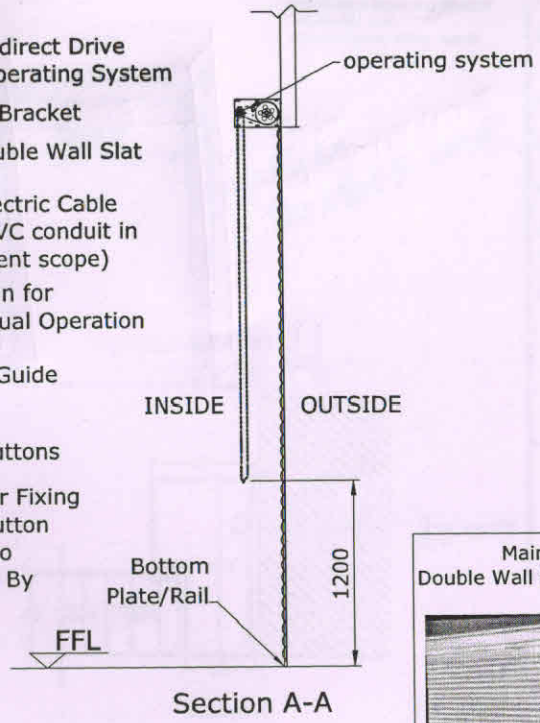

Section A-A

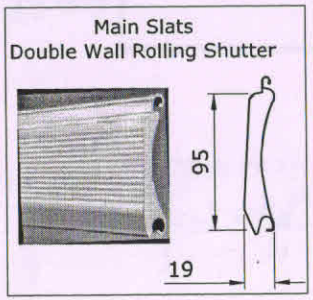

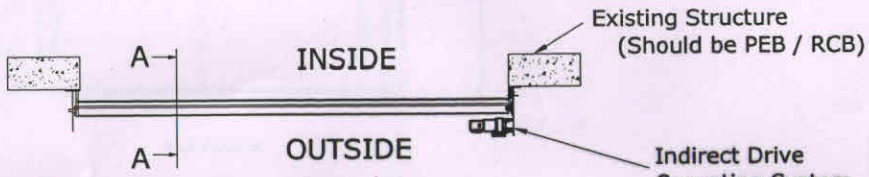

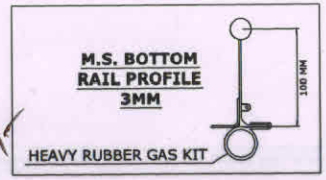

GK 15/9/17

CLEAR WIDTH (CW)	CLEAR HEIGHT (CH)	QUANTITY
1500mm	2100mm	1 NOS

DIMENSION :

CLEAR WIDTH	CLEAR HEIGHT	QUANTITY
1500mm	2100mm	1 NOS

MATERIAL :

THICKNESS :

NIHVA TECHNOLOGIES PVT. LTD.

NIHVA TECHNOLOGY PVT. LTD. PUNE
Email:- info@nihva.com
Website:- www.nihva.com

TITLE:

DOUBLE WALL ROLLING SHUTTER

CLIENT'S APPROVAL :

CLIENT -Ashok Constructions

PROJECT -Ferrero India Pvt. Ltd.

SITE LOCATION -Baramati.

DWG. NO. : NIHVA/16-17/0200

SCALE: NTS	WT:	SHEET:1 OF 1

DRAWN BY: SURAJ	DATE: 12-09-2017
CHECK : OMKAR	DATE: 12-09-2017
APPROVED BY : SHEKHAR	DATE: 12-09-2017

If any queries contact : projects@nihva.com

NOTE: ALL DIMENSION ARE IN mm

THIS DRAWING & DESIGNING IS THE PROPERTY OF NIHVA TECHNOLOGIES. NOT BE SOLD OR COPY TO ANY OTHER CONCERN.

Ashok Constructions Pune