

Abbrevation's:
WOW-Wall Opening Width
WOH-Wall Opening Height
UC-Under Cut
FFL-Finished Floor Level

## ASSESORIES DETALES


(a) HINGES:
(b) PANIC BAR:
(c) DOOR CLOSER: 2 NOS.
(d) GLASS:Clear fire Vision Glass Clear 6mm of size 300x300mm.

Shutter thickness : 47 mm
Frame Sheet thick : 1.20mm
Shutter sheet thick : 0.80mm
Fixing : On Soliid Brick plasterd wall with Anchors

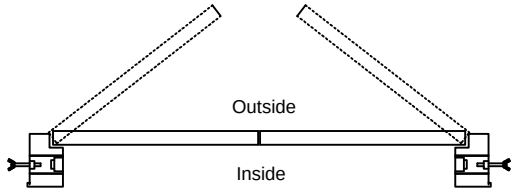

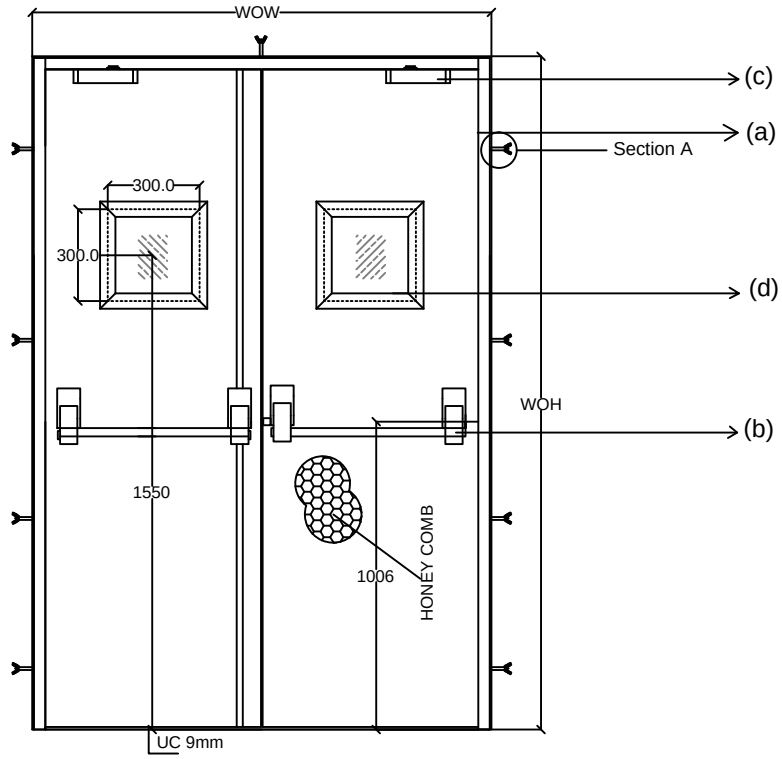


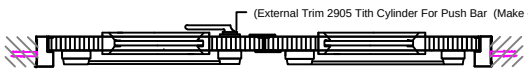

Inside Elevation




Top View

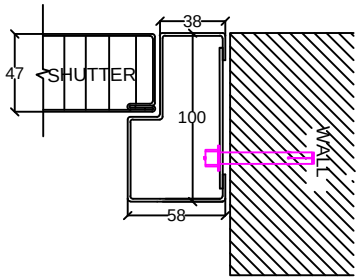NOTE:- *All Dimensions are in mm.
*Tolerance:-All Linear Dimensions ±3mm,Others ±0.5mm.
*The Drawing Is For Location of Hardware only. Drawing Does Not Represent The Hardware For More Clarity, Please Go Through Hardware Broucher.




Detail view of Section A

NOTE-
1. CLIENT SHOULD SELECT DOOR TYPE FROM ATTACHED DOOR HANDLING SHEET & COLOR OF DOOR.
2. THIRD PARTY FIRE RATED CERTIFICATE.

FIRE DOOR SIZES

| WOW | WOH | QUANTITY | LOCATION |
|---|---|---|---|
| 2000 | 2100 | 1 | |

This drawing & designing is the property of NIHVA TECHNOLOGIES. Not to be sold or copied to any other concern.

TITLE: STEEL DOOR

NIHVA TECHNOLOGIES PVT. LTD.

NIHVA TECHNOLOGIES PVT. LTD. PUNE
Tel : 020 66304033
Email:- info@nihva.com
Website:- www.nihva.com

| | NAME | SIGN | DATE |
|---|---|---|---|
| DRAWN | A.K. | | 21.01.2019 |
| CHECK | P.A. | | 21.01.2019 |
| APPROVAL | R.D. | | 21.01.2019 |
| MFG. | | | |

If any queries contact : projects@nihva.com

ALL DIMENSION ARE IN mm

CLIENT- ESR PUNE
PROJECT - BMW
SITE -. CHAKAN , PUNE
DWG. NO. : NIHVA/18-19/0245 REV. : 00
SCALE: NTS WT: SHEET: 01 OF 01