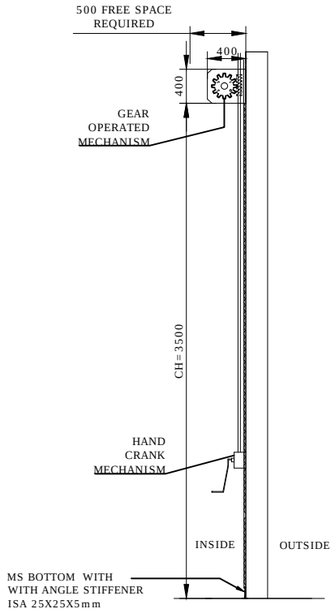
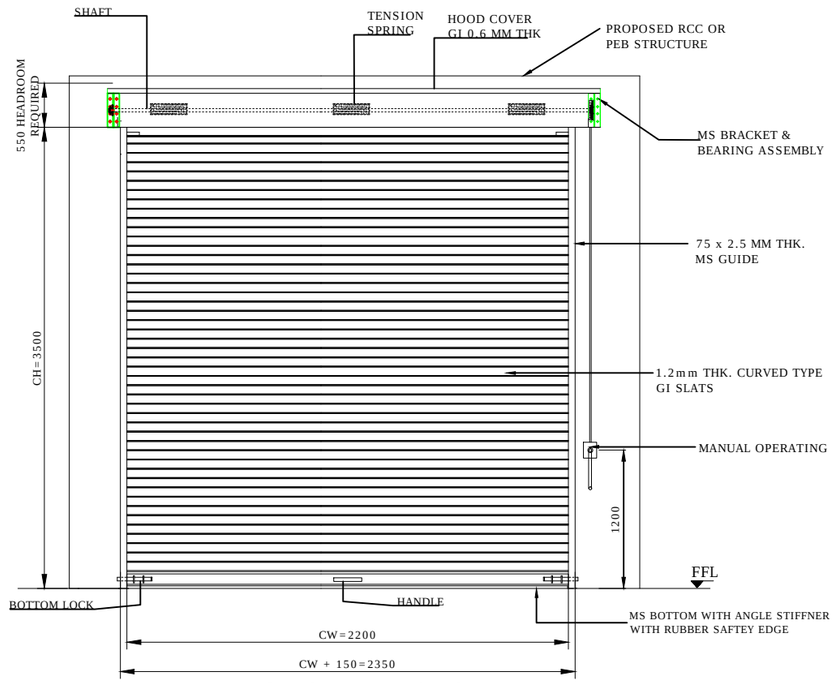
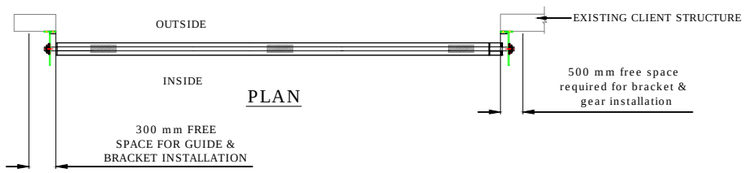


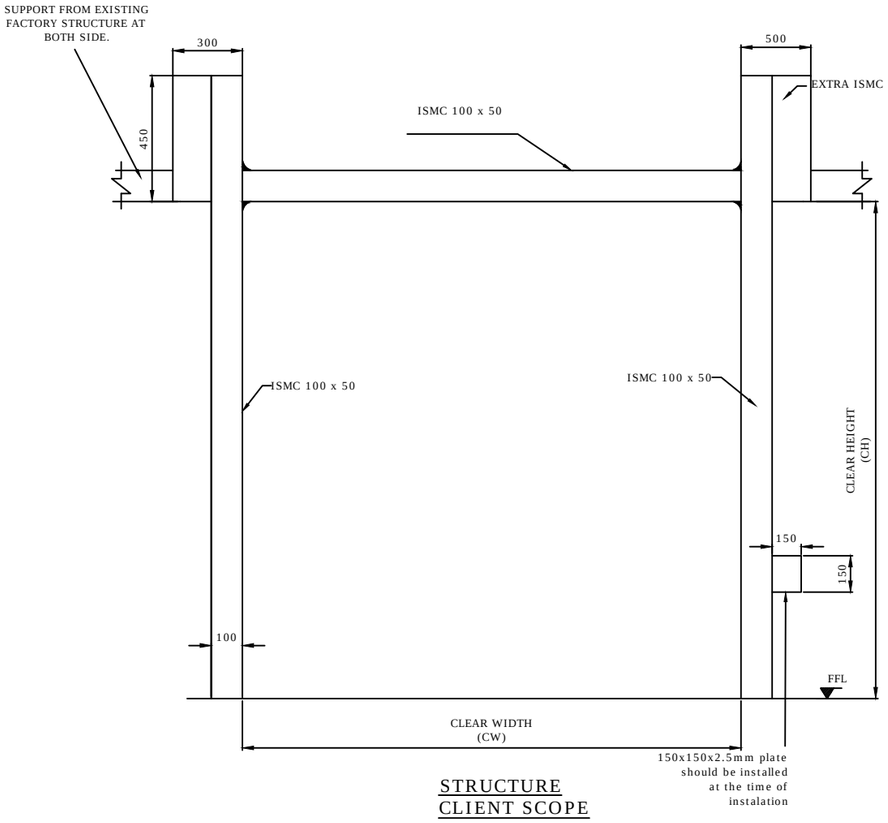

SIDE VIEW



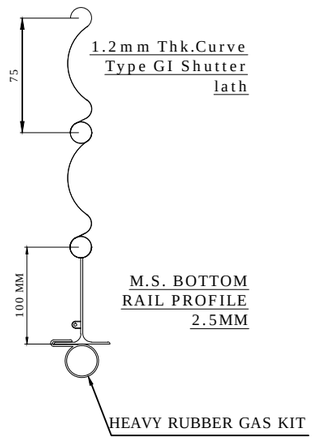

OUTSIDE ELEVATION



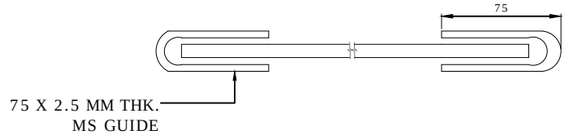

PLAN




STRUCTURE CLIENT SCOPE




M.S. BOTTOM RAIL PROFILE 2.5MM




| RAL CODE | RAL COLOR | APPROVED |
|---|---|---|
| RAL 9010 | PURE WHITE | |
| RAL 9002 | GREY WHITE | |
| RAL 7035 | LIGHT GREY | |
| RAL 5002 | ULT. M. BLUE | |

NOTE-
1. ALL CIVIL WORK WILL BE CLIENT'S SCOPE.
2. IF STRUCTURE REQUIRED FOR SHUTTER IS IN CLIENT'S SCOPE.
3. SURFACE FINISH: POWDER COATING OF APPROVED RAL CODE.
4. MOUNTING ON CONCRETE/ STEEL STRUCTURE.
5. PLEASE CONFIRM THE MOUNTING OF LEVER EITHER ON LEFT OR RIGHT SIDE.

| SR NO | ( CW ) CLEAR WIDTH | ( CH ) CLEAR HEIGHT | QUANTITY |
|---|---|---|---|
| 1 | 2200 | 3500 | 03 NO |

TOLERANCE - ±10mm

This drawing & design is the property of NIHVA TECHNOLOGIES. Not to be sold or copied to any other concern.

TITLE
GEAR OPERATED ROLLING SHUTTER

| | NAME | SIGN | DATE |
|---|---|---|---|
| DRAWN | G.I.P | | 15.02.2022 |
| CHECK | A.K. | | 15.02.2022 |
| APPRD. | V.T. | | 15.02.2022 |

If any queries contact : design@nihva.com

ALL DIMENSION ARE IN mm

NIHVA TECHNOLOGIES PVT. LTD.
Website:- www.nihva.com
NIHVA TECHNOLOGIES PVT. LTD. PUNE
Tel : 020 66304033
Email:- info@nihva.com

CLIENT - QUALITY INFRASTRUCTURE PVT LTD
PROJECT -GEAR OPERATED ROLLING SHUTTER
SITE LOCATION -GUJARAT
DWG. NO. : NIHVA/21-22/CLT/348 | REV- R0
SCALE: NTS | WT: | SHEET: 01 OF 01