



PLAN

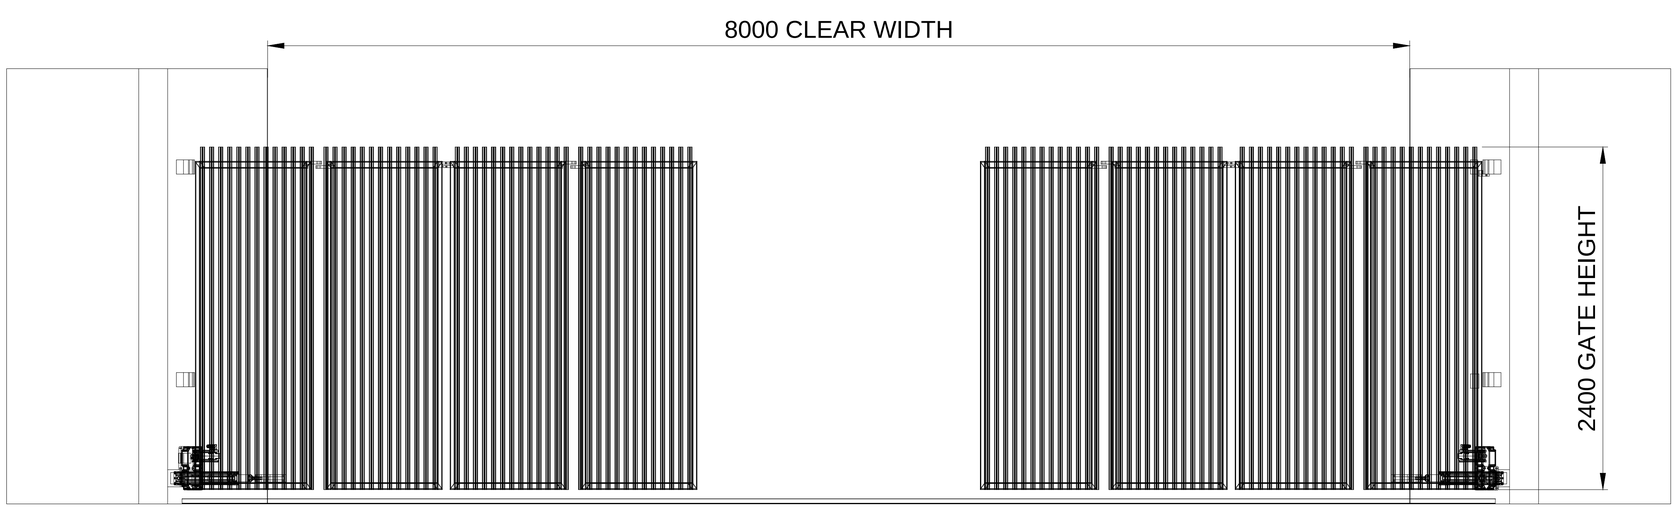

ELEVATION

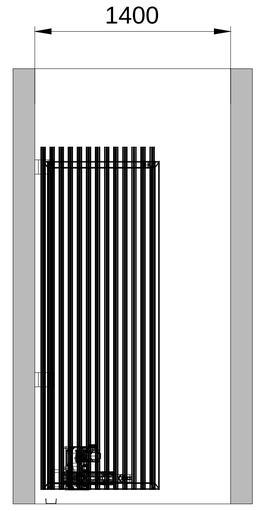

SECTION

GATE SIZE- 8000mmX2400mm
Leaf size- 1100mmX2400mm
No. of leafs- 8

TOLERANCE- ± 5mm

This drawing & design is the property of NIHVA TECHNOLOGIES. Not to be sold or copied to any other concern.

TITLE			
AUTOMATIC FOLDING GATE - INTERMEDIATE POSITION			NIHVA TECHNOLOGIES PVT. LTD. PUNE Tel : 020 66304033 Email:- info@nihva.com Website:- www.nihva.com
	SIGN	DATE	
DRAWN	S.S.	01/06/17	CLIENT - HAFEEZ CONTRACTOR
CHECK	M.D.	01/06/17	PROJECT - DAICAEC
REV.			SITE - BKC, MUMBAI
APPROVAL			DWG. NO. : NIHVA/17-18/0098
If any queries contact : projects@nihva.com			SCALE: NTS | WT: | SHEET: 01 OF 01
ALL DIMENSION ARE IN mm			