
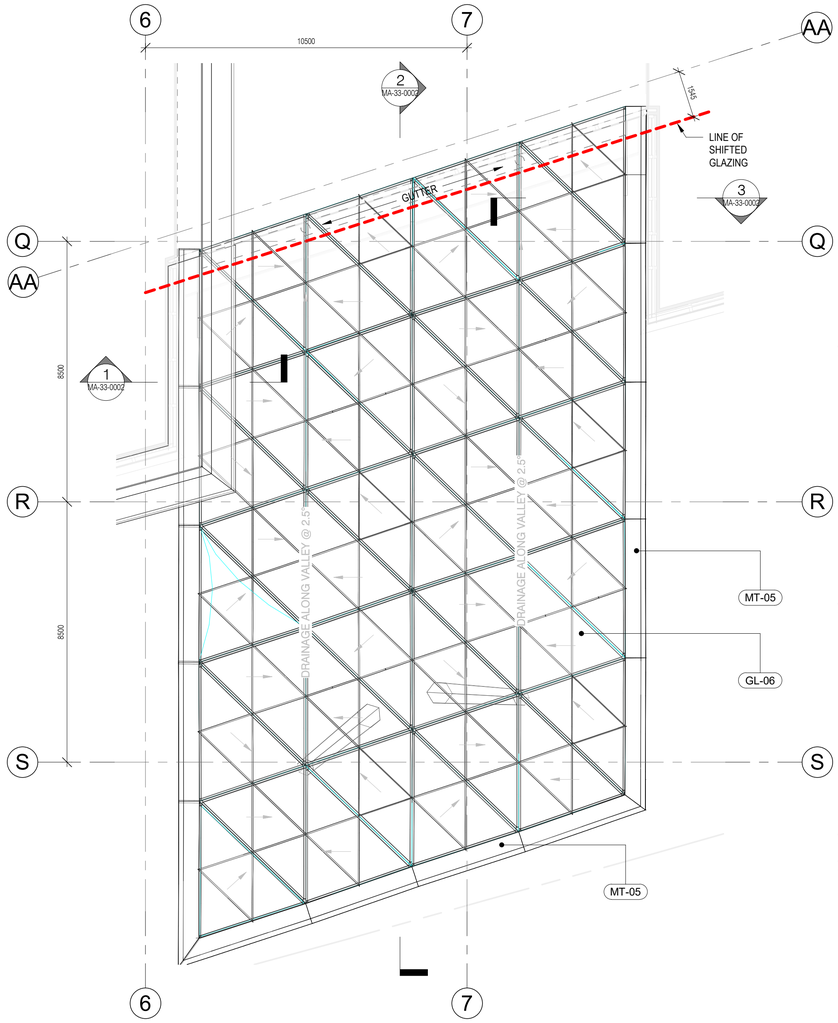



1 Entrance Canopy Plan

Scale: 1 : 100

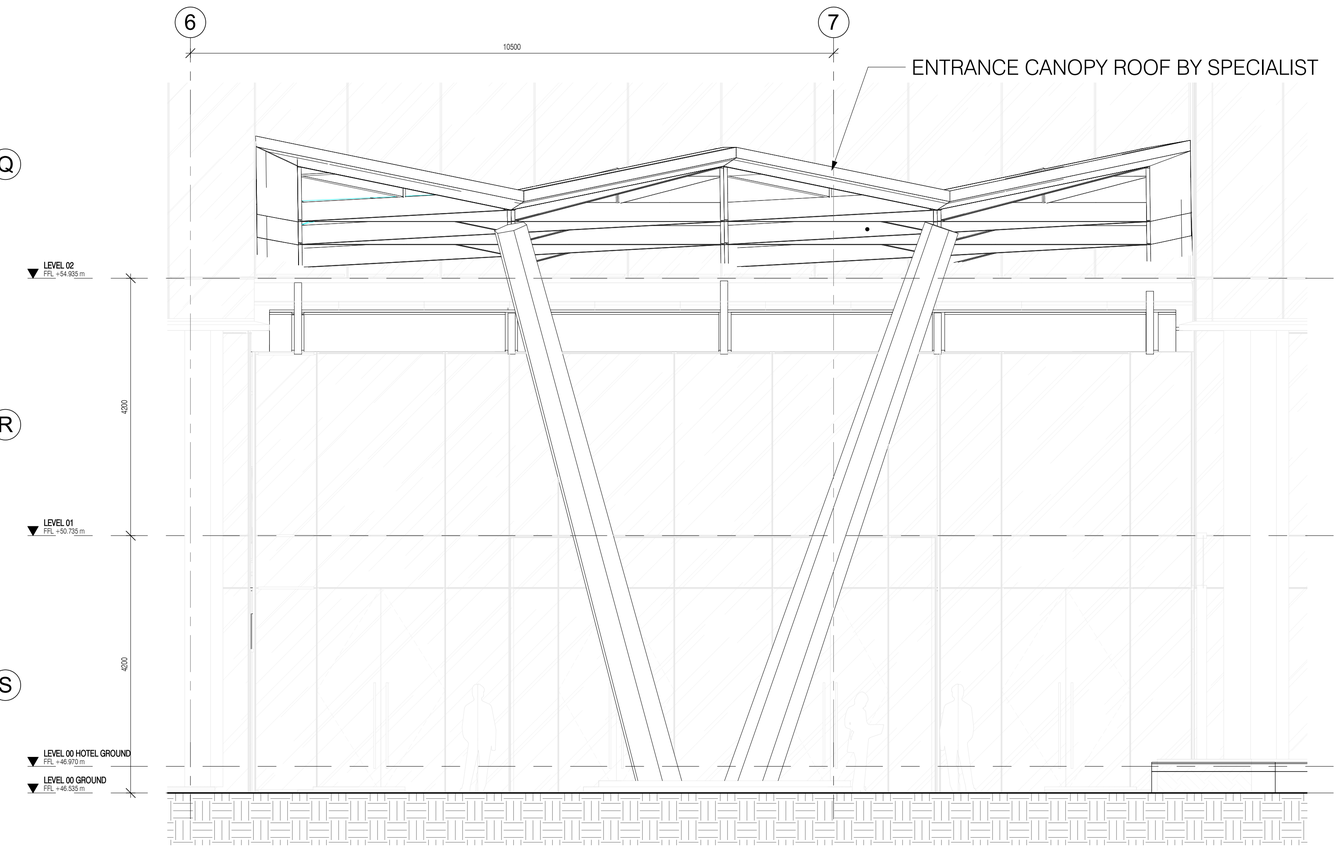

2 Entrance Canopy Section

Scale: 1 : 50

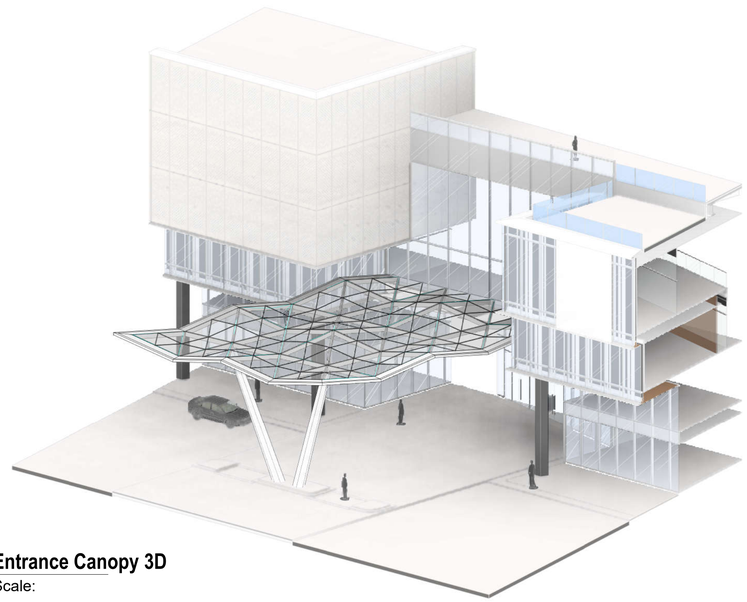

3 Entrance Canopy 3D


Scale:

BENOY disclaimer:

All dimensions to be verified on site. Do not scale this drawing. All discrepancies to be clarified with project Architect. This drawing is the property of Benoy Architects and is issued on the condition it is not reproduced, retained or disclosed to any unauthorised person, either wholly or in part without written consent of Benoy Ltd.

WME disclaimer:

Key Plan

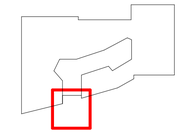

Rev	Date	Description	By	Chk'd
4	17/02/22	Issued for Comment	AG	JN
3	20/12/19	DD SUBMISSION	AS	JN
2	29/11/19	DRAFT DD SUBMISSION	AS	JN
1	18/11/30	Schematic Design	JN	CG

DESIGN CONSULTANT:

BENOY

E: asiapacific@benoy.com
T: +852 2250 7222
www.benoy.com

STRUCTURAL AND MEP CONSULTANT:

WME
T +971 4 388 1616
E info@wmeglobal.com
W www.wmeglobal.com
Dubai | Abu Dhabi | London | Bangalore | Mumbai | Singapore

CLIENT:

OBEROI REALTY
www.oberoirealty.com

Client
Oberoi Realty

Project
Borivali Mixed Use
Borivali East, Mumbai, India

Drawing Title
Entrance Canopy Details

Drawn By	Checked By
A.S.	C.G.

Scale	Sheet Size	Date
As indicated	@ A1 @ A3	30/11/2018

Project No.	Drawing No.	Rev
10980	BNY-MA-33-0001	4

Status
DETAILED DESIGN