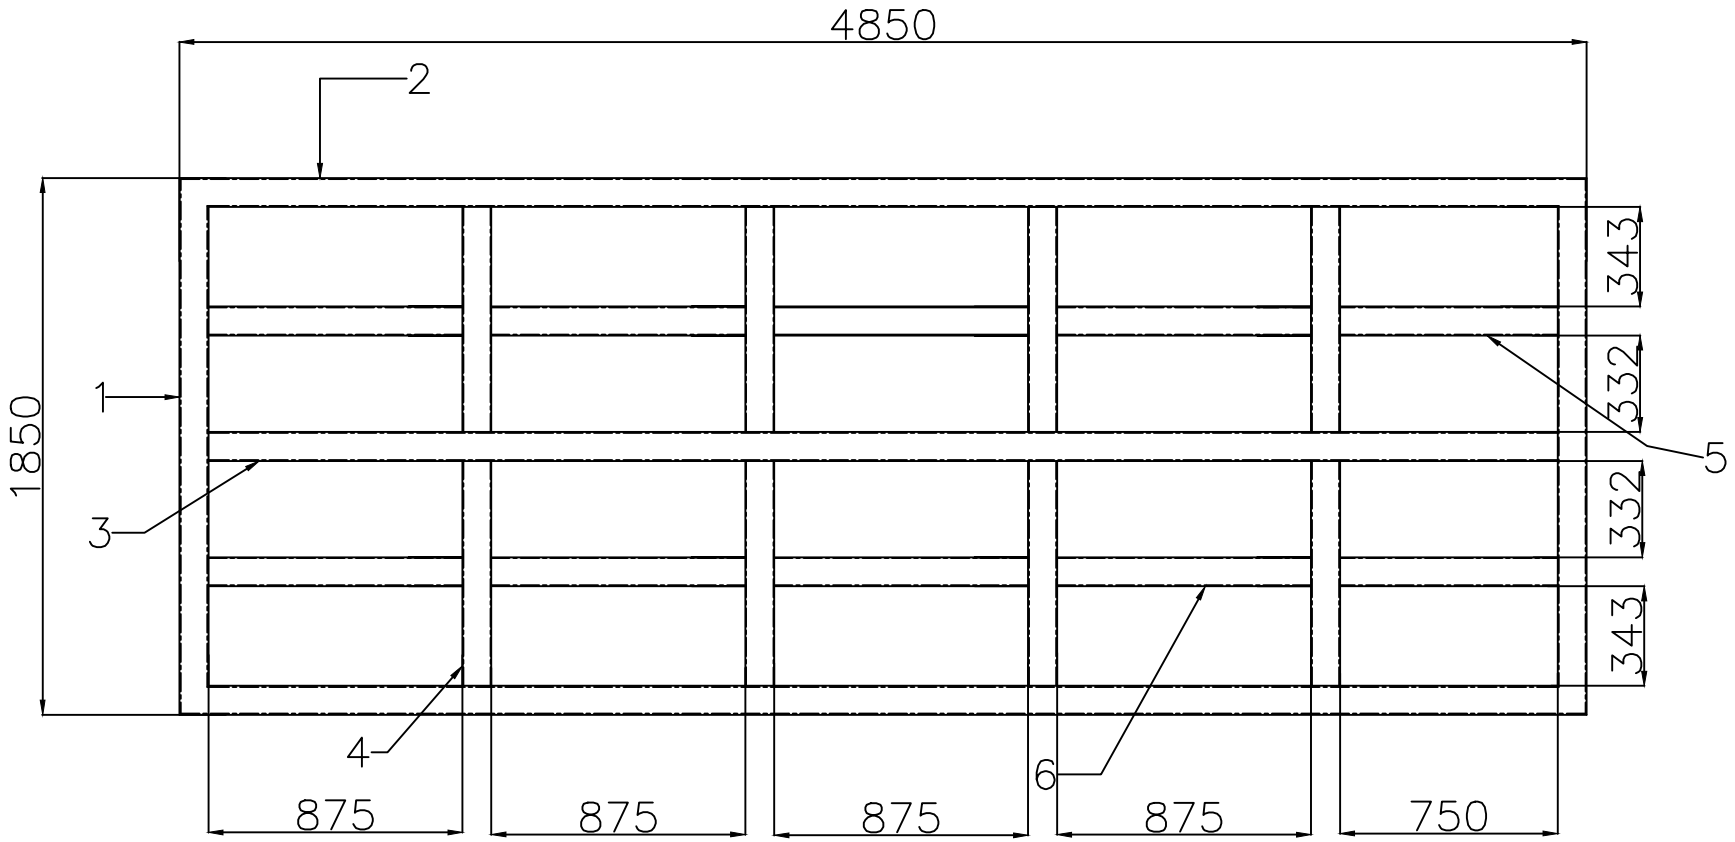

SR. NO.	DESCRIPTION	SPECIFICATION	QTY
1	RECT. TUBE	150 X 150 X 4, 1850 LENGTH	2 NOS
2	RECT. TUBE	150 X 150 X 4, 4850 LENGTH	2 NOS
3	SQ. TUBE	100 X 100 X 3, 4650 LENGTH	1 NOS
4	SQ. TUBE	100 X 100 X 3, 775 LENGTH	8 NOS
5	SQ. TUBE	100 X 100 X 3, 750 LENGTH	2 NOS
6	SQ. TUBE	100 X 100 X 3, 875 LENGTH	8 NOS

REV 01 : 1. ORIENTATION CHANGED FROM LEFT TO RIGHT.

This drawing & design is the property of NIHVA TECHNOLOGIES. Not to be sold or copied to any other concern.

TITLE
SLIDING GATE FRAME

	NAME	SIGN	DATE
DRAWN	G.P.		30.08.21
CHECK	A.K.		30.08.21
APPRD.	V.T.		30.08.21

If any queries contact : design@nihva.com

ALL DIMENSION ARE IN mm

NIHVA
NIHVA TECHNOLOGIES PVT. LTD.

NIHVA TECHNOLOGIES PVT. LTD. PUNE
Tel : 020 66304033
Email:- info@nihva.com
Website:- www.nihva.com

CLIENT -HAIMAVATHY PROPERTIES PVT. LTD.
LOCATION - MUMBAI
PRODUCT - SLIDING GATE 3500 X 2000
NIHVA\21-22\VDR\0132 REV- 00
SCALE: NTS SHEET: 01 OF 01