
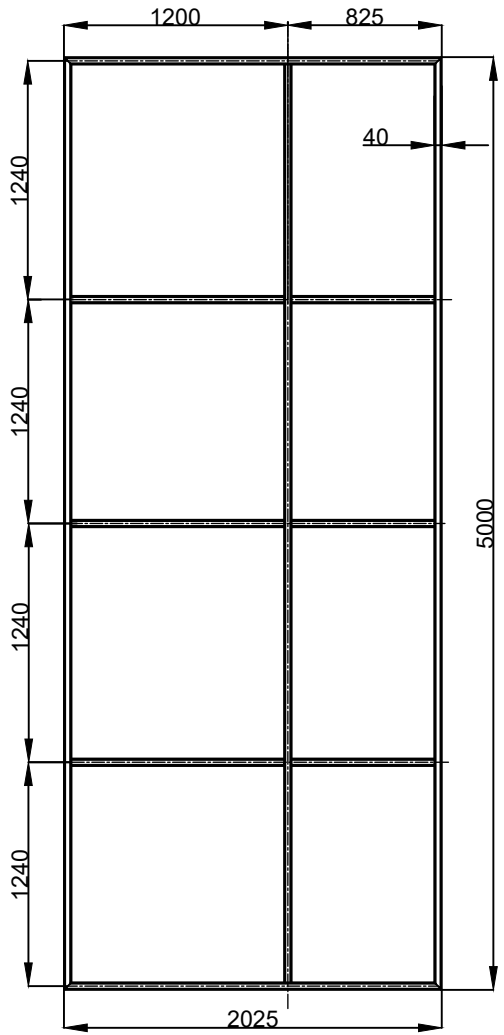


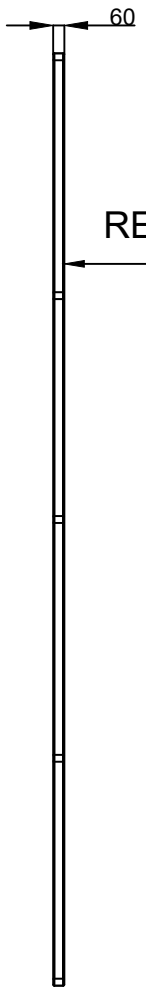

RECT, TUBE 60 X 40 X 3.2 THK

QTY. 4 Nos.

This drawing & design is the property of NIHVA TECHNOLOGIES. Not to be sold or copied to any other concern.

TITLE:- 4 LEAF RIGHT SIDE CRM DOOR 01

NIHVA TECHNOLOGIES PVT. LTD.

NIHVA TECHNOLOGIES PVT. LTD. PUNE
Tel : 020 66304033
Email:- info@nihva.com
Website:- www.nihva.com

	NAME	DATE	SIGN
DRAWN	M.SUTAR	02/05/2022	
CHECK	M.SUTAR	02/05/2022	
APPRD.	V.TARAK	02/05/2022	

If any queries contact : design@nihva.com

ALL DIMENSION ARE IN mm

CLIENT - LESTECH

LOCATION - POSCO MANGAON

PRODUCT - SLIDING DOOR

DWG NO:-NIHVA/22-23/CLT/0014 REV- 0

SCALE: NTS SCALE:-- 1:1 SHEET: 01 OF 01

Rev No.	Revision	Date	Revised By