



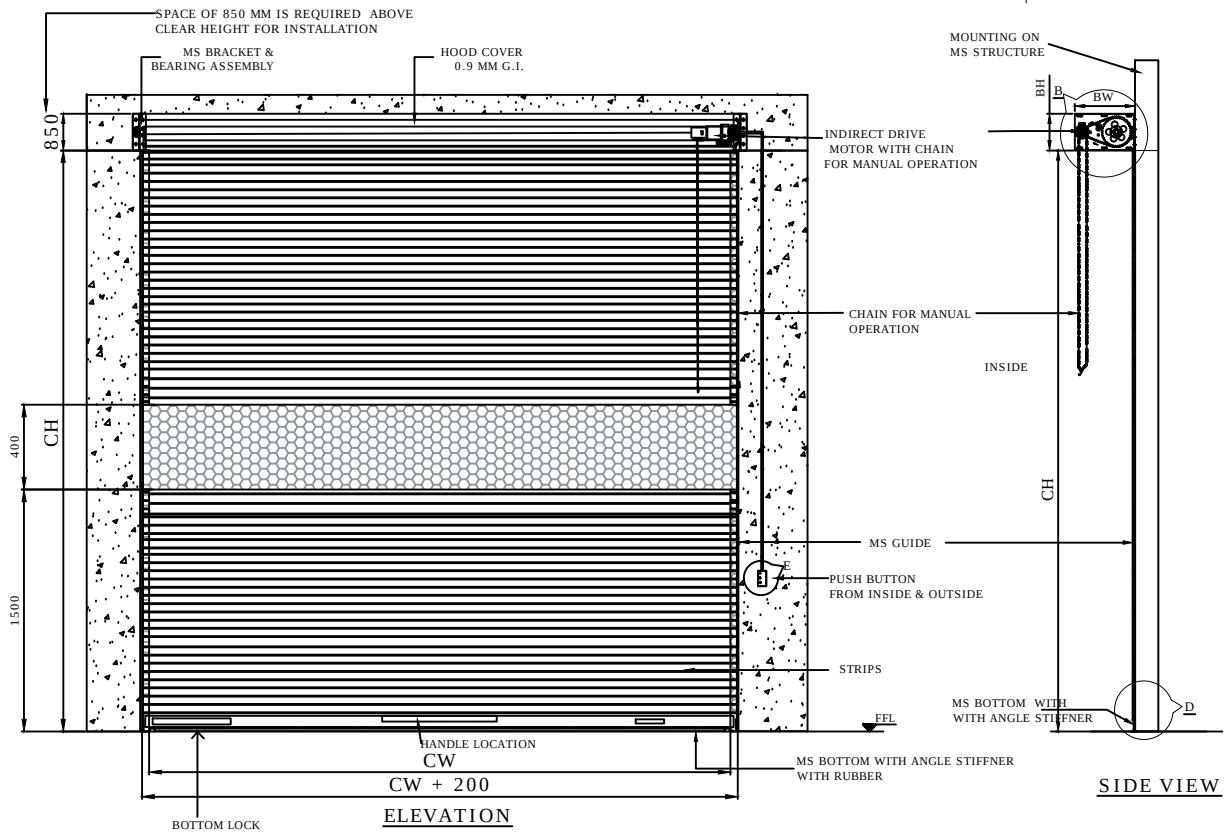


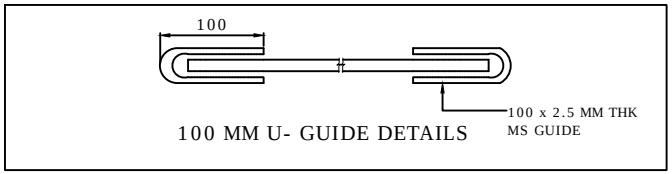

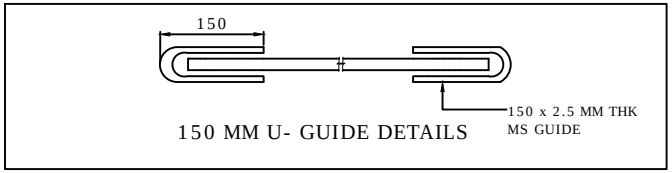


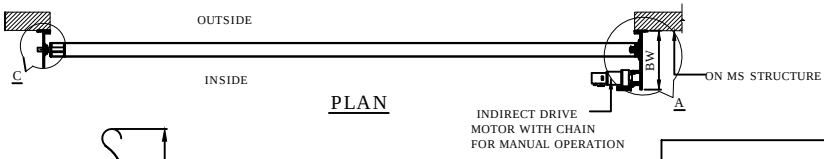


REV NO	DRAWN	DATE	REMARK
R05	S.M.S.	13.5.2021	MOUNTING ON M.S. STRUCTURE
R04	V.C.J.	11.5.2021	OUTSIDE PUSHBUTTON ADDED
R03	S.M.S.	29.4.2021	GRILL & U-GUIDE DETAILS ADDED
R02	S.M.S.	1.4.2021	GUIDE DETAILS UPDATED
R01	S.M.S.	31.3.2021	QTY ADDED & RAL SHADE CONFIRMED

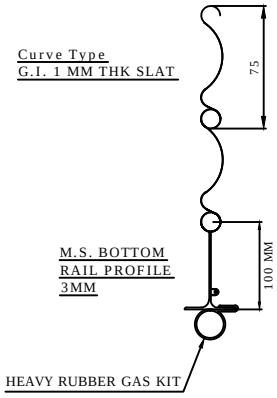

DETAILS : D

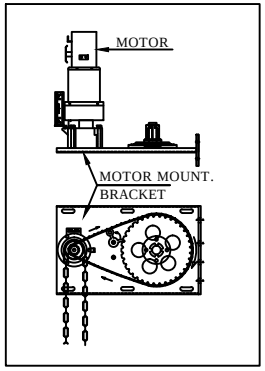

DETAILS : A & B

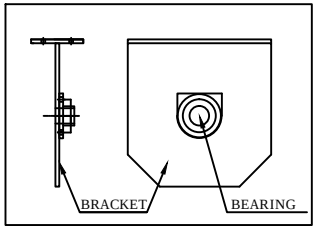

DETAILS : C

RAL CODE	SHADE	COLOUR
RAL 9002	GREY WHITE	

SR NO	CLEAR WIDTH (CW)	CLEAR HEIGHT (CH)	QUANTITY	RAL COLOR POWDER COATED
1	4000	4000	5 NOS	RAL 9002

This drawing & design is the property of NIHVA TECHNOLOGIES. Not to be sold or copied to any other concern.

TITLE GI MOTORIZED INDIRECT DRIVE ROLLING SHUTTER

NIHVA TECHNOLOGIES PVT. LTD.

NIHVA TECHNOLOGIES PVT. LTD. PUNE
Tel : 020 66304033
Email:- info@nihva.com
Website:- www.nihva.com

	NAME	SIGN	DATE
DRAWN	S.M.S.		16.3.2021
CHECK	S.M.S.		16.3.2021
APPRD.			

CLIENT - ARP CONSTRUCTION

PROJECT - JOHN DEERE

SITE LOCATION - SANASWADI , PUNE

If any queries contact : projectsupport@nihva.com

DWG. NO. : NIHVA/20-21/0177/R05 REV- R05

ALL DIMENSION ARE IN mm

SCALE: NTS WT: SHEET: