

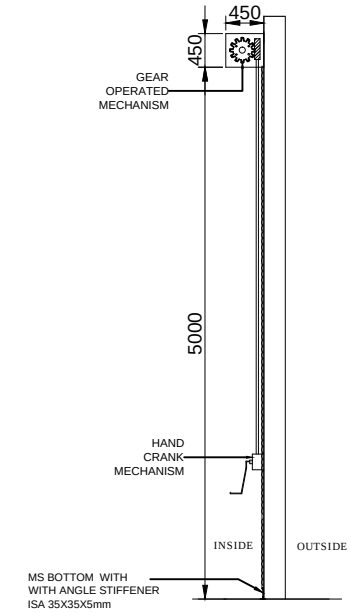



SIDE VIEW

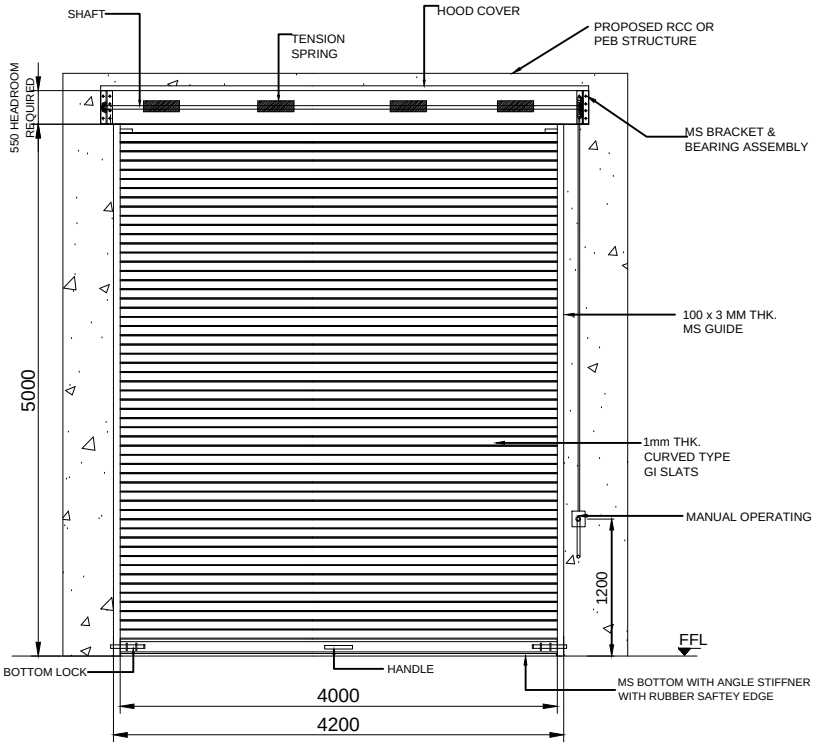


INSIDE ELEVATION

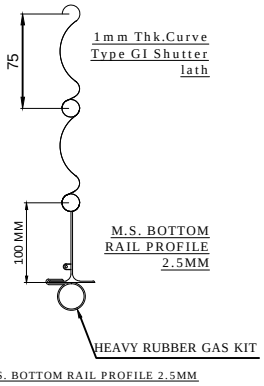

M.S. BOTTOM RAIL PROFILE 2.5MM

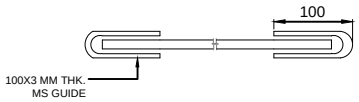

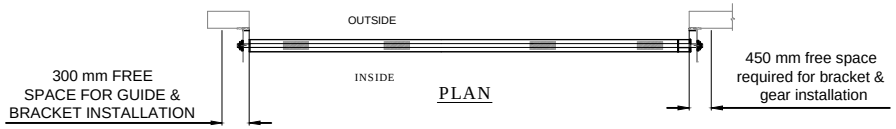

PLAN

TOLERANCE - ±10mm

S.N.	LOCATION	SIZE	QUANTITY
1	B7E	4000(W)X5000(H)	01

NOTE-
1. ALL CIVIL WORK WILL BE CLIENT'S SCOPE.
2.STRUCTURE REQUIRED FOR SHUTTER IS IN CLIENT'S SCOPE.
3.FINAL FINISH OF SHUTTER WILL BE IN POWDER COATING OF APPROVED COLOR i.e. RAL 7001.

This drawing & design is the property of NIHVA TECHNOLOGIES. Not to be sold or copied to any other concern.

TITLE	GEAR OPERATED ROLLING SHUTTER 4mX5m With Right side gearbox			NIHVA TECHNOLOGIES PVT. LTD. Website:- www.nihva.com	NIHVA TECHNOLOGIES PVT. PUNE Tel : 020 66304033 Email:- info@nihva.com
	NAME	SIGN	DATE		
DRAWN	SURAJ		04.09.2018	CLIENT -	
CHECK	PRADEEP		04.09.2018	PROJECT -	
APPRD.	R.D		04.09.2018	SITE LOCATION -	
If any queries contact : design@nihva.com				DWG. NO. : NIHVA/18-19/VDR/116	REV- 0
ALL DIMENSION ARE IN mm				SCALE: NTS	WT: SHEET: 01 OF 01