


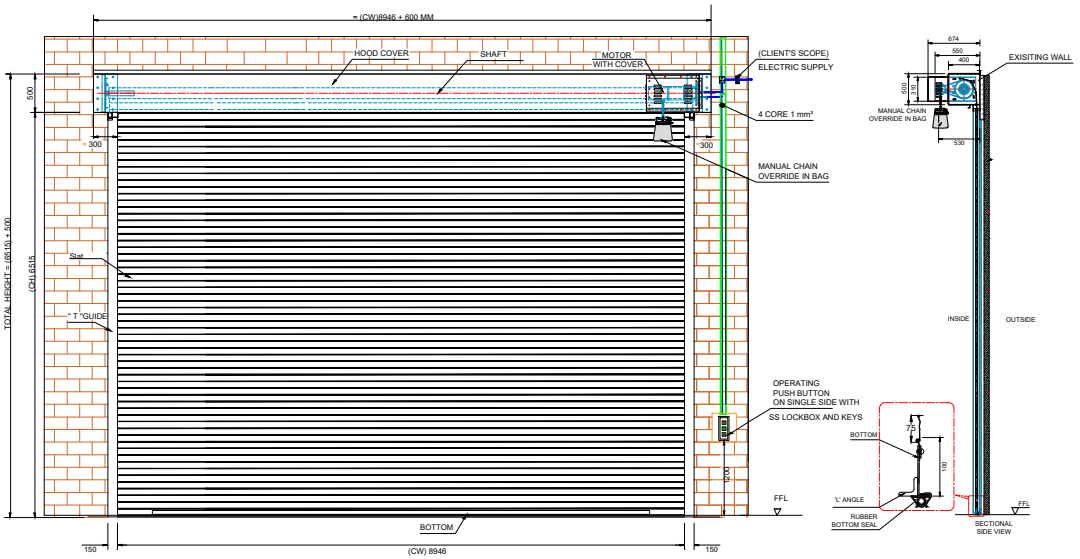

TECHNICAL SPECIFICATION:-

SR.	SPECIFICATION	DETAILS
1.	DESCRIPTION & DRIVE	INDIRECT DRIVE MOTOR .
2.	LOCATION AREA	INSIDE / OUTSIDE
3.	MOUNTING SURFACE	SIDE BRACKETS: OPTIONAL+ON CONCRETE/STEEL&SIDE
4.	SLAT	GI SHEET - 1.2 MM THK (WIDE 75MM)
5.	BOTTOM PROFILE	MS BOTTOM PROFILE
6.	GUIDE PROFILE	M.S."T" SHAPE 100X150X3 MM THK .
7.	HOOD COVER & MOTOR COVER	MADE OF GI SHEET THICKNESS 0.9 MM.
8.	MATERIAL FINISH	AS PER CLIENT REQ.
9.	PUSH BOTTON	3 WAY PUSH BUTTON ON SINGLE SIDE

SHUTTER SIZES :-

SR.	CLEAR WIDTH	CLEAR HEIGHT	QTY.
01	8946mm	6515mm	01

Note :-

1. All Dimension are in mm

This drawing & designing is the property of NIHVA TECHNOLOGIES. Not to be sold or copied to any other concern

TITLE :- MOTORISED ROLLING SHUTTER

NIHVA TECHNOLOGIES PVT. LTD. PUNE
Tel : 020 66304033
Email:- info@nihva.com
Website:- www.nihva.com

	NAME	DATE
DRAWN	J.P.	14/10/2025
CHECK & APPROVAL	B.S.	14/10/2025

CLIENT - KLE HOSPITAL
PROJECT - MOTORISED ROLLING SHUTTER
FORMAT NO - NIHVA-DD-F-03
DWG. NO. : NIHVA/24-25/GB/2411001 REV-00
SCALE: NTS WT: SHEET: 01 OF 01
ALL DIMENSION ARE IN mm
If any queries contact : design@nihva.com