
ART OF LIVING YOGA AND MEDITATION CENTER BANGLORE

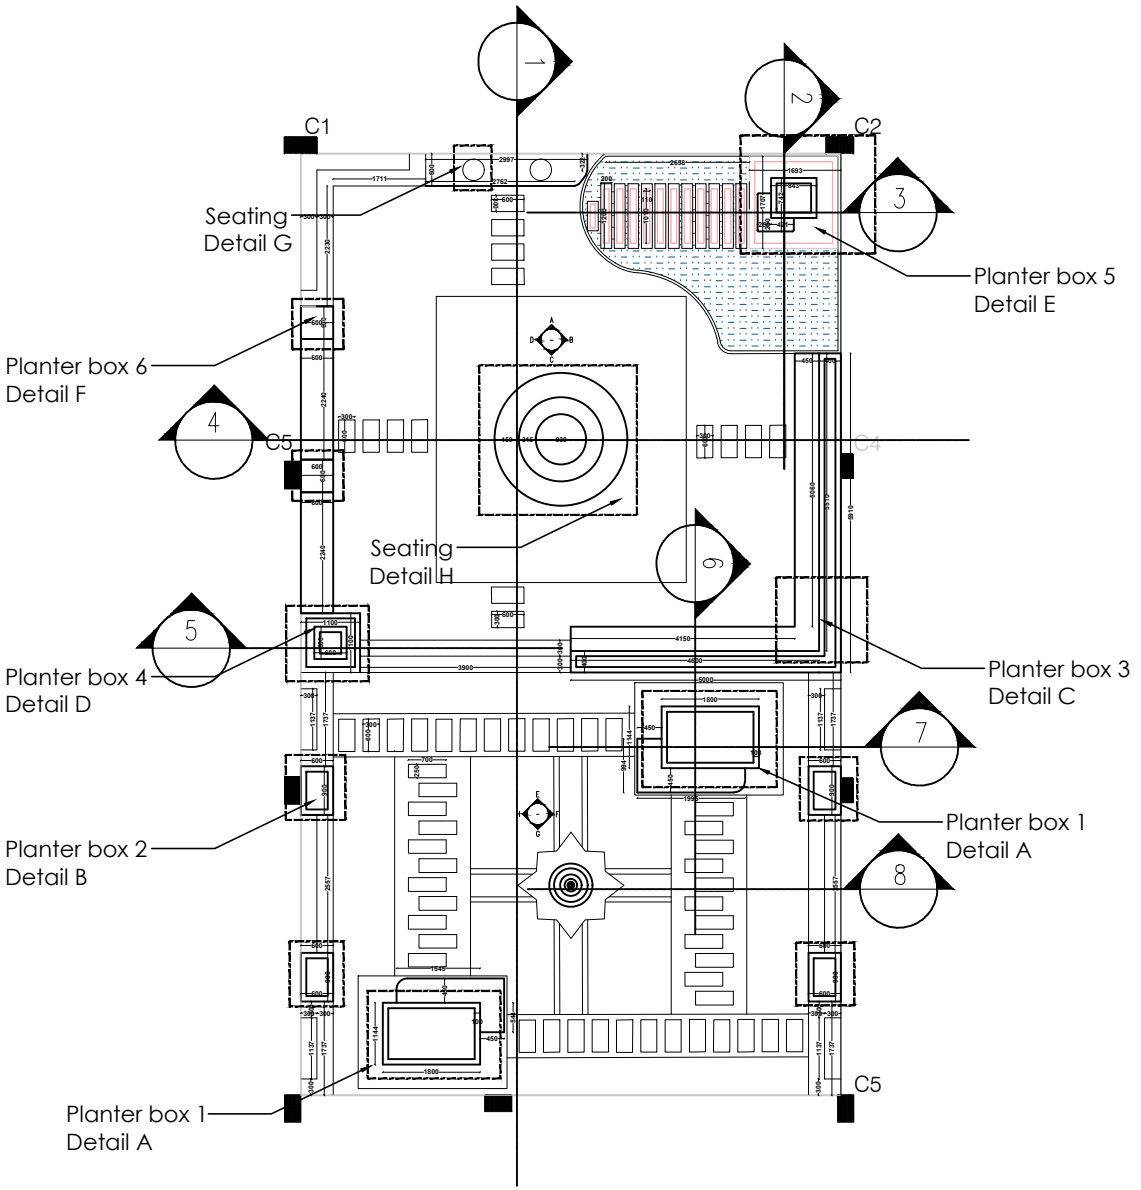

Courtyard plan 1

SCALE 1: 100

NOTES.

1. All dimensions are in millimeters and all levels are given in meters unless otherwise noted.
2. All drawings must be read in conjunction with all other architectural and engineering drawings related to the same sheet and any item on it.
3. Wall, column thickness shown here are excluding plastering
4. Refer Joinery Details for window openings and sill levels

DRAWING NAME

COURTYARD PLAN

DRAWING NUMBER	REV
ABH-SCR-AR-520	R0
SCALE - 1: 100	A3

OCCUPANCY -

ISSUED BY 22 -09 -2023

DRAWN BY Ar .Anzi EA

DRAWING TYPE GFC

CHECKED CHECKED

NO.	DATE	REVISIONS

SCHEDULE OF OPENINGS

*please refer joinery details for schedule of openings

PROJECT:

ART OF LIVING YOGA AND MEDITATION CENTER

CLIENT:

SUMERU

Sri Sumeru Reality Pvt. Ltd
2nd Floor, SAMVIT, Next to Art of Living Ashram
Near Udayapura Bus Stop,21st KM
Kanakapura Main Road, Bengaluru 560082

ARCHITECTS:

ABHILASH ARCHITECTS

ABHILASH ARCHITECTS
Near Art Of Living, Ashramam
Thappilkadavu, Kollam
Kerala, India
Pin- 691012

Tele No: +914742792144