
DWG.NO: SALT_1729_STR_07_R0

M379 — 3, 150, 8121
M361 — 8300
M306 — 83, 132, 5702
M313 — 4033, 336, 132, 336
M316 — 4142, 347, 132, 347
M315 — 348, 132, 348, 4150
M318 — 155, 140, 150, 5299
M365 — 112, 180, 5695
M12 — 8000
M10 — 85, 72, 85, 2176
M11 — 2092, 72, 81, 81
M13 — 2175, 85, 72, 85
M7 — 81, 72, 81, 2095
M8 — 2173, 85, 72, 85
M9 — 2169, 85, 72, 85
M5 — 2536, 108, 72, 108
M90 — 46, 50, 46, 1877
M91 — 1874, 50, 46, 46
M92 — 1949, 50, 49, 49
M245 — 72, 51, 51, 1709
M246 — 3941, 72, 191, 191
M518 — 72, 55, 55, 1735
M519 — 53, 72, 53, 1717
M517 — 1350
M382 — 15849
M157 — 31581
M498 — 1425
M381 — 23295
M214 — 1350
M6 — 1350
M135 — 421, 150, 50, 3873
M140 — 97, 150, 5701
M151 — 18229, 3
M87 — 1939, 50, 49, 49
M89 — 1350
M88 — 50, 50, 50, 1953
M93 — 1985, 100, 98, 98
M96 — 2503, 75, 50, 75
M3 — 266, 100, 266, 4099
M4 — 3989, 72, 189, 189
M120 — 137, 220, 5707
M152 — 25730
M191 — 114, 180, 120, 10159
M230 — 5334, 100, 94, 106
M384 — 21700
M383 — 83194
M121 — 86, 220, 91, 8675
M122 — 145, 220, 151, 9859
M97 — 58, 50, 58, 2127
M501 — 65, 72, 65, 1881

ISOMETRIC VIEW

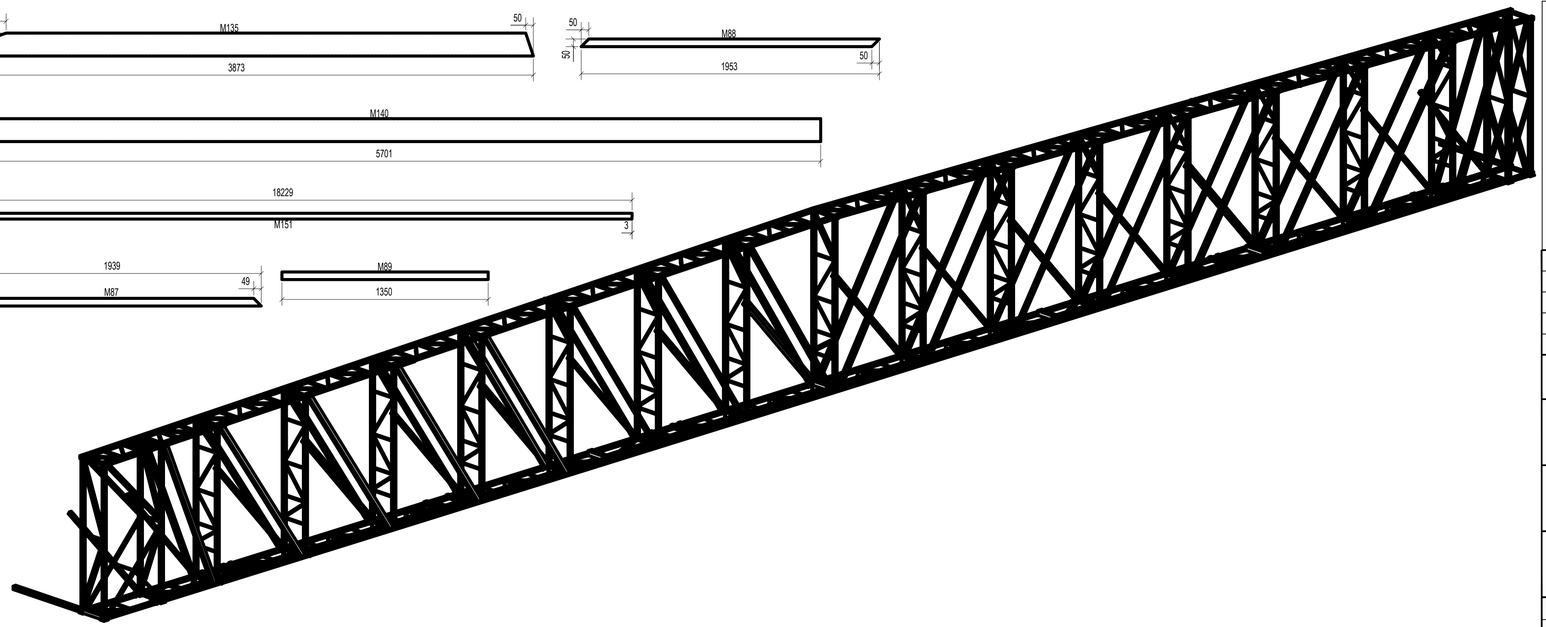

NOTES :-

1. ALL DIMENSIONS ARE IN MM & LEVEL ARE IN METER.
2. ALL STRUCTURAL STEEL AS PER IS:2062.
3. PROVIDE WELDING AS PER IS:816.
4. PROVIDE MIN. 6MM WELD WITH MIN. WELD LENGTH OF 150MM.
5. USE ELECTRODS AS PER IS:814 (PT.–I).
6. FILLET/ BUTT WELD SHALL BE OF 6MM SIZE AND SHALL BE CONTINUOUS.
7. FABRICATION AND ERECTION SHALL BE AS PER IS:800 AND IS:803.
8. WELD SHALL BE GROUND SMOOTH.
9. ALL GUSSET PLATES SHALL BE MIN. 10 THK.
10. ALL M.S. BLACK BOLTS AND NUTS SHALL CONFORM TO IS:1363(PT. 1 TO 3).
11. STRUCTURE SHALL BE APPLIED WITH ONE COAT OF RED OXIDE ZINC CROMATE PRIMER AFTER FABRICATION FOLLOWED ONE MORE COAT BEFORE ERECTION. FINALLY APPLY 2 COATS OF SYNTHETIC ENAMAL OF APPROVED QUALITY.

REV.NO.	DESCRIPTION.	REV.DATE	DRAWN.	CHKD.	APPD.
0	DRAWING FOR APPROVAL	27.12.22	AAK	HAB	HAB

DWG.TITLE :- CUTTING DETAILS FOR 99.00M TRUSS

PROJECT	MEGADOOR INSTALLATION AT HYDRABAD AIRPORT
CLIENT	GMR

SALT Design Services
NIHVA TECHNOLOGIES PVT.LTD.

SALT DESIGN SERVICES

NIHVA TECHNOLOGIES PVT. LTD. PUNE
Tel : 020 66304033
Email:- info@nihva.com
Website:- www.nihva.com

DRAWN :AAK	CHECKED : HAB	SCALE: 1:100
APPROVED : HAB	JOB CODE. : 1729	DATE: 27.12.2022
DWG.NO: SALT_1729_STR_07_R0	(SH-1OF1)	REV. - R0
		SIZE. - A0

A1 [841 x 594]