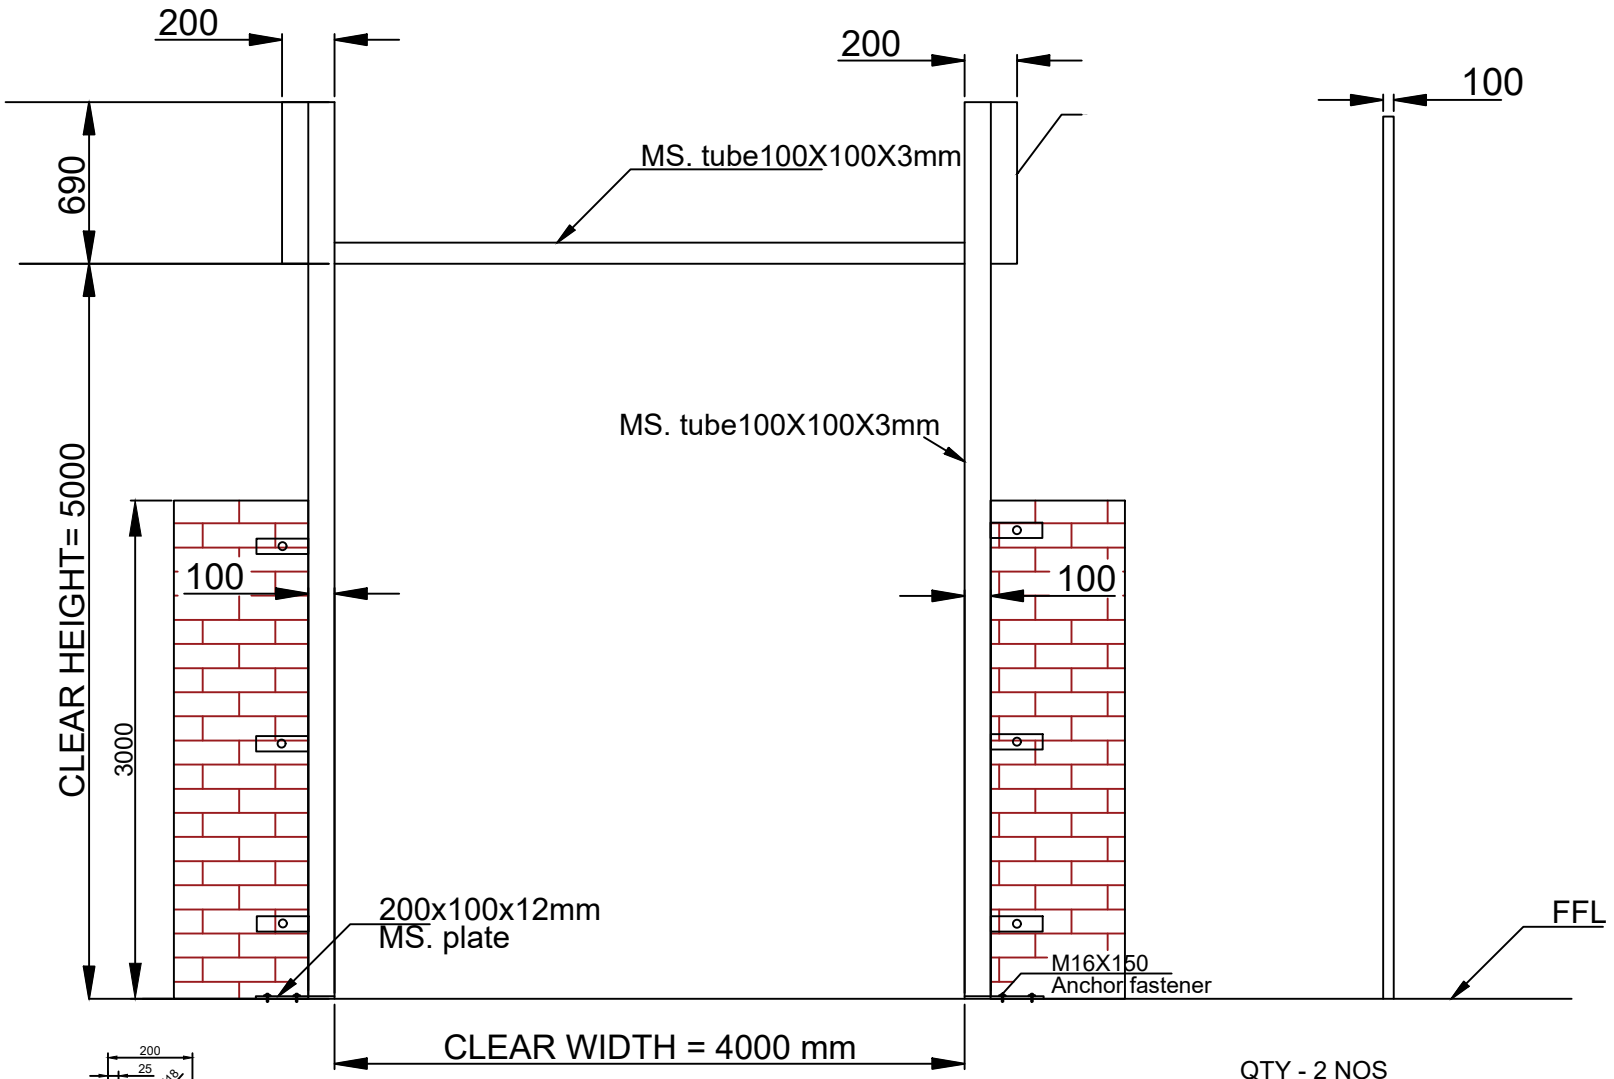


QTY - 2 NOS

NOTE -

(1) ALL CIVIL WORK IN CLIENT SCOPE .

This drawing & design is the property of NIHVA TECHNOLOGIES. Not to be sold or copied to any other concern.

TITLE: HIGH SPEED DOOR STRUCTURE				NIHVA TECHNOLOGIES PVT. LTD. PUNE Tel : 020 66304033 Email:- info@nihva.com Website:- www.nihva.com
	NAME	SIGN	DATE	
DRAWN	B.S		21.11.2025	CLIENT -JAYASHREE POLYMERS PVT. LTD.
CHECK	V.T		21.11.2025	PROJECT -..
APPRD.	V.T		21.11.2025	LOCATION - PUNE
If any queries contact : design1@nihva.com				DWG. NO. : NIHVA/24-25/xxx / REV- 0
ALL DIMENSION ARE IN mm				SCALE: NTS / WT: / SHEET: 01 OF 01