



CONTROL PANEL IS PROVIDED WITH 5 METER CABLE LENGTH AS STANDARD.

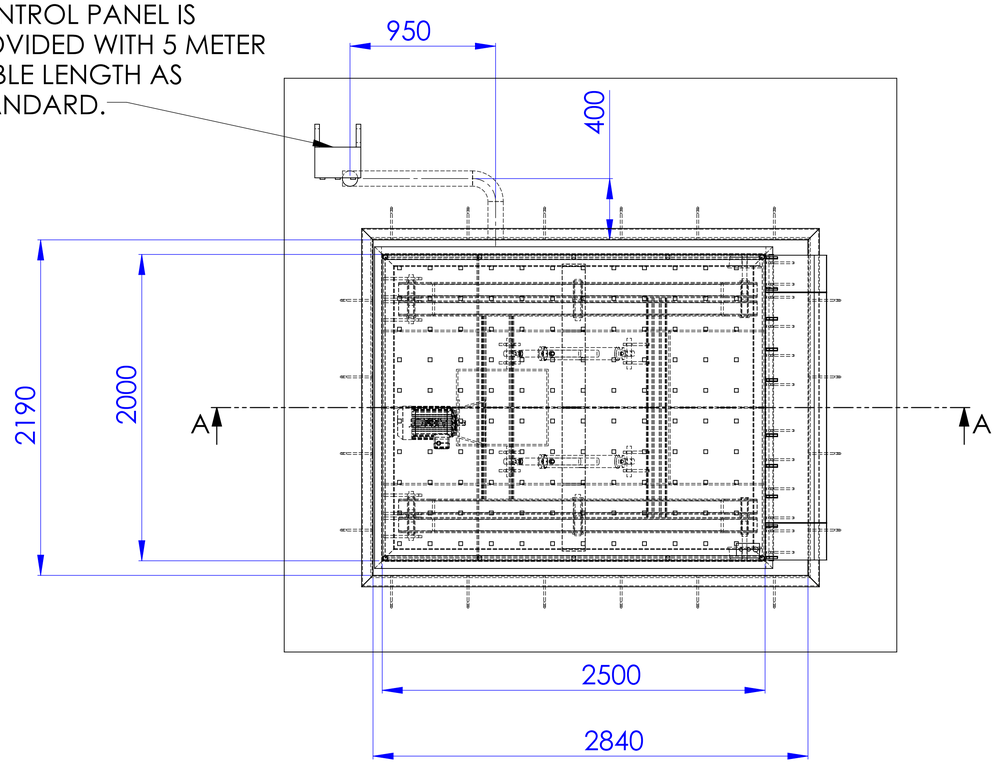

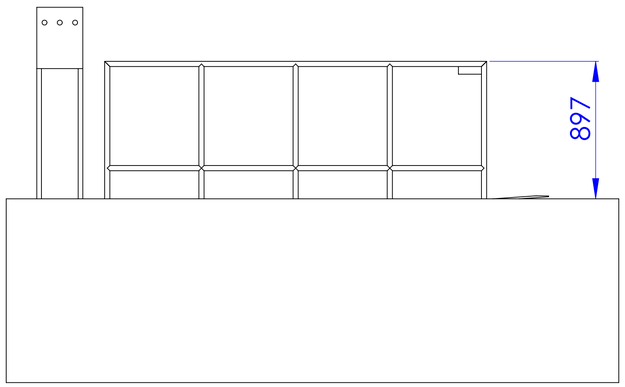

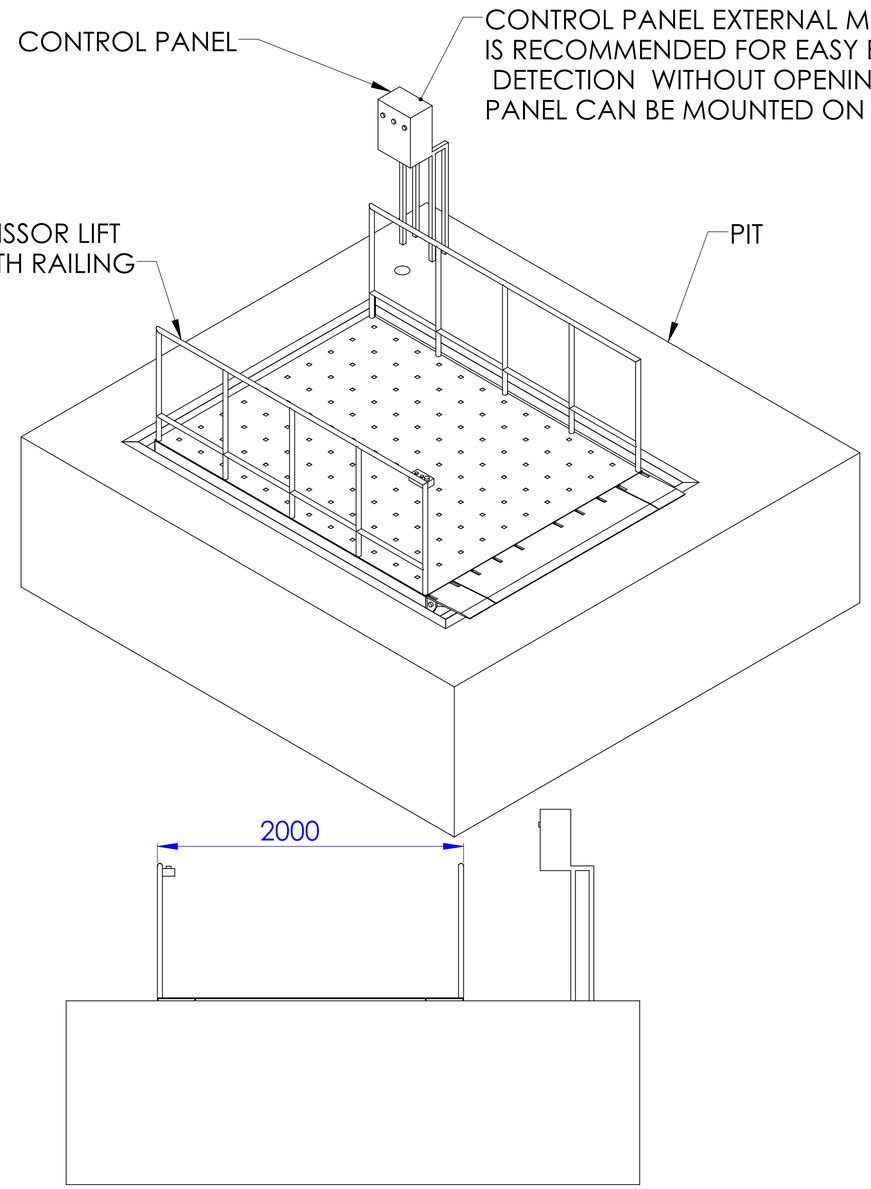

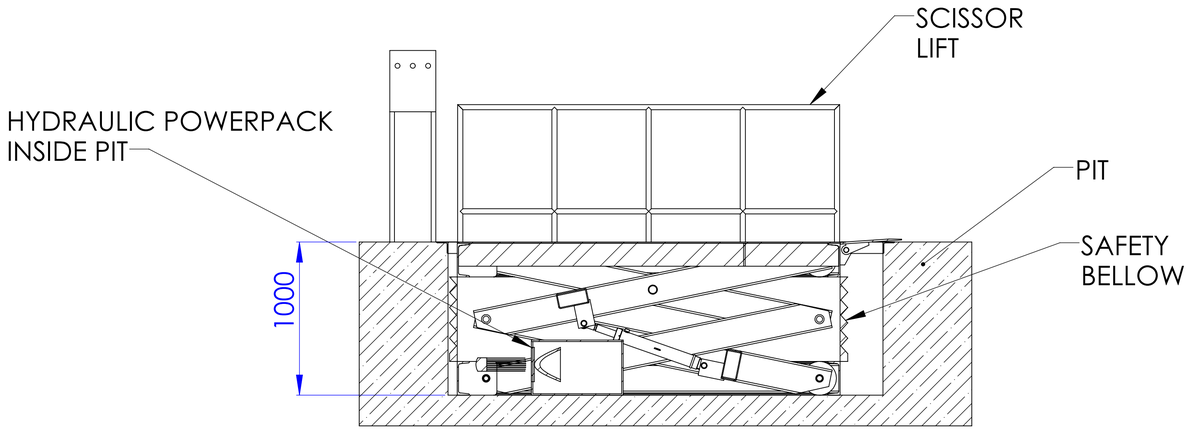

SECTION A-A

NOTES-
1. SCISSOR LIFT WILL BE INSTALLED IN PIT AT SITE .
2. REFER ATTACHED SCISSOR LIFT DRAWING FOR SPECIFICATIONS.
3. REFER ATTACHED PIT DRAWING FOR CIVIL WORK .
4. SCISSOR LIFT QTY - 4 NOS
5. SCISSOR LIFT CAPACITY-6 TON POINT LOAD 15 TON UDL

UNLESS OTHERWISE SPECIFIED:
DIMENSIONS ARE IN MILLIMETERS
SURFACE FINISH:
TOLERANCES:
LINEAR:
ANGULAR:

NIHVA
We Make Possible

DEBURR AND BREAK SHARP EDGES


DO NOT SCALE DRAWING | REVISION R00


	NAME	SIGNATURE	DATE
DRAWN	SIDDHESHWAR		2.7.2021
CHK'D			
APP'D			
MFG			
Q.A			

MATERIAL: M.S.
WEIGHT:


INSTALLATION LAYOUT


DWG.NO. NTPL-SL-XX-LAYOUT-0000 | A1
SCALE:1:20 | SHEET 1 OF 1

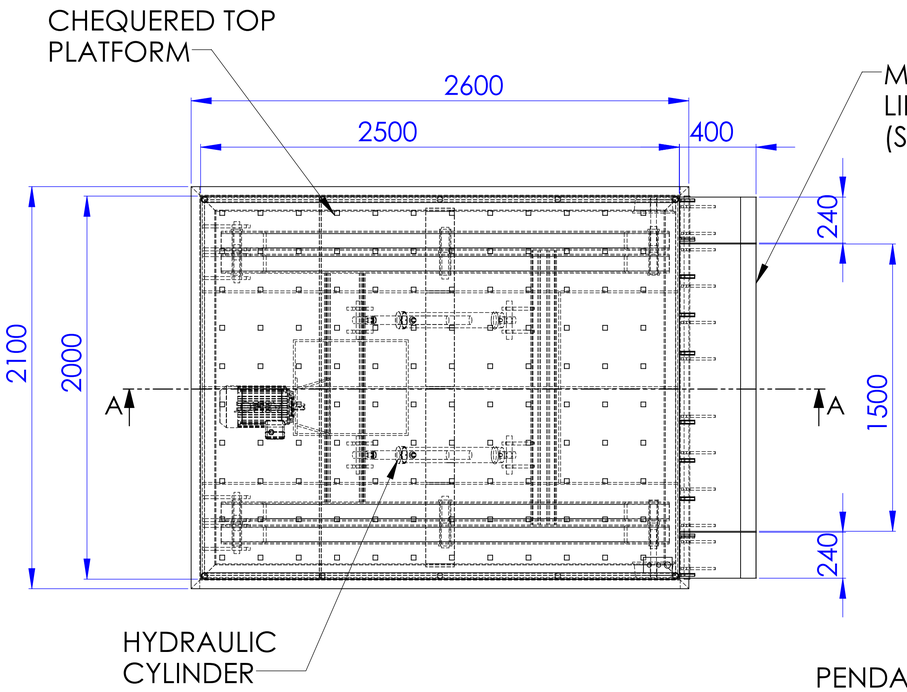


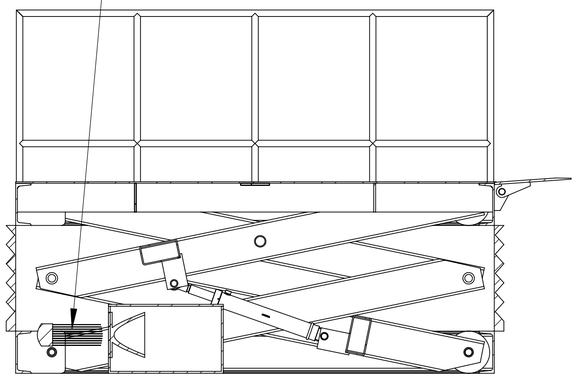


SECTION A-A
SCALE 1 : 16

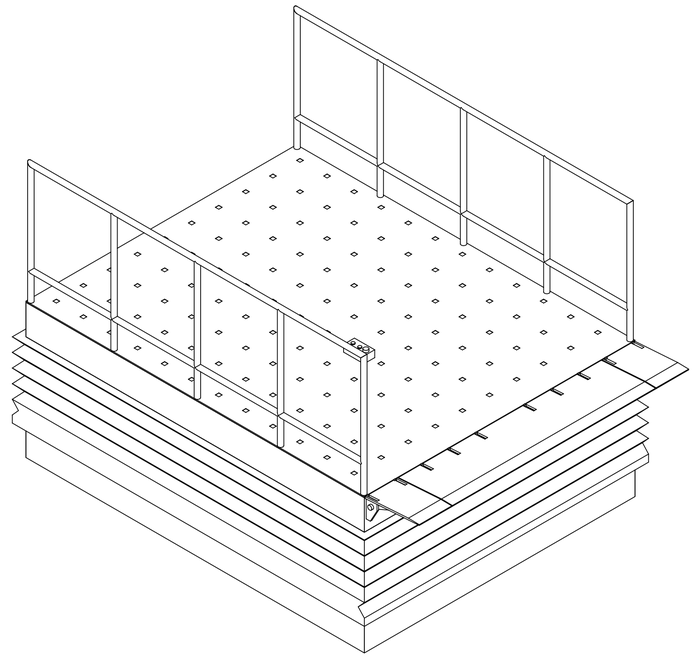

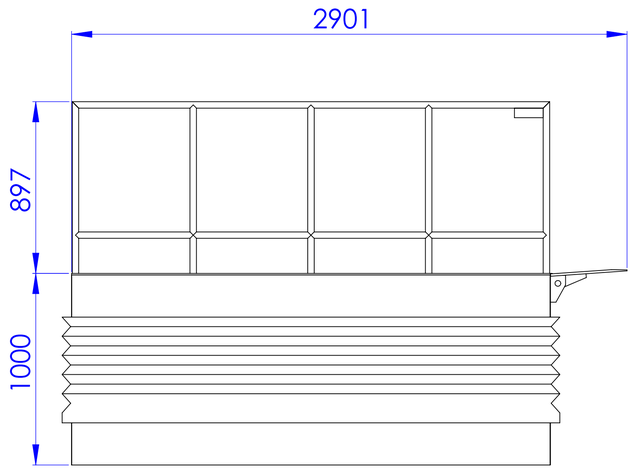

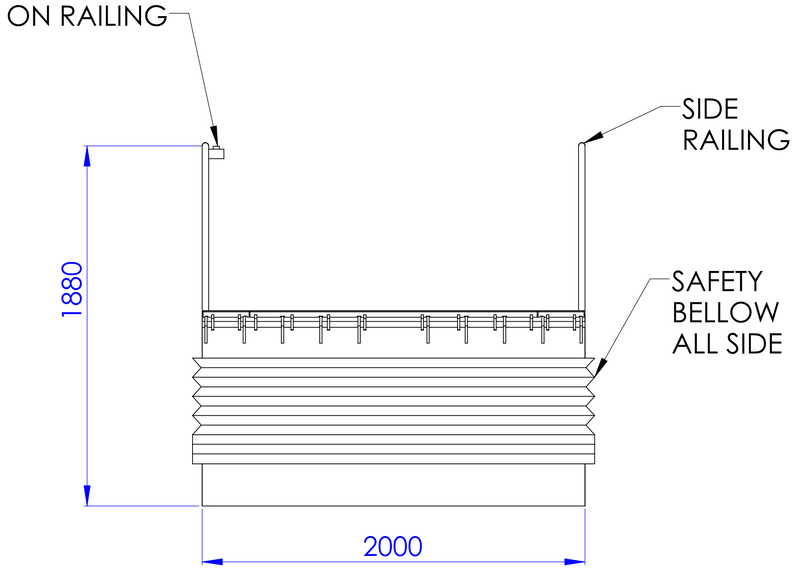

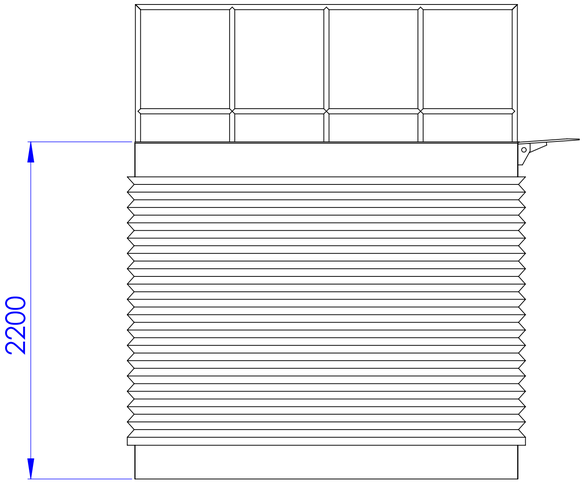

SPECIFICATIONS OF SCISSOR LIFT-

1. PLATFORM SIZE- 2000WX2500L
2. CAPACITY - 6 TON POINT LOAD 15TON UDL
3. CLOSE HEIGHT - 1000 MM
4. LIFT HEIGHT - 1200 MM
5. TOTAL HEIGHT FROM PIT BOTTOM - 2200 MM
6. LIFTING BY 2 NOS OF HYDRAULIC CYLINDER
7. HYDRAULIC POWERPACK - 5 HP , 3 PHASE AC PROVIDED INSIDE PIT
8. MANUAL TYPE LIP PLATE- SPLIT TYPE (240+1500+240)
9. SAFETY RAILING ON LENGTH SIDE
10. MAINTENANCE STOPPER PROVIDED FOR SERVICE & MAINTENANCE
11. QTY- 4NOS
12. FINISH - HOT DEEP GALVANISING
13. OPERATION CONTROL BY PENDANT MOUNTED ON RAILING
14. CONTROL PANEL IS PROVIDED OUTSIDE PIT FOR EASY ELECTRICAL FAULT DETECTION WITHOUT NEED OF REMOVING SAFETY BELLOW .
15. SAFETY BELLOW PROVIDED ON ALL SIDE.

UNLESS OTHERWISE SPECIFIED:
DIMENSIONS ARE IN MILLIMETERS
SURFACE FINISH:
TOLERANCES:
LINEAR:
ANGULAR:

NIHVA
We Make Possible

DEBURR AND BREAK SHARP EDGES

	NAME	SIGNATURE	DATE
DRAWN	SIDDHESHWAR		2.7.2021
CHK'D			
APPV'D			
MFG			
Q.A			


MATERIAL: M.S.
WEIGHT:


TITLE: SCISSOR LIFT


DWG NO. NTPL-SL-XX-SCISSORLIFTASS-0000

A1


SCALE:1:20 SHEET 1 OF 1

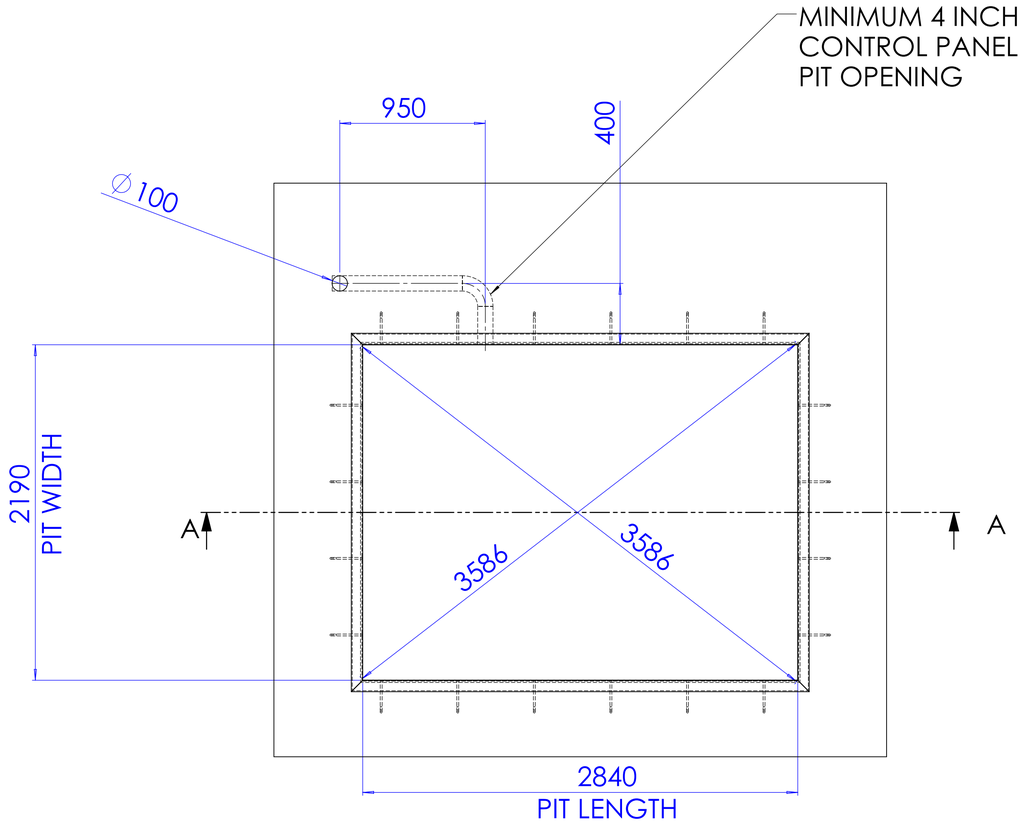

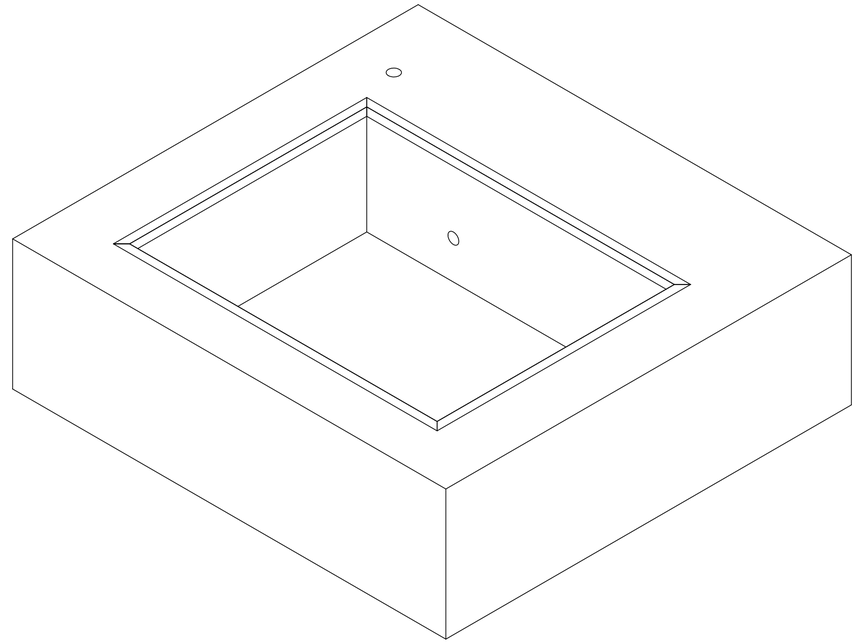

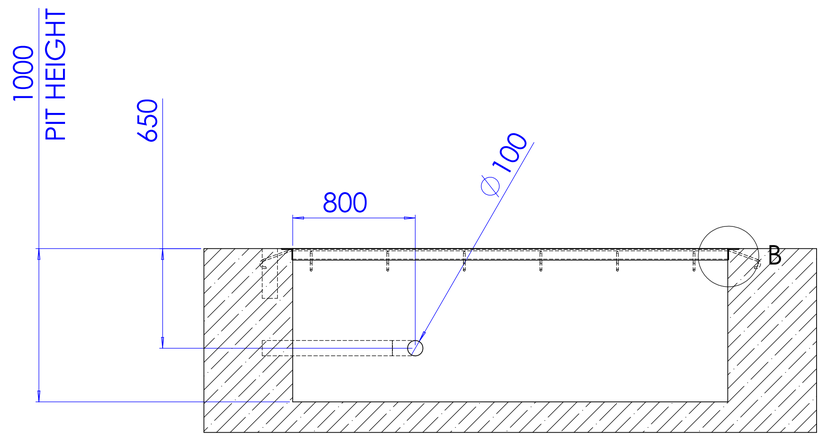

SECTION A-A

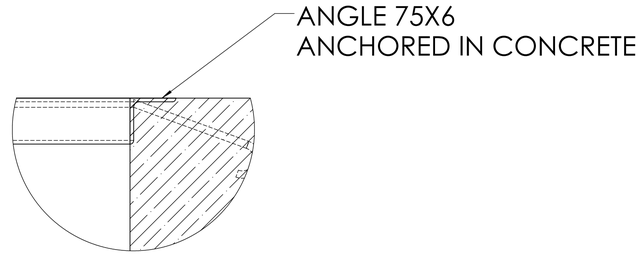

DETAIL B
SCALE 1 : 5

NOTES-
1. ALL CIVIL WORK & PIT IS IN CLIENT SCOPE .
2. ANGLE 75X6 MM THK IS ANCHORED AT ALL EDGES OF PIT . REQUIRED ANGLE IS IN CLIENT SCOPE ,
3. MINIMUM 4 INCH DUCT TO BE PROVIDED FROM POWERPACK TO PIT OPENING (DUCT IS IN CLIENT SCOPE).
4. PIT SURFACE SHOULD BE PLAIN & PIT SURFACE SHOULD TAKE LOAD OF ATLEAST 8 TON POINT LOAD .
5. PIT CLEAR SIZE - 2190WX2840X1000H.

UNLESS OTHERWISE SPECIFIED: DIMENSIONS ARE IN MILLIMETERS SURFACE FINISH: TOLERANCES: LINEAR: ANGULAR:	NIHVA We Make Possible		DEBURR AND BREAK SHARP EDGES	DO NOT SCALE DRAWING	REVISION R00
	NAME	SIGNATURE	DATE	PIT DRAWING	
DRAWN	SIDDHESHWAR		2.7.2021		
CHK'D					
APPV'D					
MFG					
Q.A					
MATERIAL: M.S.				DWG NO: NTPL-SL-XX-PITASS-0000	A1
WEIGHT:				SCALE:1:20	SHEET 1 OF 1