

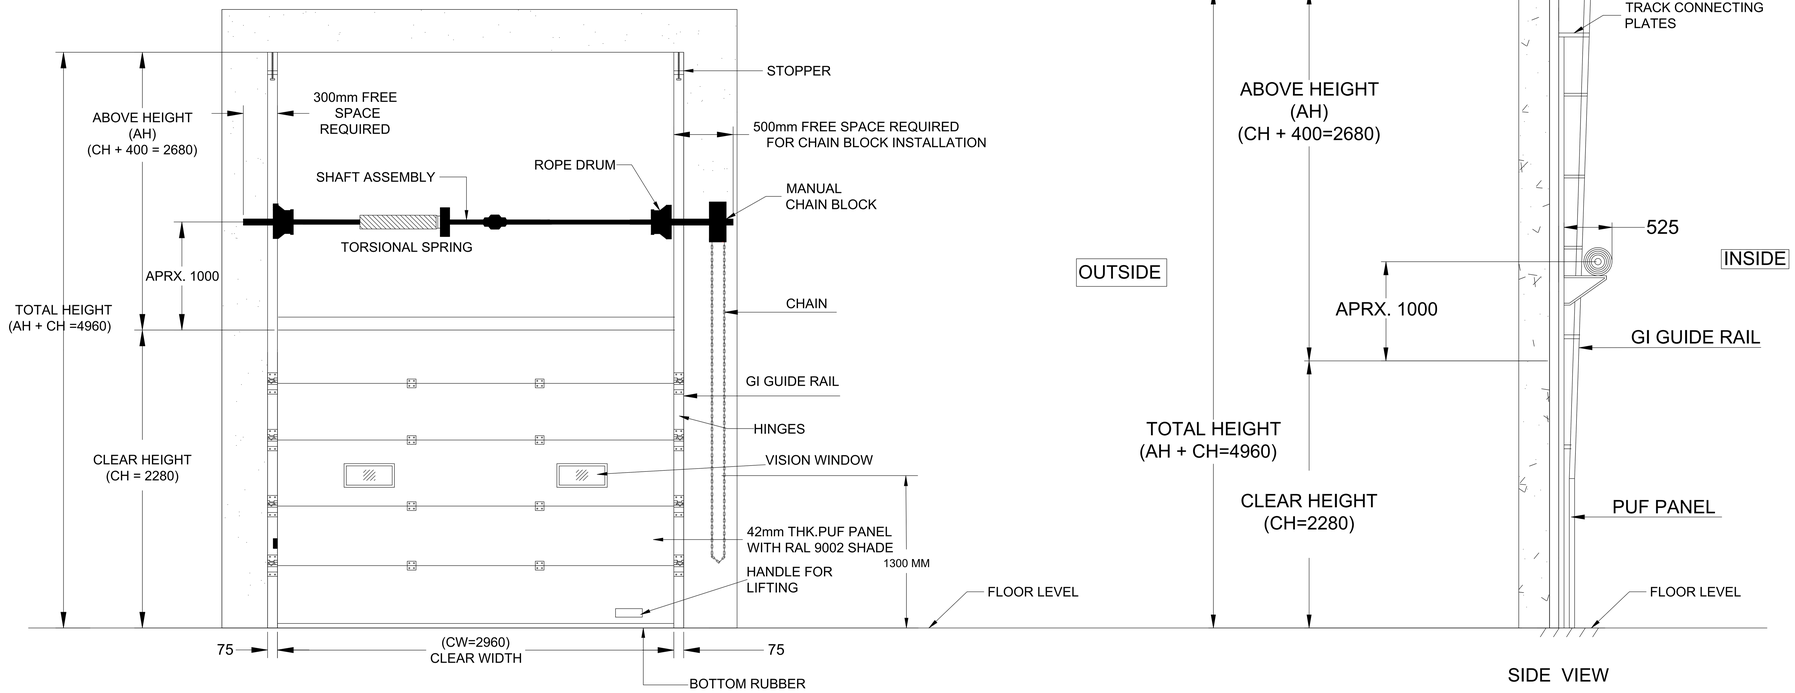



INSIDE ELEVATION

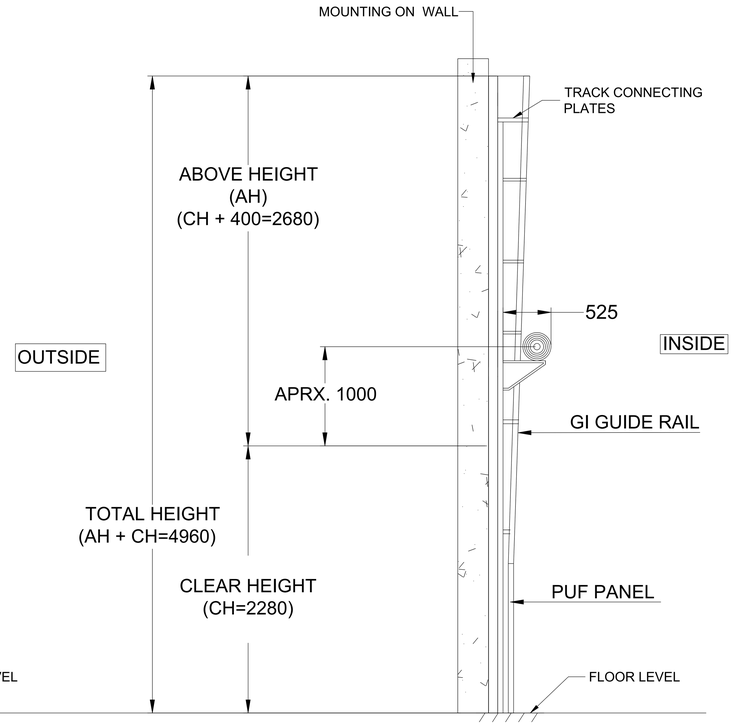

SIDE VIEW

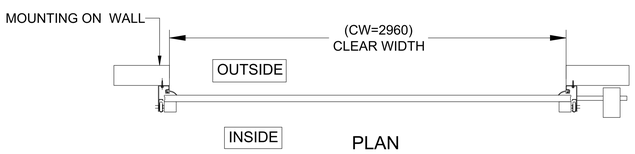

PLAN

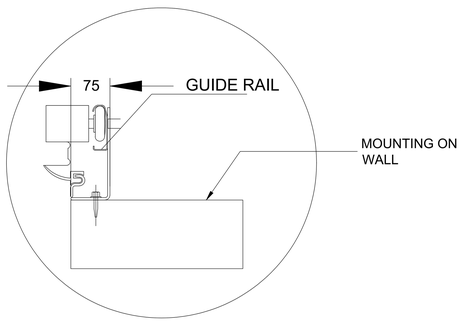

TRACK DETAILS

DIMENSION :

CLEAR WIDTH (CW)	CLEAR HEIGHT (CH)	QUANTITY
2960mm	2280 mm	01 NOS

TECHNICAL DATA :

COMPONENTS	MATERIALS	SPECIFICATIONS
DOOR PANELS	GI & PUF	42mm CFC- FREE POLYURETHANE WITH 0.5mm THK, GI PRECOATED PANELS.
DOOR HINGE	———	HEAVY DUTY HINGES FOR INTERLOCKING OF PANELS
SHAFT ASSEMBLY	STD.	TORSIONAL SPRING WITH SHAFT & BEARING PLATES
FINISH		PANELS WILL BE COLORED IN STANDARD RAL 9002

ACCESSORIES-

1. MANUAL CHAIN.
2. TWO WINDOWS.

IMPORTANT NOTES:

1. ALL CIVIL WORK SHALL BE AT CLIENT'S SCOPE.
2. All dimension are in MM
3. REQUIRED STRUCTURE FOR DOOR IS IN CLIENT'S SCOPE.

NIHVA TECHNOLOGIES PVT. LTD.

NIHVA TECHNOLOGIES PVT. LTD. PUNE
Email:- info@nihva.com
Website:- www.nihva.com

TITLE:

MANUAL VERTICAL SECTIONAL DOOR - VL

CLIENT'S APPROVAL :

CLIENT - T.E CONNECTIVITY

PROJECT -VERTICAL SECTIONAL DOOR

SITE LOCATION -SHIRWAL

DWG. NO. : NIHVA/24-25/XX00

SCALE: NTS	WT:	SHEET:1 OF 1	REV- 0

	NAME	DATE	SIGN
DRAWN	S.J.	30-09-2024	
CHECK	S.M.	30-09-2024	
APPROVAL	V.T.	30-09-2024	

If any queries contact : design1@nihva.com

NOTE: ALL DIMENSIONS ARE IN mm

THIS DRAWING & DESIGNING IS THE PROPERTY OF NIHVA TECHNOLOGIES. NOT TO BE SOLD OR COPIED TO ANY OTHER CONCERN.