
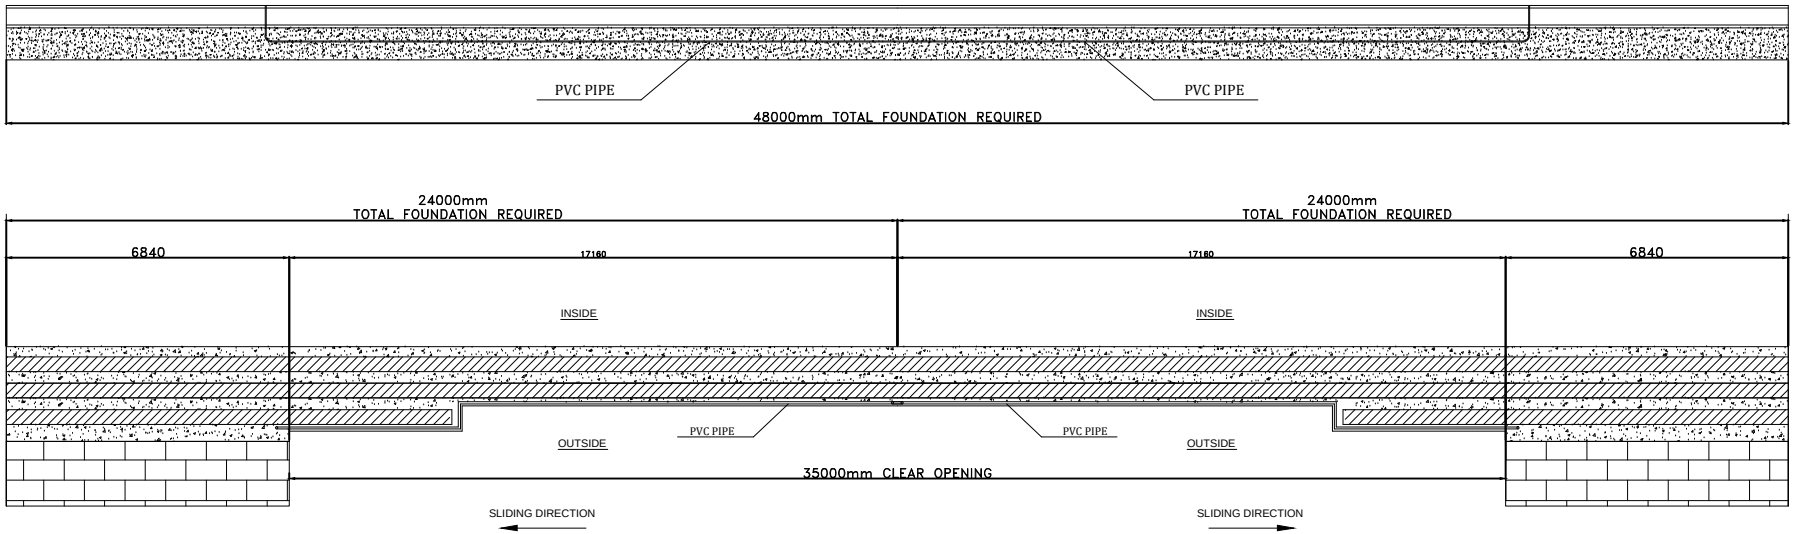


35m TELESCOPIC GATE FOUNDATION

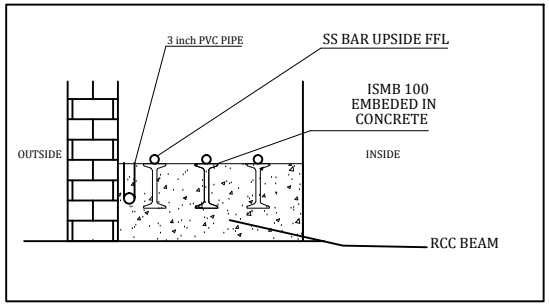

This drawing & designing is the property of NIHVA TECHNOLOGIES. Not be sold or copy to any other concern.

TITLE: MOTORIZED TELESCOPIC SLIDING GATE FOUNDATION DRAWING			
	NAME	SIGN	DATE
DRAWN	SURAJ		24.08.2018
CHECK	P.A		24.08.2018
APPROVAL	R.D		24.08.2018
If any queries contact : design@nihva.com			
ALL DIMENSION ARE IN mm			

NIHVA TECHNOLOGIES PVT. LTD.
NIHVA TECHNOLOGY PVT. LTD. PUNE
Tel : 020 66304033
Website:- www.nihva.com
Email:- info@nihva.com

CLIENT - IDAMAR
PROJECT -
SITE - NAGPUR
DWG. NO. : NIHVA/18-19/0113 | REV. : 0
SCALE: NTS | WT: | SHEET: