

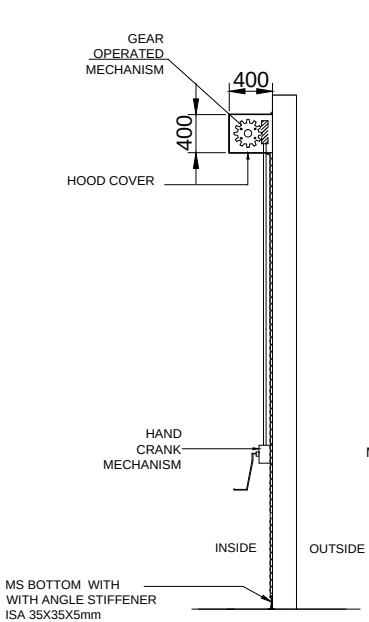



SIDE VIEW

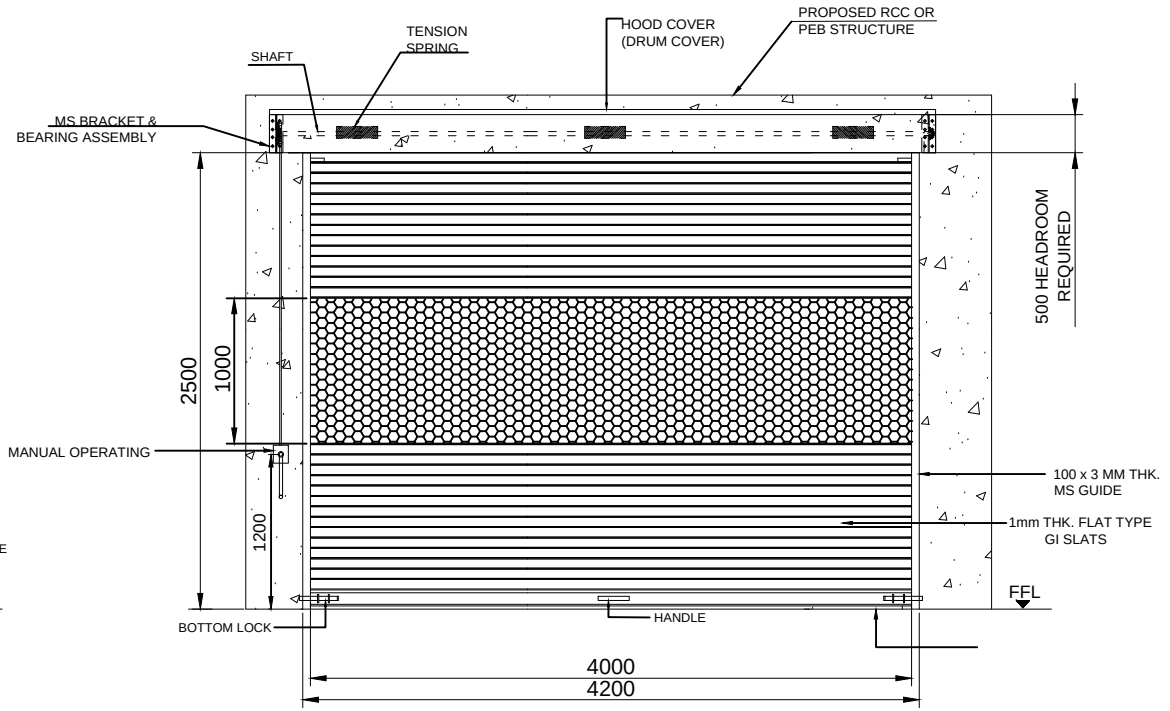


INSIDE ELEVATION

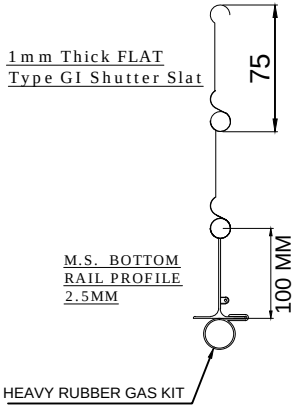


M.S. BOTTOM RAIL PROFILE 2.5MM

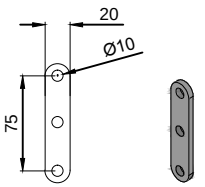


MS BOTTOM WITH ANGLE STIFFNER WITH RUBBER SAFTEY EDGE

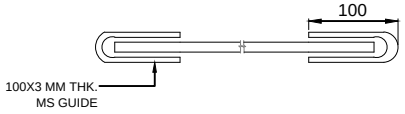

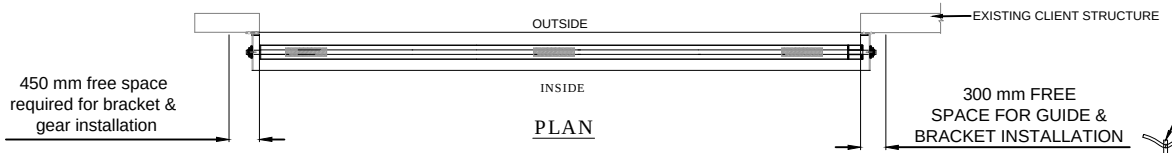

PLAN

5 mm THK. LINK

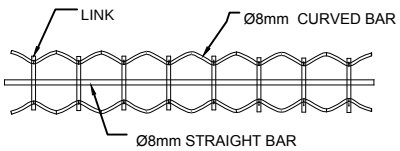

S.NO	FEATURE	EQUIPMENT DETAILS
01	SLATS MODEL	GALVANISE STEEL(GI) SLATS 1mm THK.
02	GUIDE RAIL	100 X 3mm THK MILD STEEL(MS).
03	BOTTOM RAIL	2.5mm THK MILD STEEL (M.S.).
04	HOOD COVER	0.9mm THK GALVANISE STEEL (GI).
05	RAL COLOR	RAL 9002 (WHITE GRAY)
06	NO OF SLATS	28 NOS

SR.NO.	SIZE	QUANTITY
01	4000(W)X2500(H)	01 NO

SHUTTER LOCATION :- R.M.U 2

TOLERANCE - ±10mm

NOTE-
1. ALL REQ. CIVIL WORK & M.S STRUCTURE WILL BE IN CLIENT'S SCOPE.

This drawing & design is the property of NIHVA TECHNOLOGIES. Not to be sold or copied to any other concern.

TITLE
GEAR OPERATED ROLLING SHUTTER

NIHVA TECHNOLOGIES PVT. LTD.

NIHVA TECHNOLOGIES PVT. LTD. PUNE
Tel : 020 66304033
Website:- www.nihva.com
Email:- info@nihva.com

	NAME	SIGN	DATE
DRAWN	P.A		12.02.2019
CHECK	P.A		12.02.2019
APPRD.	V.T		12.02.2019

CLIENT -
PROJECT-
SITE LOCATION -
If any queries contact : design@nihva.com
DWG. NO. : NIHVA/18-19/VDR/378
REV- 00
ALL DIMENSION ARE IN mm
SCALE: NTS
WT:
SHEET: 01 OF 01