

NOTE :
1. DOOR HINGES : GEZE MAKE.
2. DOOR CLOSER : GEZE MAKE.
3. DOOR PANIC BAR : YELE MAKE.

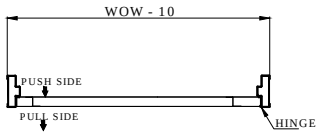

TOP VIEW

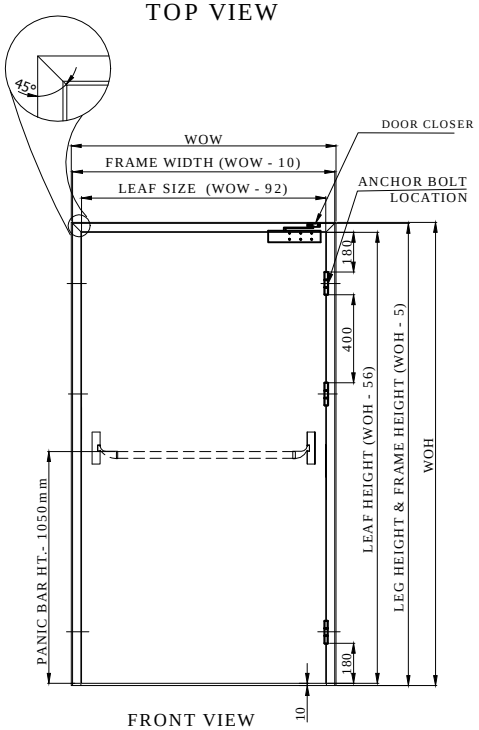


FRONT VIEW





SIDE VIEW
SECTION A-A'

SINGLE GLAZE FIXING DETAIL

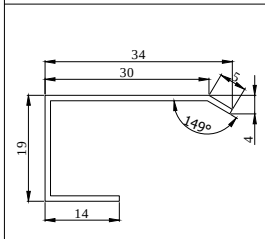


SEE DETAIL 'C'

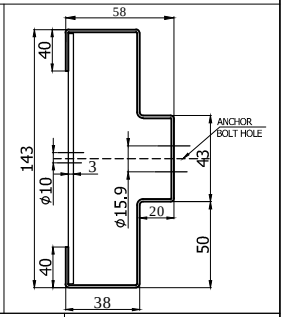

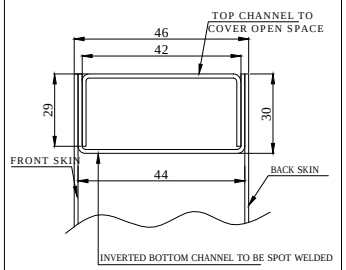

DOOR TOP SECTION DETAIL

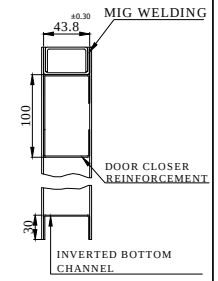

DOOR BOTTOM & TOP DETAIL

SR. NO	WALL OPENING WIDTH	WALL OPENING HEIGHT	QTY	RAL	LOCATION	HARDWARE
01	1200	2100	01	3020	A-Block North Side Mezzanine Exit Door (GD2)	Hinges , Door closer , Single point panic bar.

TOLERANCE - ±05mm

This drawing & design is the property of NIHVA TECHNOLOGIES. Not to be sold or copied to any other concern.

TITLE	NAME	SIGN	DATE
SINGLE LEAF STEEL DOOR			
DRAWN	P.V.A		26.03.2019
CHECK	V.M.T		26.03.2019
APPRD.			

NIHVA TECHNOLOGIES PVT. LTD.

NIHVA TECHNOLOGIES PVT. PUNE
Tel : 020 66304033
Email:- info@nihva.com
Website:- www.nihva.com

CLIENT -
PROJECT -
SITE LOCATION -

If any queries contact : design@nihva.com
DWG. NO. : NIHVA/18-19/VDR/427
REV- R00
ALL DIMENSION ARE IN mm
SCALE: NTS
WT:
SHEET: 01 OF 01