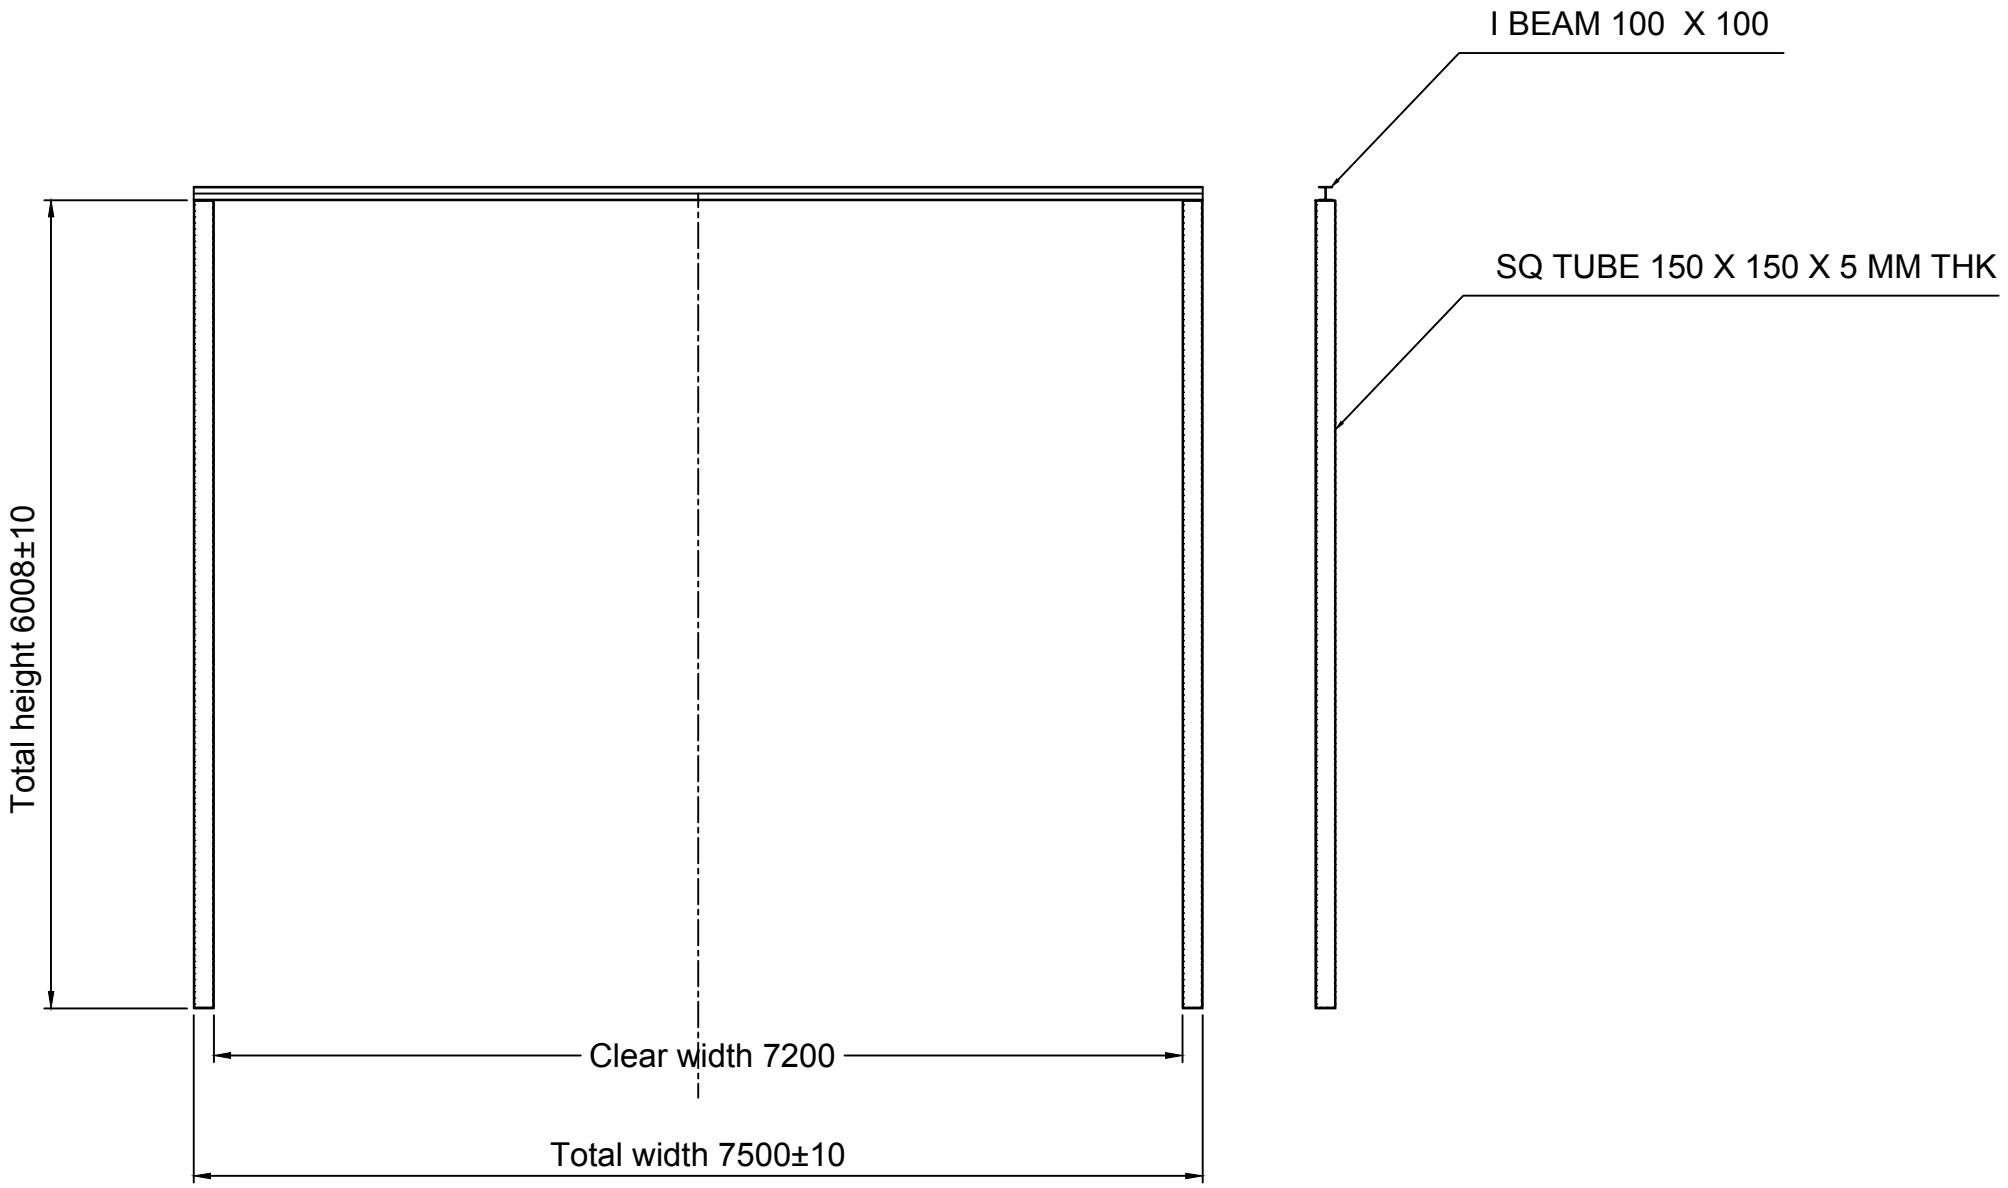


Date	Revised By

TITLE:- STRUCTURE

NIHVA TECHNOLOGIES PVT. LTD.

NIHVA TECHNOLOGIES PVT. LTD. PUNE
Tel : 020 66304033
Email:- info@nihva.com
Website:- www.nihva.com

	NAME	DATE	SIGN
DRAWN	KISHAN	19/05/2022	
CHECK	P. JAIN	19/05/2022	
APPRD.	V. TARAK	19/05/2022	

If any queries contact : design@nihva.com

ALL DIMENSION ARE IN mm

CLIENT - POSCO STEEL

LOCATION - MANGAON

PRODUCT - VERTICAL FABRIC DOOR

DWG NO:-NIHVA/22-23/CLT/0043 | REV- 0

SCALE: NTS | SCALE:-- 1:1 | SHEET: 01 OF 01