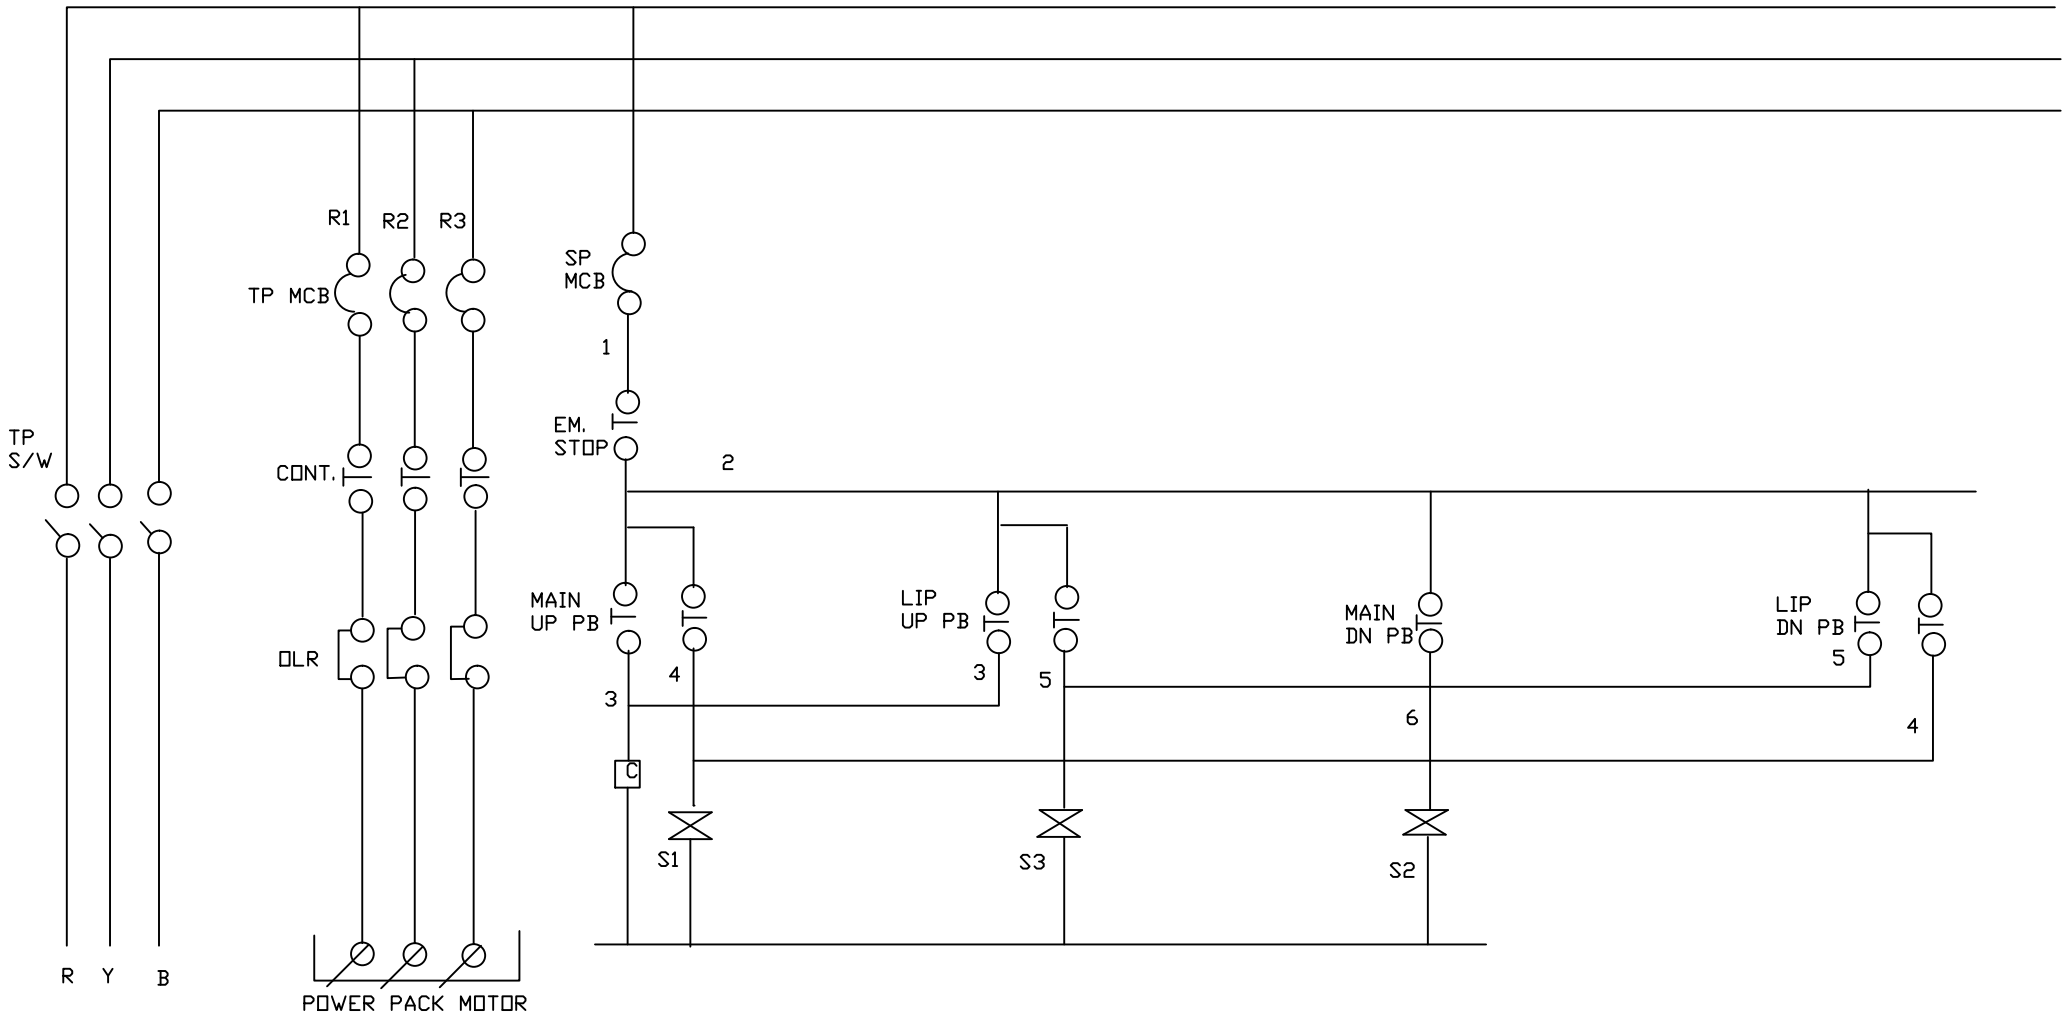

LOGIG AUTOMATION&CONTROLS
SECTOR NO 1: PLOT NO F40,
PRATHAMESH PARK,
INDRAYANI NAGAR,
BHOSARI,
PUNE-411039.
MOBILE: 9822977625
e-mail : dharamalogic75@yahoo.com

DWG TITLE		DRAWING NO.		SHEET NO	
APPLICATION		DATE		DRAWN BY	
PROJECT		REVISON		CHKD.BY	
CLIENT		SCALE	NO SCALE	APPD.BY	