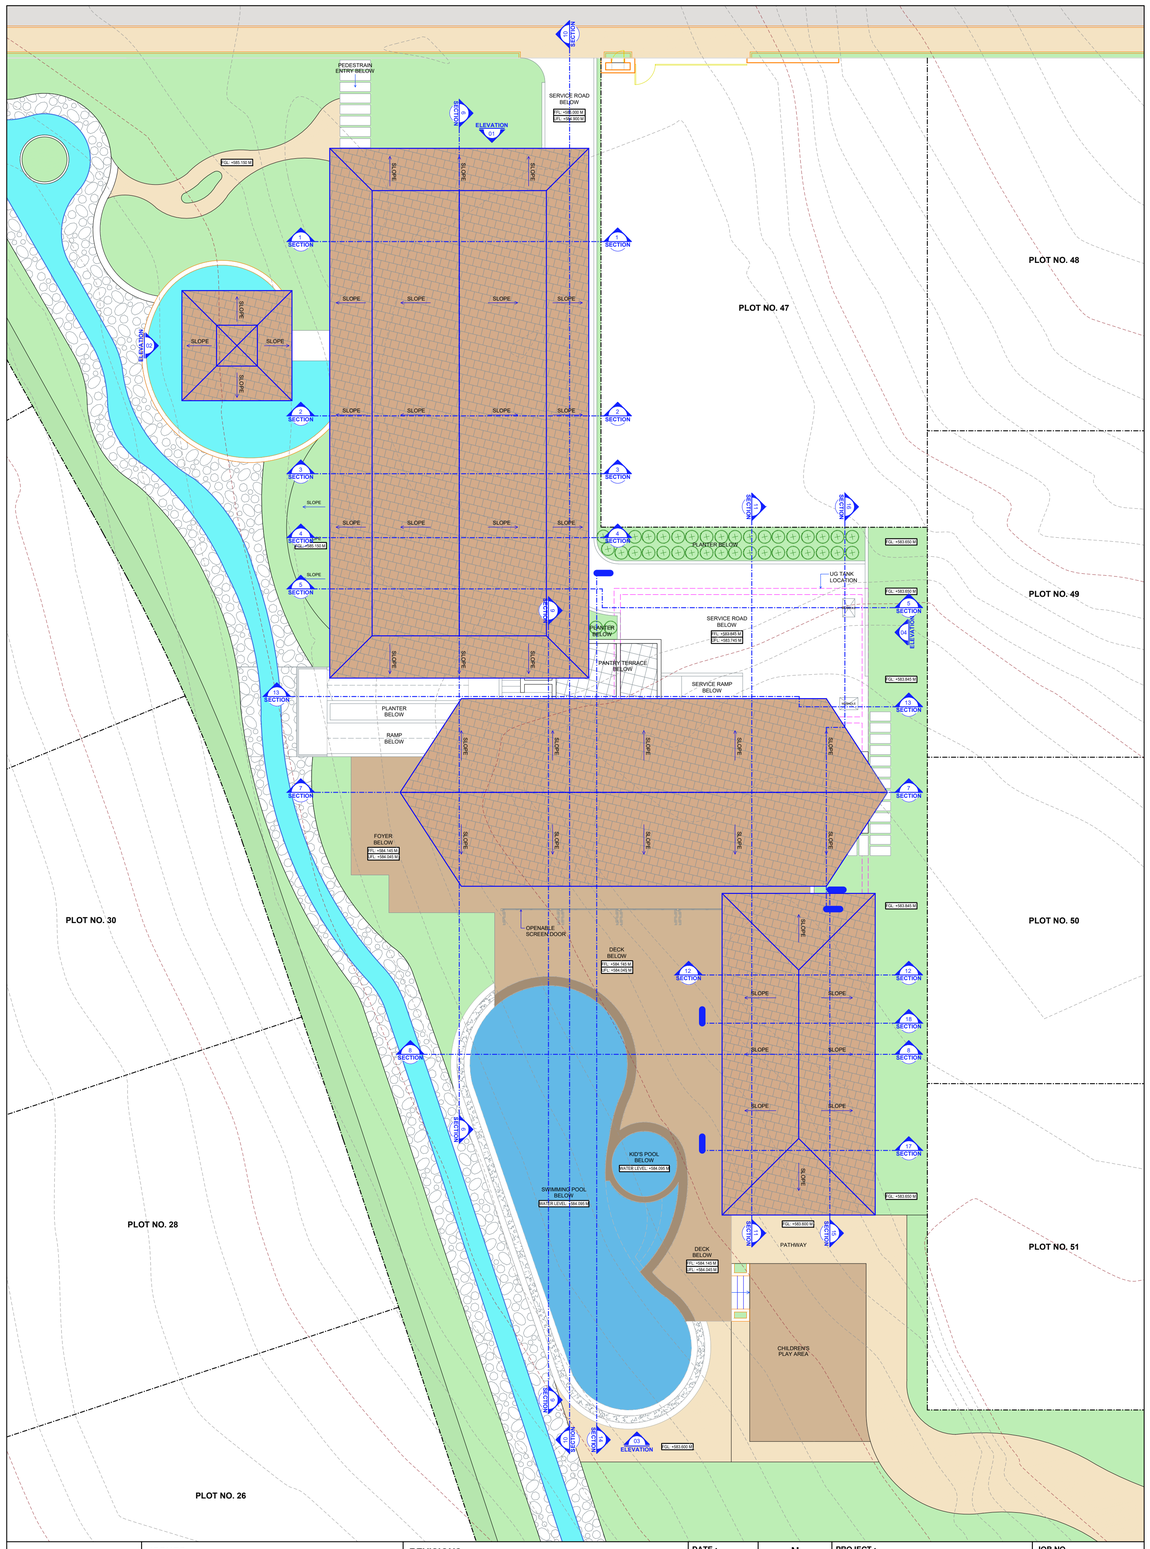


ISSUES					
SITE	RCC	LANDSCAPE	INTERIOR	SERVICES	

REVISIONS				
REV. NO.	DATE	DESCRIPTION	DRN BY	CHKD BY

DATE : 19-03-25

DEALT : PD

DRAWN BY : SB

N

SCALE : 1:100

PROJECT : BOUGAIN VILLA, LOHEGAON, PUNE

DRAWING TITLE : CLUBHOUSE - ROOF PLAN

JOB NO. PAN - 2332

DRAWING NO. XXXX

REVISION NO. XXXX

THINKBIG REALTY
Pune: Tech Park One, Tower "S", 101 Yerwada, Pune 411 006