


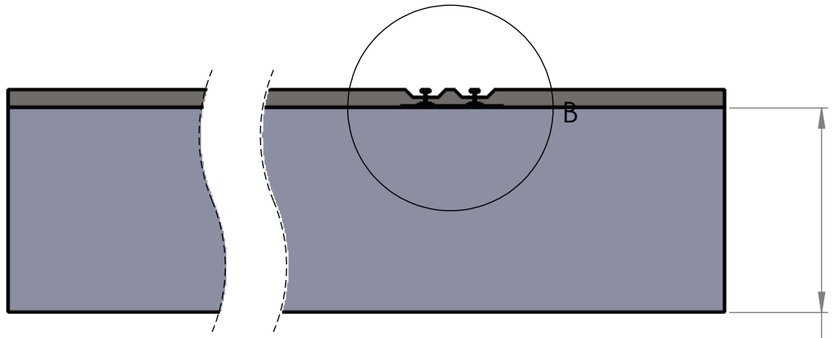


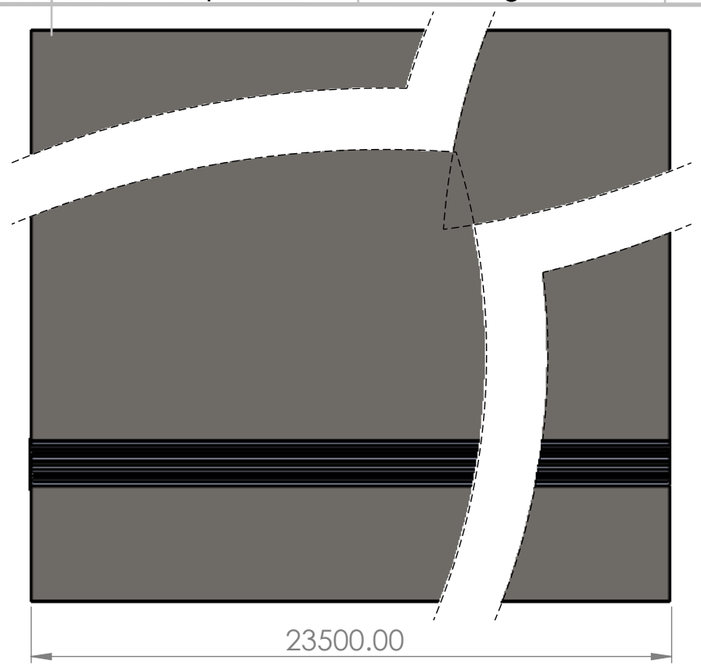

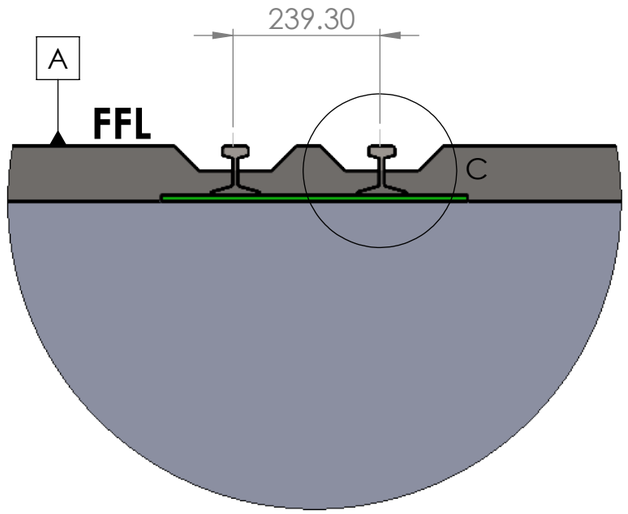

DETAIL B
SCALE 1 : 10

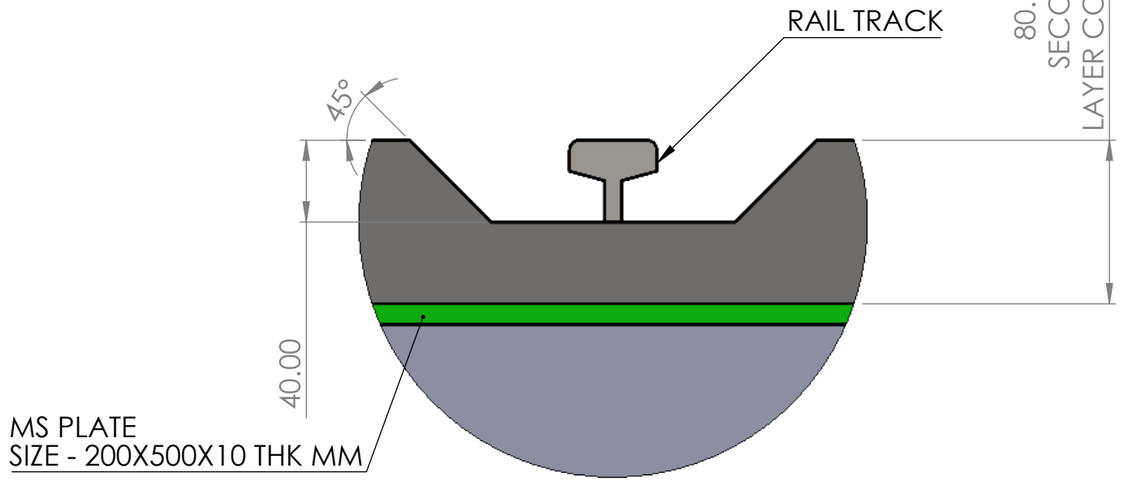

DETAIL C
SCALE 1 : 10

NOTE -

1) CREATE 1000 MM CONCRETE LAYER. --- (CLIENT SCOPE)
2) ABOVE CONCRETE PUT MS PLATE. ----- (CLIENT SCOPE)
3) ABOVE MS PLATE WELD THE RAIL TRACK AS PER DRAWING.---- (CLIENT SCOPE)
   (RAIL TRACK IS PROVIDED BY NIHVA).
4) AFTER RAIL TRACK WELDING THEN SECOND LAYER OF
   CONCRETE IS CREATED AS PER DRAWING.----- (CLIENT SCOPE)

TITLE : FOUNDATION DRAWING

NIHVA TECHNOLOGIES PVT LTD

	NAME	SIGNATURE	DATE
DRAWN	SURAJ.W		17-03-2025
CHK'D	SURAJ.W		17-03-2025
APPV'D	VIJAY T.		17-03-2025

CLIENT NAME : SURAJ BUILDCON ,AMARAVATI

PRODUCT NAME : TELESCOPIC HANGER SLIDING DOOR

SITE LOCATION : AMARAVATI,MH

DWG NO. FOUNDATION DRAWING — A3

REVISION : 0

DIMENSIONS ARE IN MILLIMETERS

SCALE:

SHEET 1 OF 1