




DRAWING

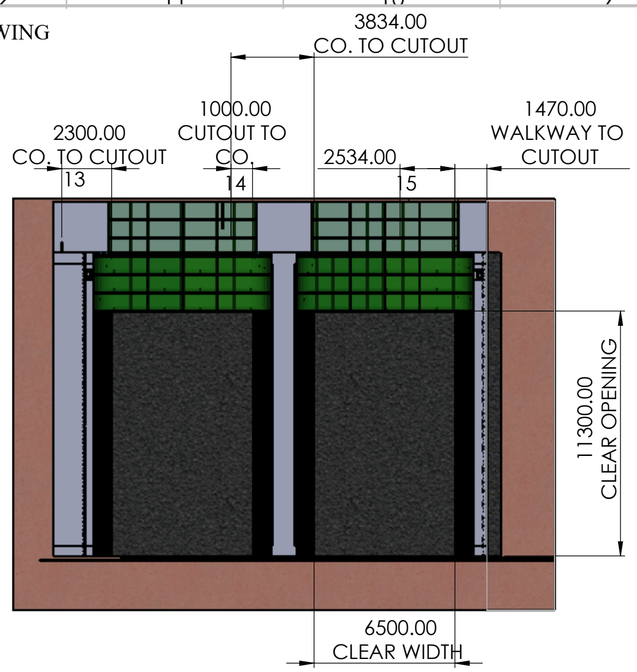

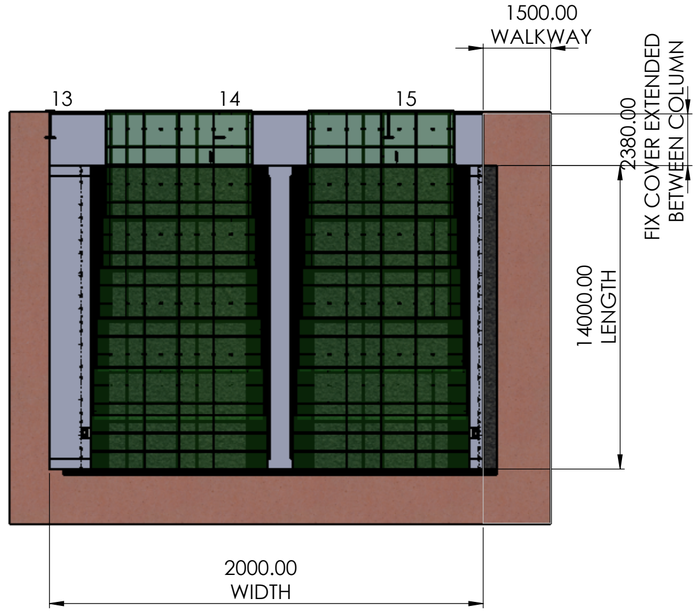


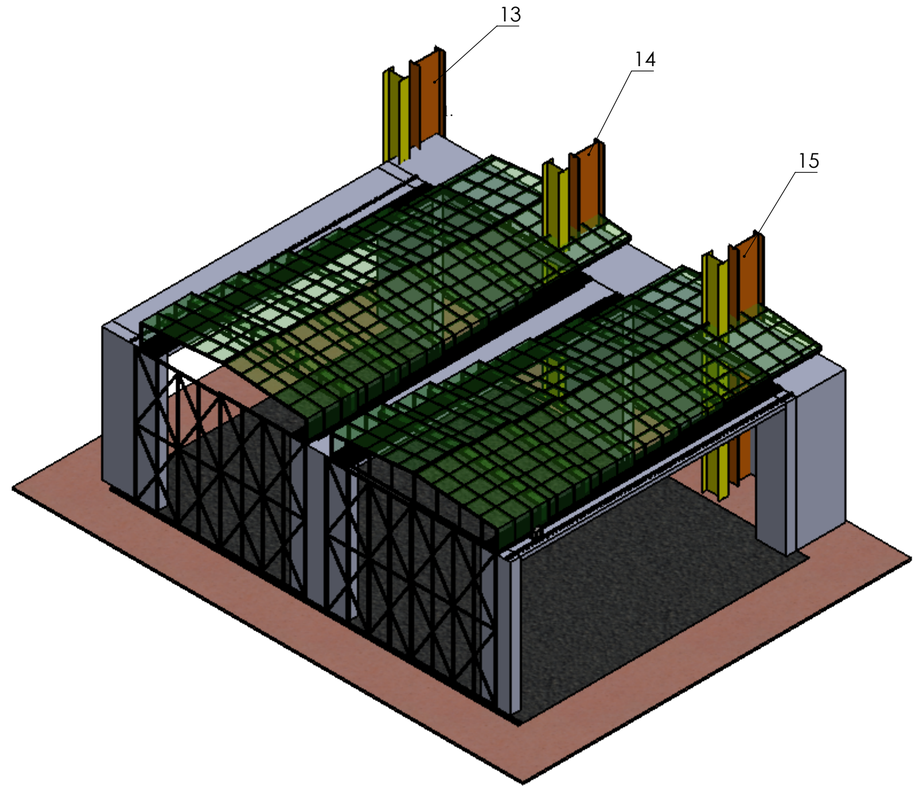

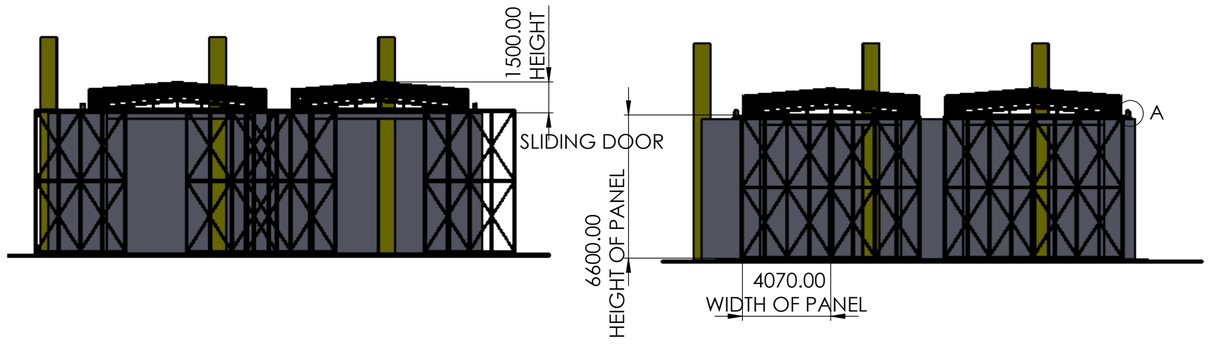

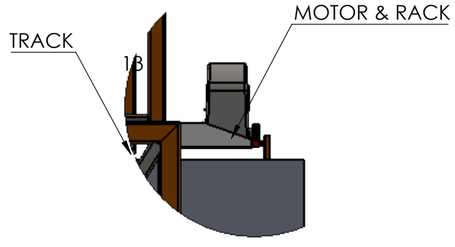

DETAIL A
SCALE 1 : 20

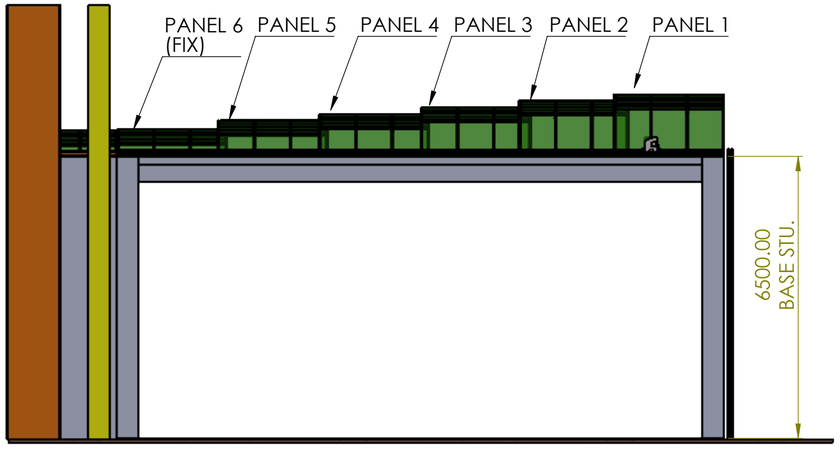

REV DESCRIPTION	DATE	REV NO
	05-06-2026	REV 00

NOTE :

1. These Drawinf only for client approval.
2. Civil Stu. is in client scope.

SPECIAL INSTRUCTION'S :

TITLE - ROOF AUTOMATION				NIHVA TECHNOLOGIES PVT.LTD.PUNE Website - www.nihva.com
DWG NO - NTPL-000-PM-001-00-00-00				
	NAME	SIGNATURE	DATE	PRODUCT - RETRACTABLE ROOF
DRAWN	J.P.		04-06-2026	PROJECT NO - NTPL-000-PM / REVISION - 00
CHK'D	B.S.		05-06-2026	SITE LOCATION - HYDERABAD
APPV'D	V.T.		05-06-2026	MATRIAL - / QTY - 1
If any queries contact - Design@nihva.com				PROJECTION METHOD: / SCALE :
ALL DIMENSION ARE IN mm		A2		SHEET 1 OF 1