
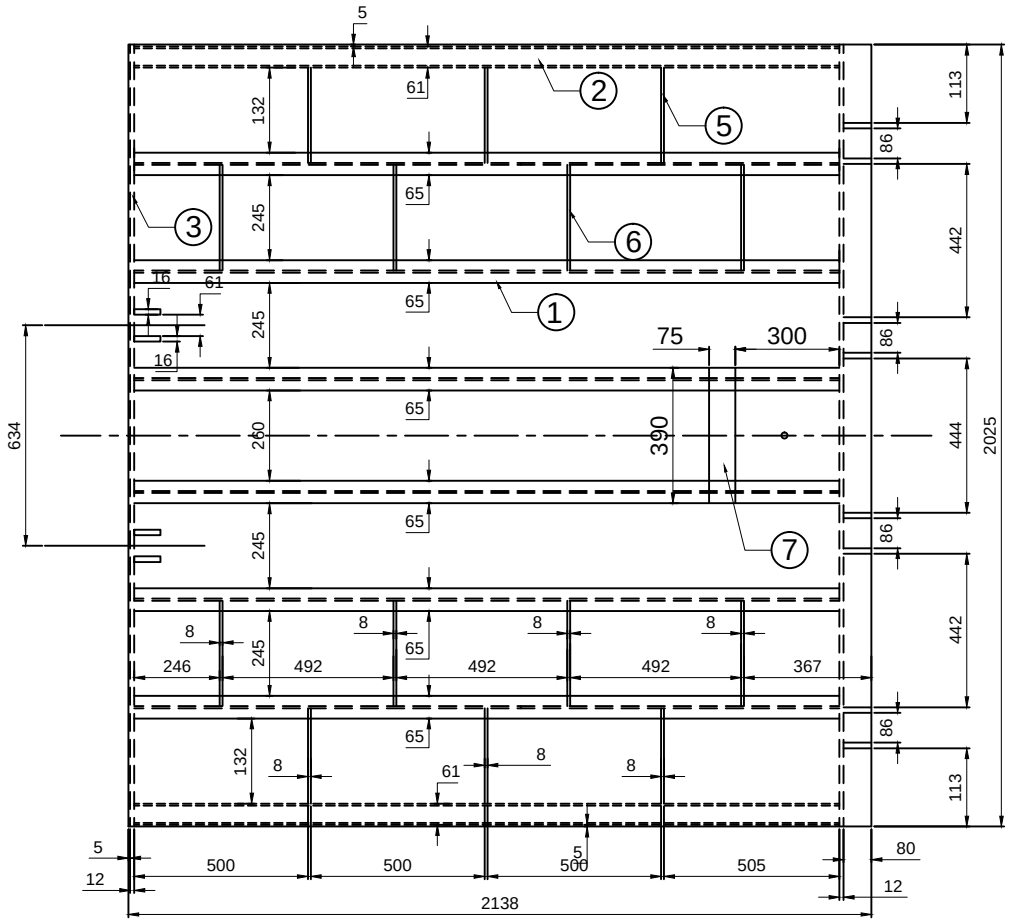


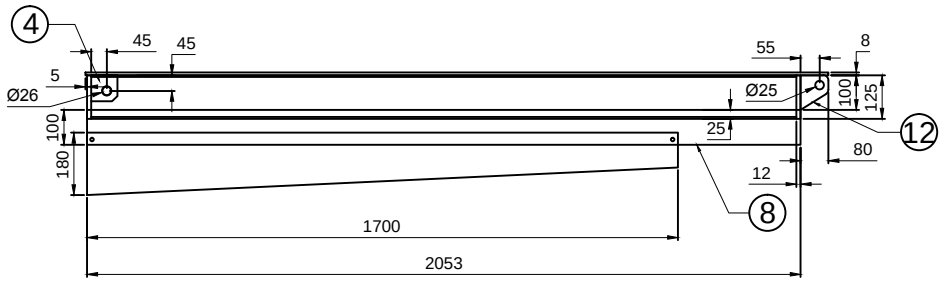

NOTE:~ MTL : MS

PART NO.	PART NAME	DESCRIPTION	QTY
1.	ISMB	125 X 65 X 2030L	6 NOS
2.	R.TUBE	122 X 61 X 5.4THK X 2030L	2 NOS
3.	FLAT	125 X 12 X 2250L	2 NOS
4.	FLAT	75 X 16 X 75L	4 NOS
5.	FLAT	125 X 8 X 162L	6 NOS
6.	FLAT	150 X 8 X 302L	8 NOS
7.	FLAT	75 X 6 X 380L	1 NOS
8.	PLATE	100 X 3THK X 2050L	2 NOS
9.	SIDE COVER	180 X 3THK X 1700L	2 NOS
10.	LIP STOPER	Ø20 X 50L	4 NOS
11.	CHEQ.SHEET	2138 X 8 THK X 2025L	1 NO
12.	FLAT	100 X 16 X 80L	8 NOS
13.	EYE BOLT	M16 X STD WITH NUT	3 NOS

This drawing & design is the property of NIHVA TECHNOLOGIES. Not to be sold or copied to any other concern.

TITLE

DECK ASSLY

NIHVA TECHNOLOGIES PVT. LTD.

NIHVA TECHNOLOGIES PVT. LTD. PUNE
Tel : 020 66304033
Email:- info@nihva.com
Website:- www.nihva.com

	NAME	SIGN	DATE
DRAWN	PRADEEP		05.09.2018
CHECK	PRADEEP		05.09.2018
APPRD.	PRADEEP		05.09.2018

If any queries contact : design@nihva.com

ALL DIMENSION ARE IN mm

CLIENT -

PROJECT - DLSD1010

SITE LOCATION -

DWG. NO. : NIHVA/18-19/MFG/DLSD1010/001

SCALE: NTS | WT: | REV- 00