

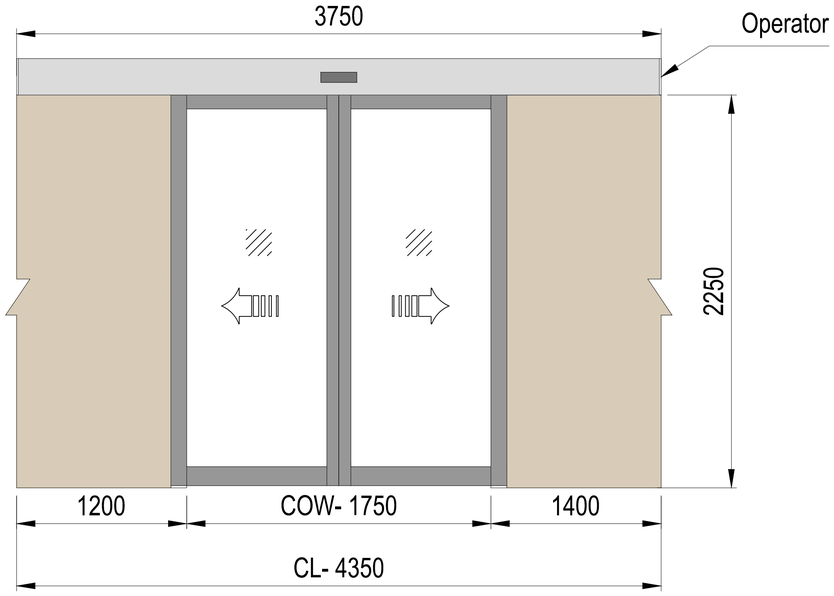



Inside Elevation

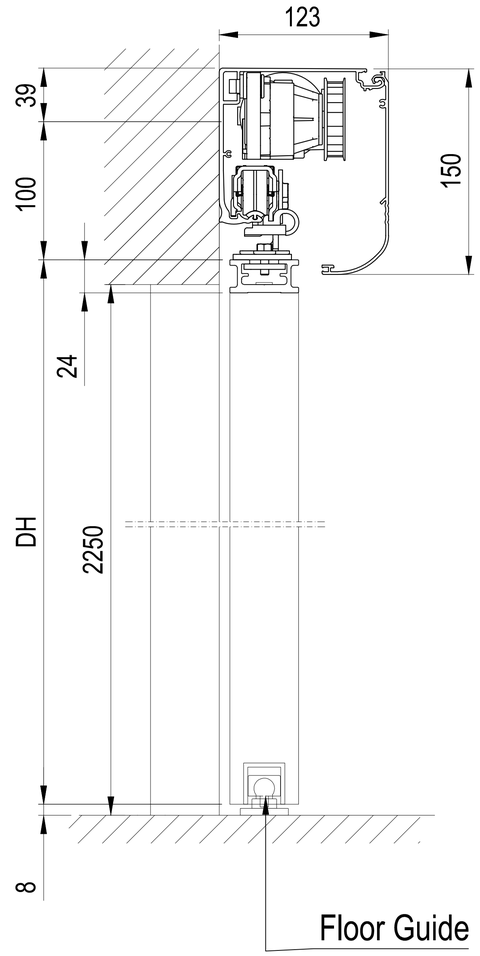

Fixing Plan

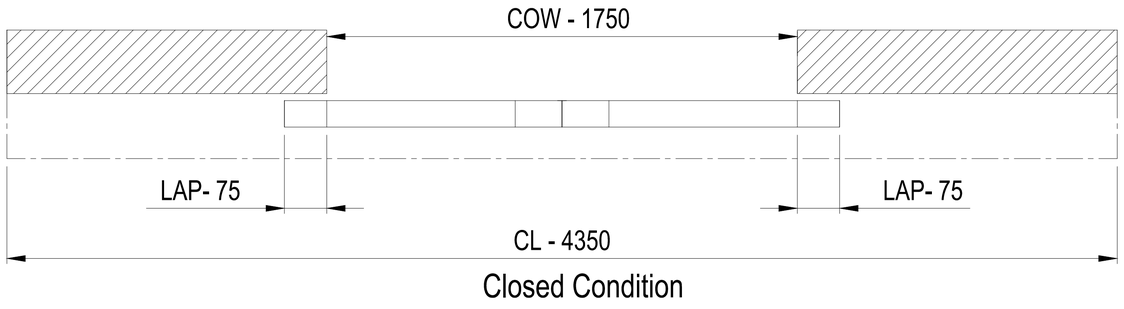

Closed Condition

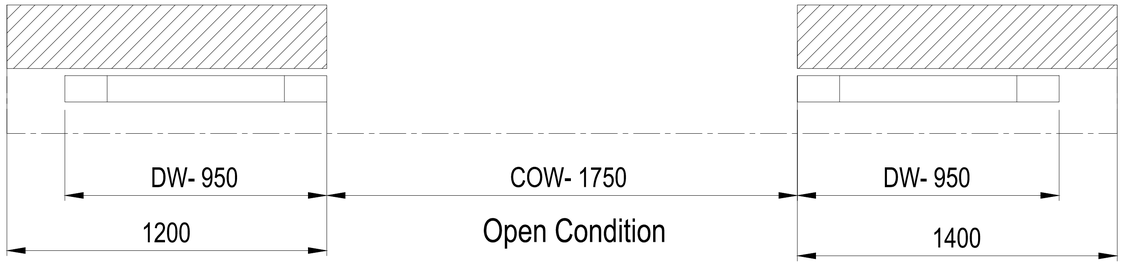

Open Condition

Plan



Fixing Plan

Door Size

Sr. No.	Clear Width	Clear Height	Quantity
1	1750	2250	1

Glass Type- 10mm Toughened

This drawing & designing is the property of NIHVA TECHNOLOGIES. Not to be sold or copied to any other concern.

TITLE	AUTOMATIC SLIDING FRAMED GLASS DOOR		NIHVA TECHNOLOGIES PVT. LTD. PUNE Tel : 020 66304033 Email:- info@nihva.com Website:- www.nihva.com
	SIGN	DATE	
DRAWN	OMKAR	03/07/17	CLIENT - VIJAY LOGISTICS
CHECK	S.S.	03/07/17	PROJECT -
REV.	00		SITE - CHAKAN
APPROVAL			DWG. NO. : NIHVA/17-18/0121
If any queries contact : projects@nihva.com			SCALE: NTS / WT: / SHEET: 01 OF 01
ALL DIMENSION ARE IN mm			