

VERTICAL CROSS SECTION OF 4 LEAF SINGLE SLIDE DOOR

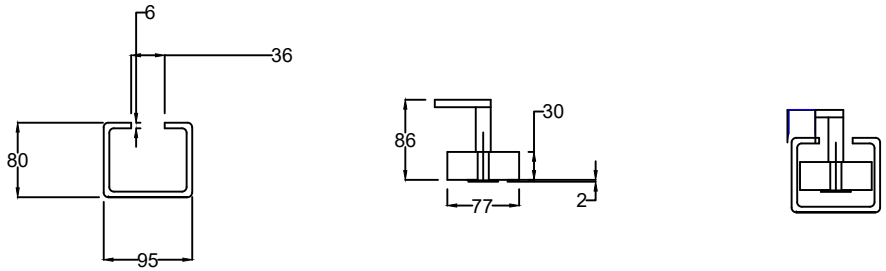

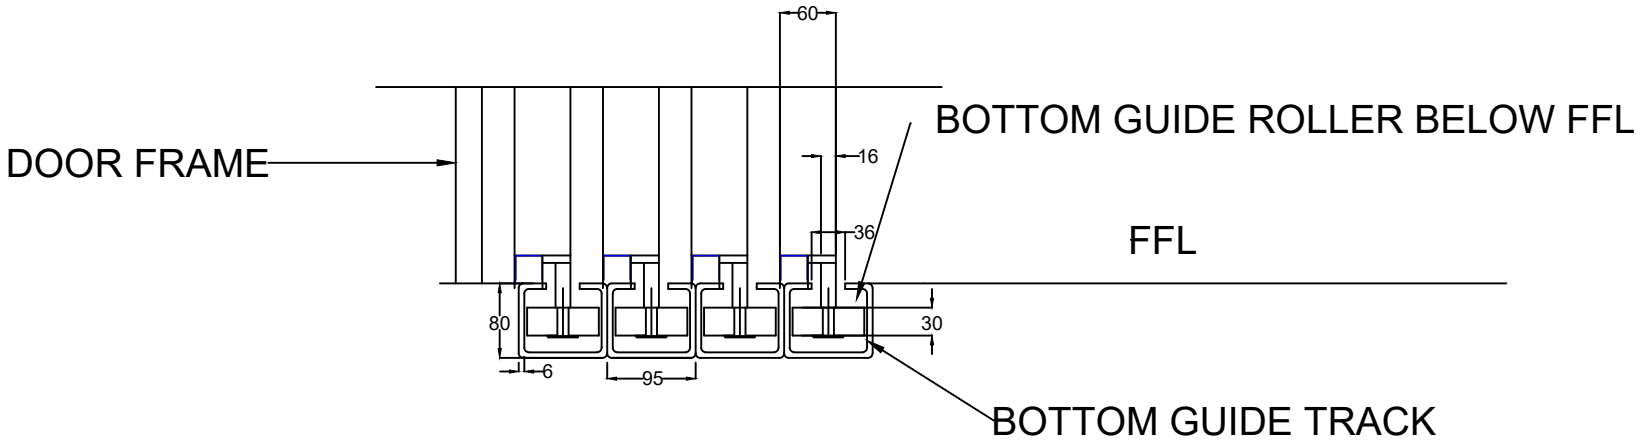

Note:--

1.All dimension are in MM

2.All Civil work will be in client scope

This drawing & design is the property of NIHVA TECHNOLOGIES. Not to be sold or copied to any other concern.

Rev No.	Revision	Date	Revised By

TITLE:- 4 LEAF RIGHT SIDE CRM DOOR 01

NIHVA TECHNOLOGIES PVT. LTD.

NIHVA TECHNOLOGIES PVT. LTD. PUNE
Tel : 020 66304033
Email:- info@nihva.com
Website:- www.nihva.com

	NAME	DATE	SIGN
DRAWN	SUJATA		
CHECK			
APPRD.			

CLIENT -

LOCATION -

PRODUCT - SLIDING DOOR

If any queries contact : design@nihva.com

DWG NO:-NIHVA/21-22/ REV- 0

ALL DIMENSION ARE IN mm

SCALE: NTS SCALE:-- 1:1 SHEET: 01 OF 01