




SIDE VIEW

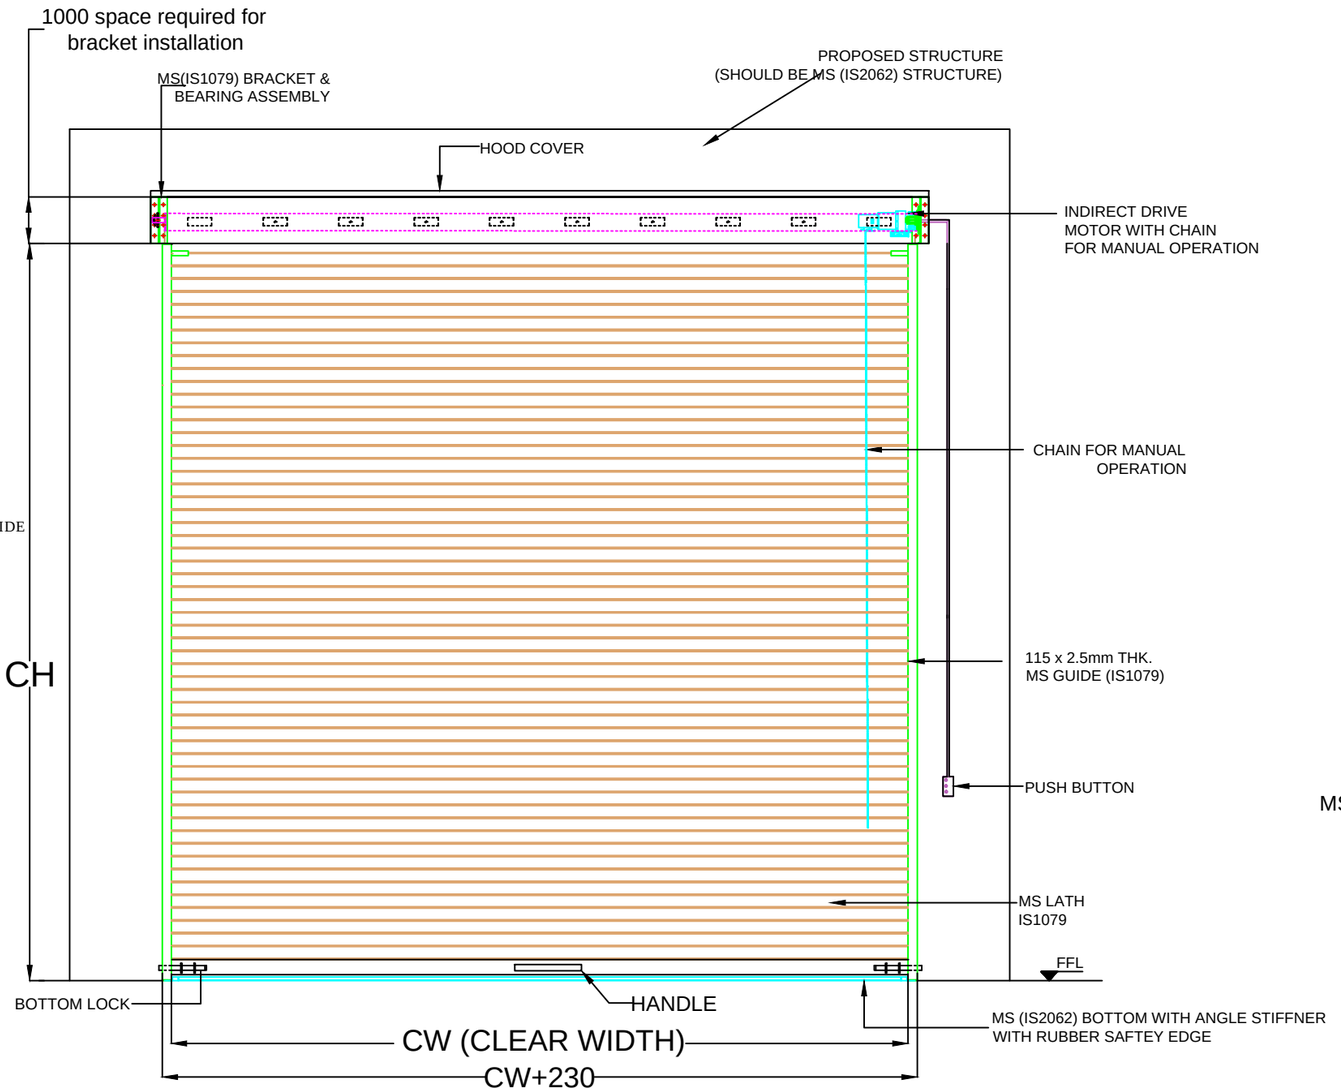

ELEVATION

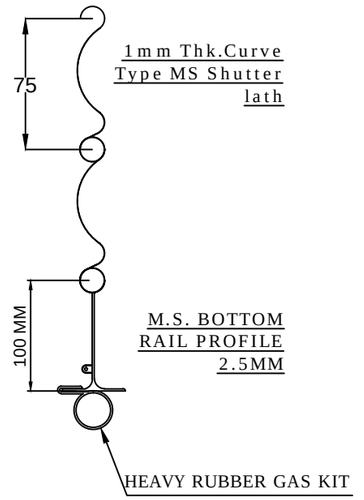


M.S. BOTTOM RAIL PROFILE 2.5MM

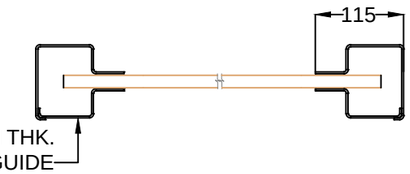

COLOR:- 1.RAL7035(LIGHT GRAY) ☐
2.RAL9016(TRAFFIC WHITE) ☐
3.RAL5005(SIGNAL BLUE) ☐
4.RAL7004(SIGNAL GRAY) ☐
5.RAL5015(SKY BLUE) ☑

CLEAR WIDTH (CW)	CLEAR HEIGHT (CH)	QUANTITY
5000	6000	8

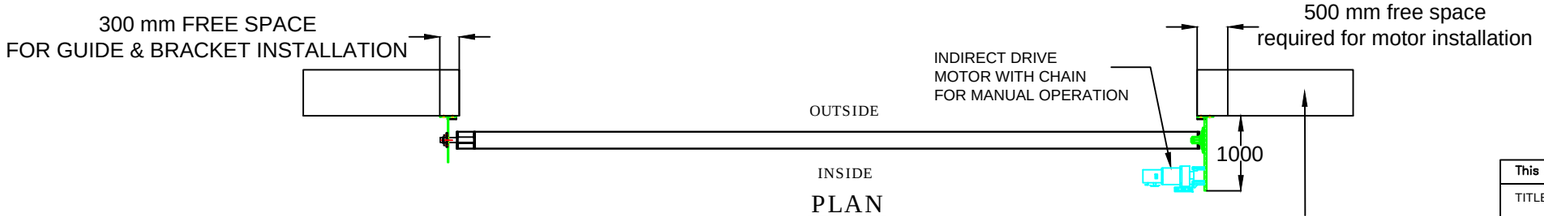

PLAN

Rev 01:- 04/02/2022
1.Added IS material specification for MS material.
2.Added motor capacity details.
3.Mentioned RAL code.
Rev 02:- 11/ 02/ 2022
1.Reduced quantity of shutter.

NOTE:-
1.REQUIRED STRUCTURE FOR ROLLING SHUTTER SHALL BE IN NIHVA SCOPE.
2. ALL REQUIRED CIVIL WORK IN CLIENT SCOPE.
3. 3 PHASE POWER SUPPLY SHOULD BE PROVIDED BY CLIENT.
4. MOTOR : JIELONG , 1 TON, 3PH

This drawing & designing is the property of NIHVA TECHNOLOGIES. Not to be sold or copied to any other concern.

TITLE: MOTORIZED ROLLING SHUTTER

	NAME	SIGN	DATE
DRAWN	G.P.		13/09/21
CHECK	A.K.		13/09/21
APPROVAL	V.T.		13/09/21

NIHVA TECHNOLOGIES PVT. LTD. PUNE
Tel : 020 66304033
Email:- info@nihva.com
Website:- www.nihva.com

CLIENT - REWARD CONSTRUCTION
PROJECT -
SITE - INDAPUR
DWG. NO. : NIHVA/21-22/0232 | REV. - 02
If any queries contact : design@nihva.com
ALL DIMENSION ARE IN mm | SCALE: NTS | WT: | SHEET: 01 OF 01