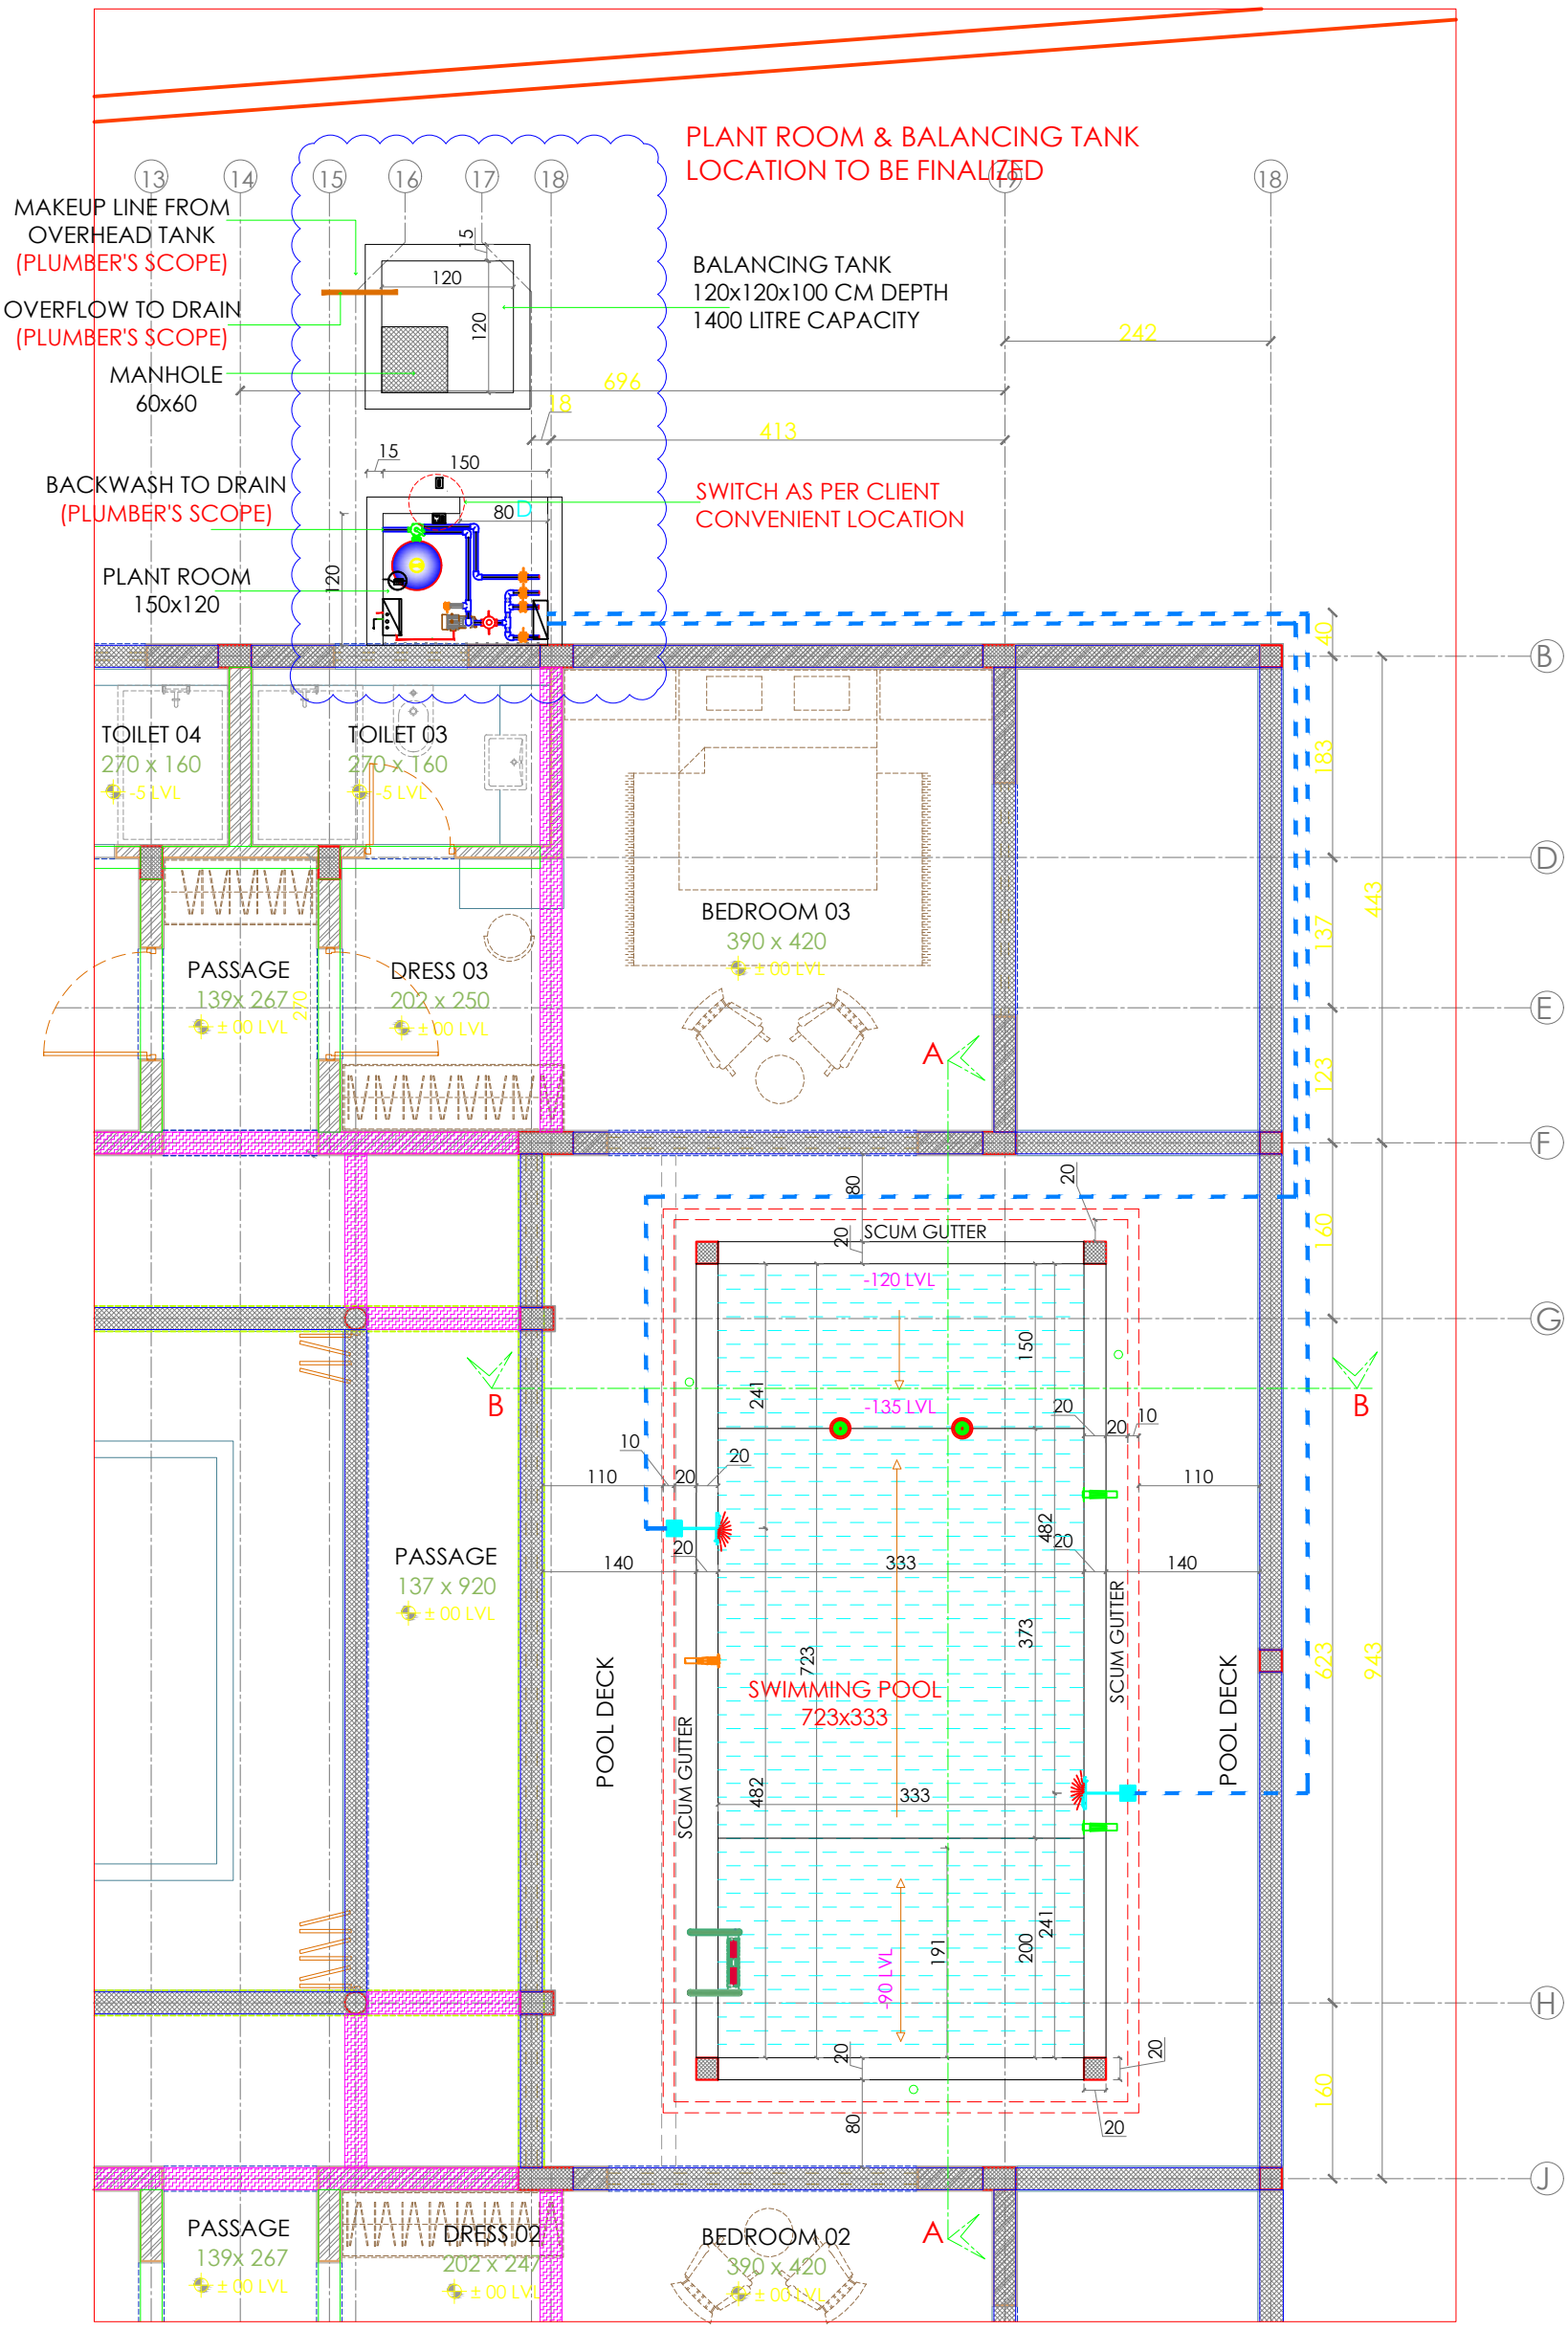


LEGEND	DESCRIPTION	QTY.	LEGEND	DESCRIPTION	QTY.	LEGEND	DESCRIPTION	QTY.
	PLANT ROOM LIGHT	1		LED UNDER WATER LIGHT,7.2 W/ 12V	2			
VF	POWER PLUG & SWITCH	1		DECK BOX	2			
	RE-CIRCULATION PUMP -1 HP	1						
	PRE FILTER IN THERMOPLASTIC IN 2" SIZE	1						
	CONTROL PANEL	1						
N	DRIVE BOX	1						

NOTE:-

ANY DISCREPANCIES IN THE DRAWING SHALL BE BROUGHT TO THE NOTICE OF THE CONSULTANTS AND CORRECTED BEFORE EXECUTION.

DIMENSIONS SHALL NOT BE MEASURED DIRECTLY FROM THE DRAWING. ALL DIMENSIONS IN CENTIMETER,UNLESS MENTIONED OTHERWISE.

THIS DRAWING IS THE PROPERTY OF M/s. SANWE POOLS AND SHOULD NOT BE USED OR REPRODUCED WITHOUT THEIR CONSENT.

REV.	DATE	DESCRIPTION
REV.2	05.02.2022	

☐ CONCEPT ☐ TENDER
☐ APPROVAL ☐ FOR CONSTRUCTION

SCALE: 1:100 SHEET NO: 02

ISSUE DATE	PROJECT NO	DRAWING NO
23-01-2021	000 23012021	SAN 1330
DRAWN BY	CHECKED BY	APPROVED BY
JINSHA	RASHOB	S Raj

Residence Project at Cheruvathur,Kasargode

TITLE :

SWIMMING POOL
OVERFLOW (SCUM GUTTER)

SUB TITLE :

PLAN
ELECTRICAL

CLIENT: Mr.Abdullah. R,Cheruvathur

ARCHITECT:
M/s.Soho Architects,Calicut

Consultant:

Sanwe MEP contracting Pvt Ltd.,
Qatar UAE India
18/1580Q ii Floor, Kethar Tower , Thali Temple Road, Puthiyapalam, Calicut 2