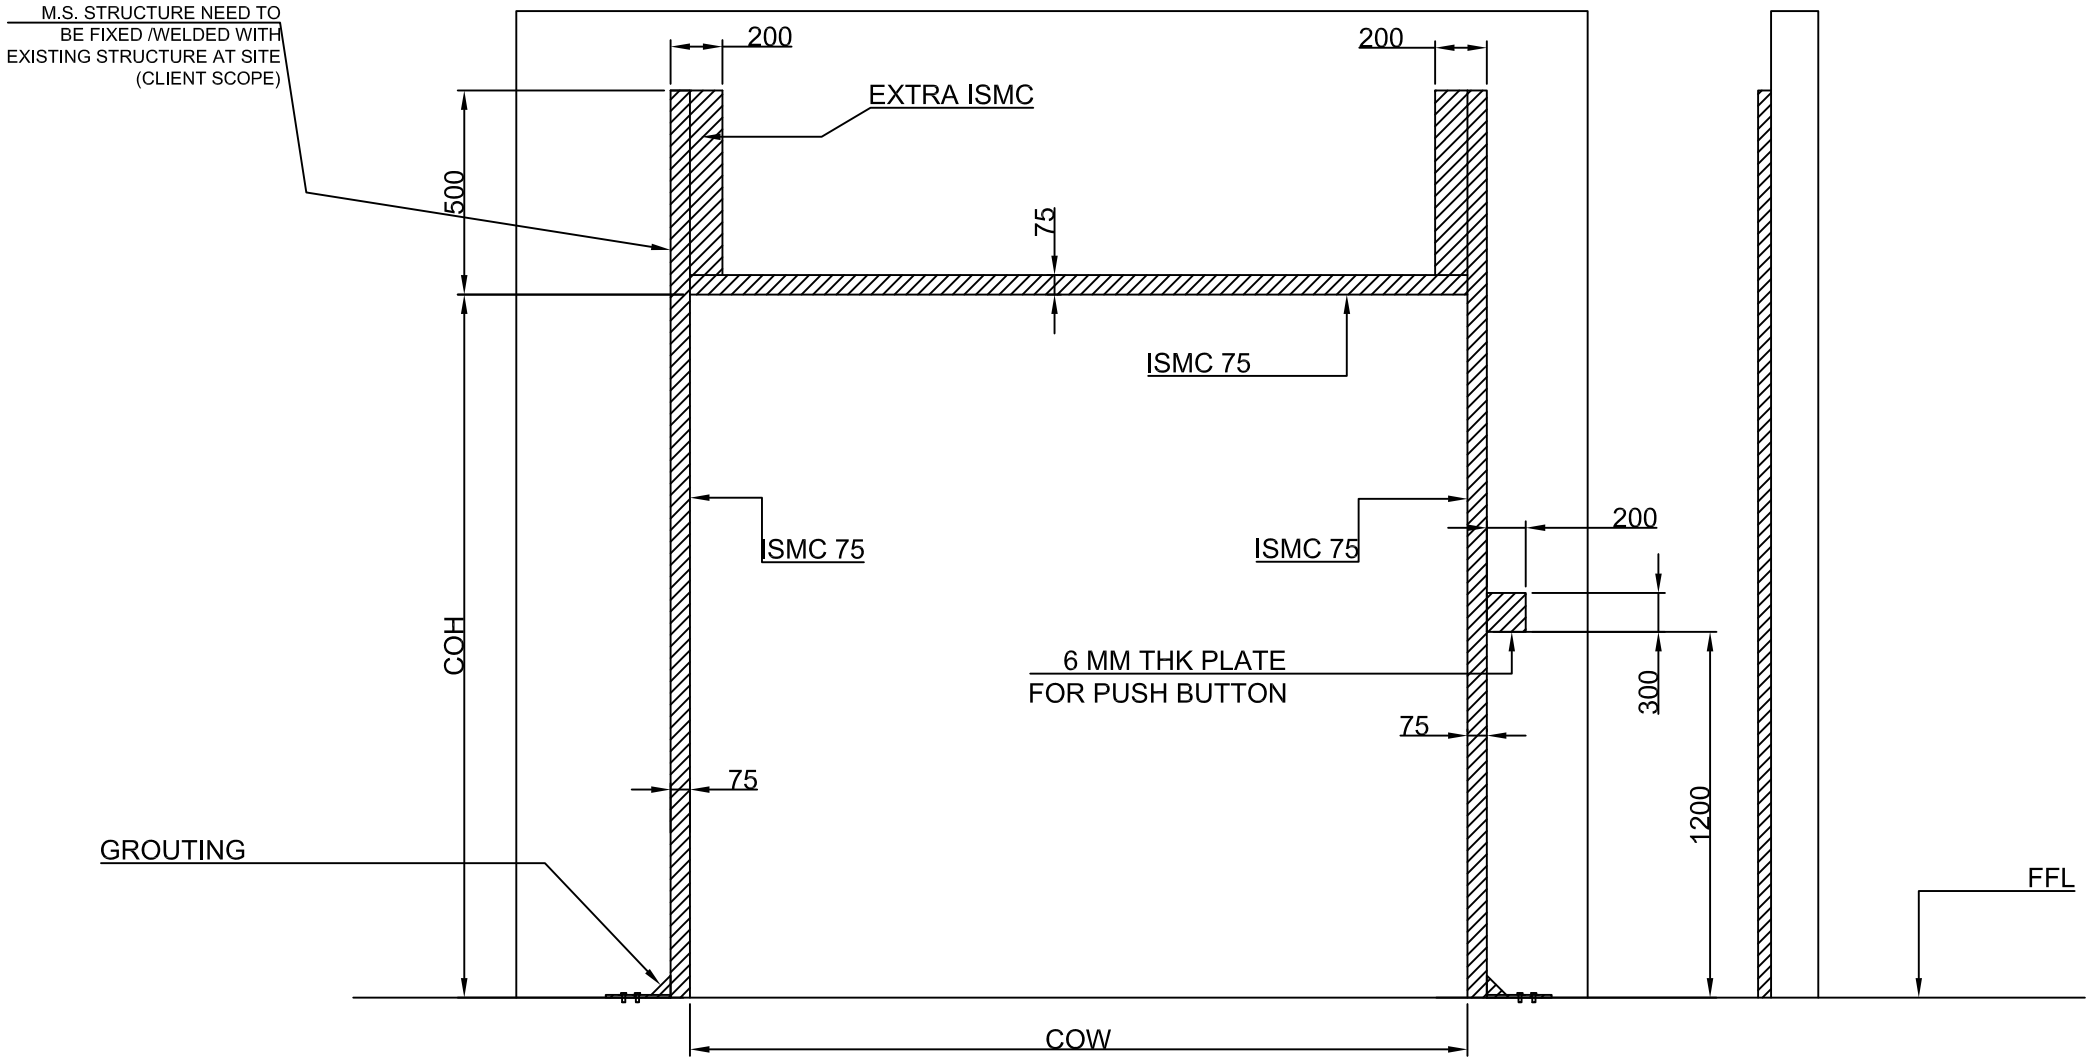



TOLERANCE:±10mm

This drawing & design is the property of NIHVA TECHNOLOGIES. Not to be sold or copied to any other concern.

| TITLE | | | | |
|---|---|---|---|---|
| M.S. STRUCTURE | | | | |
| | NAME | SIGN | DATE | |
| DRAWN | S.M.S. | | 15.1.2021 | CLIENT -SCON PROJECTS PVT LTD |
| CHECK | S.M. | | 15.1.2021 | PROJECT -INNOVATECH INDIA PVT LTD |
| APPROVAL | | | | SITE LOCATION - SANAND |
| If any queries contact : design@nihva.com | | | | DWG. NO. : NIHVA/20-21/0137 REV: 0 |
| ALL DIMENSION ARE IN mm | | | | SCALE: NTS WT: SHEET: 02 OF 02 |

NIHVA TECHNOLOGIES PVT. LTD. PUNE
Tel : 020 66304033
Email:- info@nihva.com
Website:- www.nihva.com

| SR NO | CLEAR OPENING WIDTH(COW) | CLEAR OPENING HEIGHT(COH | QTY | MOUNTING | MOTOR SIDE |
|---|---|---|---|---|---|
| 2 | 2500 | 3070 | 1 | INSIDE | RH |
| 1 | 2480 | 2980 | 1 | INSIDE | RH |

KINDLY NOTE THAT REQUIRED M.S. STRUCTURE , FITTING & ALL CIVIL WORK IS IN CLIENT SCOPE.