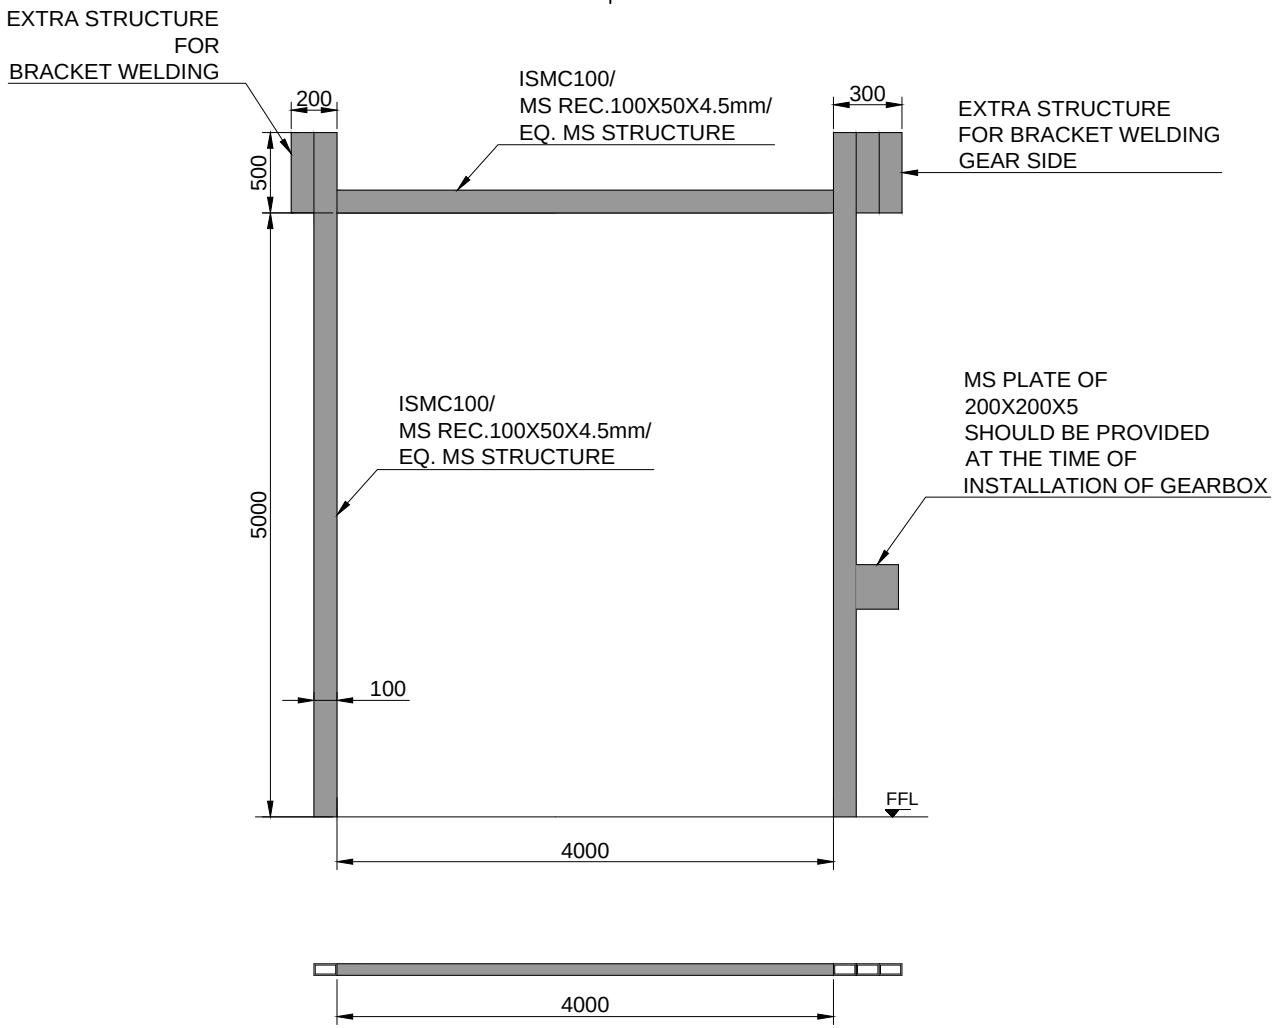


S.N.	LOCATION	SIZE	QUANTITY
1	B6A & B7E	4000(W)X5000(H)	02

NOTE-
1. ALL CIVIL WORK WILL BE CLIENT'S SCOPE.
2.STRUCTURE REQUIRED FOR SHUTTER IS IN CLIENT'S SCOPE.

TOLERANCE - ±10mm

This drawing & design is the property of NIHVA TECHNOLOGIES. Not to be sold or copied to any other concern.

TITLE: STRUCTURE FOR GEAR OPERATED ROLLING SHUTTER 4mX5m WITH RIGHT SIDE GEARBOX

NIHVA TECHNOLOGIES PVT. LTD.
NIHVA TECHNOLOGIES PVT. LTD, PUNE
Tel : 020 66304033
Email:- info@nihva.com
Website:- www.nihva.com

	NAME	SIGN	DATE
DRAWN	SURAJ		21.08.2018
CHECK	PRADEEP		21.08.2018
APPRD.	R.D		21.08.2018

CLIENT - INDOSPACE
PROJECT - BUILDING B6A & B7E
SITE LOCATION - CHAKAN 1
If any queries contact : design@nihva.com
DWG. NO. : NIHVA/18-19/0102
REV- 0
ALL DIMENSION ARE IN mm
SCALE: NTS
WT:
SHEET: 01 OF 01