




DETAIL 'A'

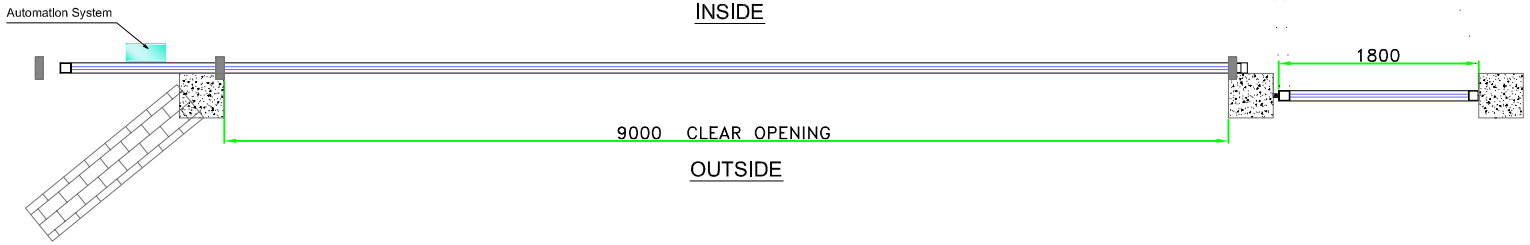

SLIDING GATE SIZE	= 10500 (W) X 1800 (H), QTY = 1NOS.
CLEAR OPENING	= 9,000 (W) X 1800 (H)
WICKET GATE SIZE	= 1800(W) X 1800 (H), QTY = 1NOS.
OUTER FRAME	= 100 X 50 X 3 mm
INNER FRAME	= 25 X 25 X 2.5 mm
GAP B/W FRAME	= 100 c/c
C'COLUMN(V) SUPPORT	= 4 NOS.
Total weight of sliding gate	= 625 kg (APPORX).

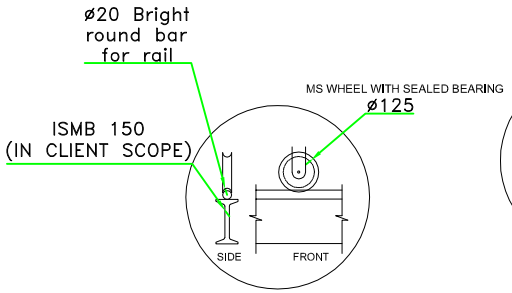

DETAIL 'B'

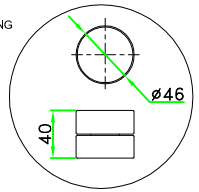

WICKET GATE HINGES DETAILS

This drawing & designing is the property of NIHVA TECHNOLOGIES. Not be sold or copy to any other concern.

TITLE

SLIDING GATE

CLIENT APPROVAL

ALL DIMENSION ARE IN mm

NIHVA TECHNOLOGIES PVT. LTD.

NIHVA TECHNOLOGY PVT. LTD. PUNE
Tel : 020 66304033
Email:- Info@nihva.com
Website:- www.nihva.com

	SIGN	DATE	
DRAWN	ABHIJIT	10/01/14	CLIENT - REWARD CONSTRUCTION
CHECK	ANIL	10/01/14	PROJECT -INGRERSOLL RAND
REV.	04		SITE -NARODA , GUJRAT
APPRD.			DWG. NO. - NVA/REWARD/D1/R2
MFG			SCALE: 01 | WT: | SHEET: 01
Ref. No.			If any queries contact : projects@nihva.com